



Департамент капитального ремонта города Москвы Государственное автономное учреждение города Москвы Московский научно-исследовательский и проектный институт жилищного хозяйства «МосжилНИИпроект» (ГАУ «МосжилНИИпроект»)

mgnp@mgnp.mos.ru +7 495 624 40 65 107078, г. Москва, ул. Каланчевская, д. 4/2, стр. 1

Арх. №

Капитальный ремонт здания Государственного бюджетного общеобразовательного учреждения города Москвы «Школа №1574», расположенного по адресу: г. Москва, пер. Старопименовский, д. 5

ПРОЕКТНАЯ ДОКУМЕНТАЦИЯ

Раздел 4. «Конструктивные решения»

2024-00375-01-0-КР.ВОР

Приложение к тому 4

1 этап

2025

Капитальный ремонт здания Государственного бюджетного общеобразовательного учреждения города Москвы «Школа №1574», расположенного по адресу: г. Москва, пер. Старопименовский, д. 5

ПРОЕКТНАЯ ДОКУМЕНТАЦИЯ

Раздел 4. «Конструктивные решения»

2024-00375-01-0-KP.BOP

Приложение к тому 4

1 этап

Заместитель директора



Н.Р. Нигматулин

11.12.24

Главный инженер проекта

Н.М. Пильгуй

11.12.24

Список работ приведен в разделе 2024-00375-01-0-КР.ТЧ пункт Д

Усиление внутренних стен в зоне расширяемых дверных проемов в подвале и в надземной части здания (2024-00375-01-0-КР.ТЧ. л.8)

№	Наименование вида работ	Объем работ			Обоснование объема работ
		Кол-во	Масса ед. кз.	Масса всех кз.	
1	Рама Рс-1, шт.	68	327.8	22290.4	2024-00375-01-0-КР листы 1-7, 19
2	Рама Рс-10.1, шт.	23	237.0	5451.0	2024-00375-01-0-КР листы 1-7, 19
3	Шпильки М16, шт.	1160	-	-	N=13*68+12*23; 2024-00375-01-0-КР листы 1-7, 19
4	Гайки с шайбами М16, шт.	2320	-	-	N=26*68+24*23; 2024-00375-01-0-КР листы 1-7, 19
5	Ремонтная смесь БИРС РМ (или аналог), м³	4.9			Объем при толщине заделки 15 мм 2024-00375-01-0-КР листы 1-7, 19
	<u>Устройство рамы Рс-1</u>				
	Г22п, l=п.м.	4.50	21.00	94.5	2024-00375-01-0-КР лист 19
	стойки L120x10, l=п.м.	9.28	18.24	169.3	2024-00375-01-0-КР лист 19
	L120x10, l=п.м.	4.14	18.24	75.5	2024-00375-01-0-КР лист 19
	L120x10, l=620*	4	11.31	45.2	2024-00375-01-0-КР лист 19
	-8x60, l=150, шт.	16	0.57	9.0	2024-00375-01-0-КР лист 19
	-8x60, l=620*, шт.	11	2.34	25.7	2024-00375-01-0-КР лист 19
	ребро -8x75, l=200, шт.	4	0.94	3.8	2024-00375-01-0-КР лист 19
			Итого:	423.0	
	Шпильки М16, l=730, шт.	13			2024-00375-01-0-КР лист 19
	Гайки с шайбами М16, шт.	26			2024-00375-01-0-КР лист 19
	<u>Устройство рамы Рс-10.1</u>				
	L160x10, l=п.м.	2.80	24.67	69.1	2024-00375-01-0-КР лист 19
	L120x10, l=750*	4	13.68	54.7	2024-00375-01-0-КР лист 19
	L120x10, l=п.м.	5.96	18.24	108.7	2024-00375-01-0-КР лист 19
	-8x60, l=150, шт.	8	0.57	4.5	2024-00375-01-0-КР лист 19
			Итого:	237.0	
	Шпильки М16, l=800, шт.	12			2024-00375-01-0-КР лист 19
	Гайки с шайбами М16, шт.	24			2024-00375-01-0-КР лист 19

						2024-00375-01-0-КР.ВОР	Лист
							1
Изм.	Кол.уч.	Лист	№ док.	Подпись	Дата		

Усиление наружных стен в зоне оконных проемов в надземной части здания в осях "1-16/В-М" (2024-00375-01-0-КР.ТЧ. л.8) (начало)

№	Наименование вида работ	Объем работ			Обоснование объема работ
		Кол-во	Масса ед. кз.	Масса всех кз.	
1	Рама Р0-2, шт.	16	173,7	2779.2	2024-00375-01-0-КР листы 1-7, 20
2	Рама Р0-3, шт.	17	219,0	3723.0	2024-00375-01-0-КР листы 1-7, 20
3	Рама Р0-4, шт.	38	377,6	14348.8	2024-00375-01-0-КР листы 1-7, 20
4	Рама Р0-5, шт.	107	204,4	21870.8	2024-00375-01-0-КР листы 1-7, 20
5	Шпильки М16, шт.	2848	-	-	N=17*14+38*18+18*107; 2024-00375-01-0-КР листы 1-7, 20
6	Гайки с шайбами М16, шт.	5696	-	-	N=17*28+38*36+36*107; 2024-00375-01-0-КР листы 1-7, 20
7	Г22п, л=п.м.	291.3	21,00	6117.30	Над Р0-5 по периметру стены 2024-00375-01-0-КР листы 2-6, 20
8	Ремонтная смесь БИРС РМ (или аналог), м³	8.9			Объем при толщине заделки 15 мм 2024-00375-01-0-КР листы 1-7, 20
	<u>Устройство рамы Р0-2</u>				
	обрамление L100x8, л=п.м.	8.4	12.25	102.9	2024-00375-01-0-КР лист 20
	L100x8, л=620*	4	7.60	30.4	2024-00375-01-0-КР лист 20
	-8x60, л=п.м.	5.8	3.77	21.7	2024-00375-01-0-КР лист 20
	-8x60, л=620*, шт.	8	2.34	18.7	2024-00375-01-0-КР лист 20
			Итого:	173.7	
	<u>Устройство рамы Р0-3</u>				
	обрамление L100x8, л=п.м.	12.6	12.25	153.9	2024-00375-01-0-КР лист 20
	L100x8, л=620*	4	7.60	30.4	2024-00375-01-0-КР лист 20
	-8x60, л=п.м.	2.4	3.77	9.0	2024-00375-01-0-КР лист 20
	-8x60, л=620*, шт.	11	2.34	25.7	2024-00375-01-0-КР лист 20
			Итого:	219.0	
	Шпильки М16, л=730, шт.	14			2024-00375-01-0-КР лист 20
	Гайки с шайбами М16, шт.	28			2024-00375-01-0-КР лист 20

Усиление наружных стен в зоне оконных проемов в надземной части здания в осях "1-16/В-М" (2024-00375-01-0-КР.ТЧ. л.8) (окончание)

№	Наименование вида работ	Объем работ			Обоснование объема работ
		Кол-во	Масса ед. кг.	Масса всех. кг	
	<u>Устройство рамы Р0-4</u>				
	L200x14, l=п.м.	3.7	42.80	157.5	2024-00375-01-0-КР лист 20
	обрамление L100x8, l=п.м.	12.1	12.25	148.0	2024-00375-01-0-КР лист 20
	L100x8, l=620*	4	7.60	30.4	2024-00375-01-0-КР лист 20
	-8x60, l=п.м.	2.4	3.77	9.0	2024-00375-01-0-КР лист 20
	-8x60, l=620*, шт.	14	2.34	32.7	2024-00375-01-0-КР лист 20
			Итого:	377.6	
	Шпильки М16, l=730, шт.	18			2024-00375-01-0-КР лист 20
	Гайки с шайбами М16, шт.	36			2024-00375-01-0-КР лист 20
	<u>Устройство рамы Р0-5</u>				
	обрамление L100x8, l=п.м.	11.6	12.25	141.6	2024-00375-01-0-КР лист 20
	L100x8, l=620*	4	7.60	30.4	2024-00375-01-0-КР лист 20
	-8x60, l=п.м.	2.4	3.77	9.0	2024-00375-01-0-КР лист 20
	-8x60, l=620*, шт.	10	2.34	23.4	2024-00375-01-0-КР лист 20
			Итого:	204.4	
	Шпильки М16, l=730, шт.	13			2024-00375-01-0-КР лист 20
	Гайки с шайбами М16, шт.	26			2024-00375-01-0-КР лист 20

Усиление стен в зоне пилонов в осях «И/15» и «И/15-16»
(2 пилон) (2024-00375-01-0-КР.ТЧ. л.9) (начало)

№	Наименование вида работ	Объем работ			Обоснование объема работ
		Кол-во	Масса ед. кг.	Масса всех. кг	
	<u>Усиление пилон в осях "И/15"</u>				
1	L200x14, l=п.м.	35.8	42.80	1532.2	2024-00375-01-0-КР лист 21
2	-10x120, l=п.м.	33.1	9.42	311.8	2024-00375-01-0-КР лист 21
3	L120x10, l=п.м.	17.9	18.24	326.5	2024-00375-01-0-КР лист 21
4	-10x120, l=630*	26	5.93	154.3	2024-00375-01-0-КР лист 21
5	-20x400, l=630*.	4	39.56	158.3	2024-00375-01-0-КР лист 21
6	-16x205, l=510.	4	13.13	52.5	2024-00375-01-0-КР лист 21
7	-20x300, l=550.	1	25.91	25.9	2024-00375-01-0-КР лист 21
8	-20x300, l=480.	2	22.61	45.2	2024-00375-01-0-КР лист 21
9	-30x540, l=770.	1	97.92	97.9	2024-00375-01-0-КР лист 21
10	пр. $\phi 30 \times 4$, l=п.м.	9.6	2.570	24.7	2024-00375-01-0-КР лист 21
	<u>Закладная деталь ЗД-2</u>	1	29.04	29.04	
11	L100x8, l=450.	2	5.51	11.0	2024-00375-01-0-КР лист 21
12	L100x8, l=660.	2	8.09	16.2	2024-00375-01-0-КР лист 21
13	Шпильки M27, l=500, шт.	10	0.18	1.8	2024-00375-01-0-КР лист 21
	<u>Закладная деталь ЗД-3</u>	4	20.94	83.76	
14	-20x320, l=400, шт.	4	20.10	80.4	2024-00375-01-0-КР лист 21
15	$\phi 10A500c$, l=680, шт.	8	0.420	3.4	2024-00375-01-0-КР лист 21
			Итого:	2842.1	
	<u>Погонная арматура/сетка</u>				
16	$\phi 20A240$, l=п.м.	213.2	2.470	526.6	2024-00375-01-0-КР лист 21
17	Сетка $\phi 5Bp1$ 50x50 ; м ²	6.0	6.16	36.96	2024-00375-01-0-КР лист 21
			Итого:	526.6	
18	Шпильки M20, l=750*, шт.	43			2024-00375-01-0-КР лист 21
19	Гайки с шайбами M20, шт.	206			43шт.*2+30шт.*2, где 43- гайки для шпилек M20 с 2х сторон, 30- гайки для горизонтальных тяжей с 2х сторон 2024-00375-01-0-КР лист 21
20	Гайки с шайбами M27, шт.	10			2024-00375-01-0-КР лист 21
21	Бетон кл. B25 ; м ³	1.0			1,93м ² *0.35м+0.63м*0.5м*0.25м*4шт., где 1,93м ² - площадь МП2, 0,35м - толщина МП2, 0,63*0,5*0,25-размеры МП1, 4-кол-во МП1. 2024-00375-01-0-КР лист 21, лист 2 узел В
					Лист
					4
Изм.	Кол.уч.	Лист	№ док.	Подпись	Дата

2024-00375-01-0-КР.ВОР

Усиление стен в зоне пилонов в осях «И/15» и «И/15-16»
(2 пилон) (2024-00375-01-0-КР.ТЧ. л.9) (продолжение)

№	Наименование вида работ	Объем работ			Обоснование объема работ
		Кол-во	Масса ед. кг.	Масса всех. кг	
	<u>Усиление пилона в осях "И/15-16"</u>				
1	L160x10, l=п.м.	44.6	24.67	1100.3	2024-00375-01-0-КР лист 22
2	-20x160, l=п.м.	60.6	25.12	1522.3	2024-00375-01-0-КР лист 22
3	-10x120, l=п.м.	44.8	9.42	422.0	2024-00375-01-0-КР лист 22
4	-10x120, l=750*	39	7.07	275.5	2024-00375-01-0-КР лист 22
5	-20x400, l=670*.	4	42.08	168.3	2024-00375-01-0-КР лист 22
6	-16x205, l=510.	4	13.13	52.5	2024-00375-01-0-КР лист 22
7	L200x14, l=750*	1	32.10	32.1	2024-00375-01-0-КР лист 22, узел 7 по ширине пилонa
8	-10x180, l=180	2	2.54	5.1	2024-00375-01-0-КР лист 22
9	L100x8, l=п.м.	9.8	12.25	120.5	2024-00375-01-0-КР лист 22
10	тр. Ø30x4, l=п.м.	13.1	2.570	33.7	2024-00375-01-0-КР лист 22
	<u>Закладная деталь ЗД-З</u>	4	20.94	83.76	
11	-20x320, l=400, шт.	4	20.10	80.4	2024-00375-01-0-КР лист 22
12	Ø10A500с, l=680, шт.	8	0.420	3.4	2024-00375-01-0-КР лист 22
			Итого:	3816.1	
	<u>Погонная арматура/сетка</u>				
13	Ø20A240, l=п.м.	213.2	2.470	526.6	2024-00375-01-0-КР лист 22
14	Сетка Ø5ВрI 50x50 ; м²	6.0	6.16	36.96	2024-00375-01-0-КР лист 22
			Итого:	563.6	
15	Шпильки М20, l=900*, шт.	78			2024-00375-01-0-КР лист 22
16	Гайки с шайбами М20, шт.	340			2024-00375-01-0-КР лист 22
17	Бетон кл. В25 ; м³	0.4			2024-00375-01-0-КР лист 22
	<u>Устройство плиты толщиной 350 мм</u>				
18	Ø16 А500С, L=1110, шт	7	1,75	12,25	2024-00375-01-0-КР лист 22
19	Ø12 А500С, L=890, шт	3	0,79	2,37	2024-00375-01-0-КР лист 22
20	Скоба из Ø16А500С, L=1450, шт.	12	2,29	27,48	2024-00375-01-0-КР лист 22
21	Скоба из Ø12А500С, L=1500, шт.	2	1,33	2,66	2024-00375-01-0-КР лист 22
	<u>Материалы</u>				
22	Бетон кл. В25, м³ (плита толщ.350мм)	0.36	-	-	2024-00375-01-0-КР лист 22

Усиление стен в зоне пилонов в осях «И/15» и «И/15-16»
(2 пилон) (2024-00375-01-0-КР.ТЧ. л.9) (окончание)

№	Наименование вида работ	Объем работ			Обоснование объема работ
		Кол-во	Масса ед. кг.	Масса всех. кг	
	<u>Устройство стен толщиной 200 мм</u>				
	<u>Стены толщ.200мм</u>				
23	Ø16 А500С, L=3670, шт.	18	5,79	104,22	2024-00375-01-0-КР лист 22
24	Ø16 А500С, L=3900, шт	24	6,15	147,60	2024-00375-01-0-КР лист 22
			Итого:	251,82	
25	Ø12 А500С, норм. дл., поз.м.	195,0	0,888	173,16	2024-00375-01-0-КР лист 22
26	Скоба из Ø12А500С, L=1340, шт.	73	0,37	27,01	2024-00375-01-0-КР лист 22
27	Скоба из Ø16А500С, L=3470, шт.	5	0,38	1,90	2024-00375-01-0-КР лист 22
28	Скоба из Ø16А500С, L=3270, шт.	5	0,38	1,90	2024-00375-01-0-КР лист 22
29	Скоба из Ø16А500С, L=2300, шт.	2	0,38	0,76	2024-00375-01-0-КР лист 22
30	Скоба из Ø16А500С, L=2200, шт.	2	0,38	0,76	2024-00375-01-0-КР лист 22
31	Шпилька из Ø6А240, L=275, шт.	207	0,06	12,42	2024-00375-01-0-КР лист 22
	<u>Материалы</u>				
32	Бетон кл. В25, м ³ (стены)	4.2	-	-	4.21м*0.2м*3.8м+0,6м*0,75м*0,4м*4шт.+ +0,5м*0,63м*0,25м*4шт. , где 4.21 – протяженность стен, 0.2 – толщина стен, 3,8–высота стен, 0,6*0,75*0,4 – размеры сквозных гнезд в кирпичной стене, 4 – количество сквозных гнезд в кирпичной стене, 0,5*0,63*0,25 – размеры МПЗ, 4 – количество МПЗ. 2024-00375-01-0-КР лист 22, лист 1 узел Г
	<u>“Зачеканка” зазоров между элементами рамы усиления ремонтной смесью БИРС РМ (или аналогом)</u>				
33	- пилон в осях “И/15”, м ³	0.23			Объем при толшина заделки 15 мм, 2024-00375-01-0-КР лист 21
34	- пилон в осях “И/15-16”, м ³	0.21			Объем при толшина заделки 15 мм, 2024-00375-01-0-КР лист 22

Замена перекрытий в осях «1-16/В-М»
(2024-00375-01-0-КР.ТЧ. л.9) (начало)

№	Наименование вида работ	Объем работ			Обоснование объема работ
		Кол-во	Масса ед. кз.	Масса всех кз.	
	<u>Замена перекрытий над подвалом</u>				
1	45Ш1, l=п.м.	156.70	123.60	19368.1	2024-00375-01-0-КР листы 8, 14
2	35Ш1, l=п.м.	114.56	65.30	7480.4	2024-00375-01-0-КР листы 8, 14
3	30Ш1, l=п.м.	113.98	56.80	6473.8	2024-00375-01-0-КР листы 8, 14
4	Г22п, l=п.м.	176.9	21.00	3715.5	2024-00375-01-0-КР листы 8, 14
5	Г18п, l=п.м.	78.26	16.30	1275.6	2024-00375-01-0-КР листы 8, 14
6	L100x8, l=п.м.	339.04	12.25	4153.2	2024-00375-01-0-КР листы 8, 14
7	-10x200, l=350, шт.	182	5.50	1000.1	2024-00375-01-0-КР листы 8, 14
8	-10x120, l=310, шт.	112	2.92	327.1	2024-00375-01-0-КР листы 8, 14
9	-10x400, l=144, шт.	74	4.36	322.4	2024-00375-01-0-КР листы 8, 14
10	-10x100, l=270, шт.	139	2.12	294.6	2024-00375-01-0-КР листы 8, 14
11	-10x200, l=75, шт.	8	1.18	9.4	2024-00375-01-0-КР листы 8, 14
12	-10x160, l=85, шт.	82	1.07	87.5	2024-00375-01-0-КР листы 8, 14
13	-10x160, l=60, шт.	26	0.75	19.6	2024-00375-01-0-КР листы 8, 14
			Итого:	44527.3	
14	Бетон кл. В25 на мелком заполнителе (бетонная подушка); м³	10.4			2024-00375-01-0-КР лист 8, лист 14 сечение Г-Г
15	Сетка Ø5Врl 50x50 ; м²	48.8	6.16	300.8	2024-00375-01-0-КР листы 8, 14
16	профнастил Н75-750-0.8, м²	676.9	11.20	7581.4	2024-00375-01-0-КР листы 8, 14
17	Сетка Ø5Врl 100x100 ; м²	676.9	3.08	2084.9	2024-00375-01-0-КР листы 8, 14
18	Арматура Ø10А500С ; пм	11291.5	0.617	6966.9	2024-00375-01-0-КР листы 8, 14
19	Бетон (плита перекрытия) кл. В25; м³	81.9			2024-00375-01-0-КР листы 8, 14

						2024-00375-01-0-КР.ВОР	Лист
							7
Изм.	Кол.уч.	Лист	№ док.	Подпись	Дата		

Замена перекрытий в осях «1-16/В-М» (2024-00375-01-0-КР.ТЧ. л.9) (продолжение)

№	Наименование вида работ	Объем работ			Обоснование объема работ
		Кол-во	Масса ед. кз.	Масса всех кз	
	<u>Замена перекрытий над 1 этажом</u>				
20	45Ш1, l=п.м.	291.71	123.60	36055.1	2024-00375-01-0-КР лист 9, 14
21	35Ш1, l=п.м.	68.13	65.30	4448.9	2024-00375-01-0-КР лист 9, 14
22	30Ш1, l=п.м.	137.18	56.80	7791.8	2024-00375-01-0-КР лист 9, 14
23	С22п, l=п.м.	185	21.00	3877.6	2024-00375-01-0-КР лист 9, 14
24	С18п, l=п.м.	34.07	16.30	555.3	2024-00375-01-0-КР лист 9, 14
25	Л100х8, l=п.м.	60.66	12.25	743.1	2024-00375-01-0-КР лист 9, 14
26	-10х200, l=350, шт.	181	5.50	994.6	2024-00375-01-0-КР лист 9, 14
27	-10х120, l=310, шт.	38	2.92	111.0	2024-00375-01-0-КР лист 9, 14
28	-10х400, l=144, шт.	153	4.52	691.8	2024-00375-01-0-КР лист 9, 14
29	-10х160, l=210, шт.	4	2.64	10.6	2024-00375-01-0-КР лист 9, 14
30	-10х100, l=270, шт.	104	2.12	220.4	2024-00375-01-0-КР лист 9, 14
31	-10х200, l=75, шт.	6	1.18	7.1	2024-00375-01-0-КР лист 9, 14
32	-10х160, l=85, шт.	90	1.07	96.1	2024-00375-01-0-КР лист 9, 14
33	-10х160, l=60, шт.	2	0.75	1.5	2024-00375-01-0-КР лист 9, 14
			Итого:	55604.8	
34	Бетон кл. В25 на мелком заполнителе (бетонная подушка); м³	11.8			2024-00375-01-0-КР лист 9, 14
35	Сетка Ø5Врl 50х50 ; м²	57.0	6.16	351.2	2024-00375-01-0-КР лист 9, 14
36	профнастил Н75-750-0.8, м²	735.9	11.20	8242.5	2024-00375-01-0-КР лист 9, 14
37	Сетка Ø5Врl 100х100 ; м²	735.9	3.08	2266.7	2024-00375-01-0-КР лист 9, 14
38	Арматура Ø10А500С ; пм	12274.8	0.617	7573.6	2024-00375-01-0-КР лист 9, 14
39	Бетон (плита перекрытия) кл. В25; м³	89.0			2024-00375-01-0-КР лист 9, 14

						2024-00375-01-0-КР.ВОР	Лист
							8
Изм.	Кол.уч.	Лист	№ док.	Подпись	Дата		

Замена перекрытий в осях «1-16/В-М»
(2024-00375-01-0-КР.ТЧ. л.9) (продолжение)

№	Наименование вида работ	Объем работ			Обоснование объема работ
		Кол-во	Масса ед. кз.	Масса всех кз	
	<u>Замена перекрытий над 2 этажом</u>				
40	45Ш1, l=п.м.	330.81	123.60	40888.6	2024-00375-01-0-КР лист 10, 14
41	40Ш1, l=п.м.	99.40	88.60	8806.8	2024-00375-01-0-КР лист 10, 14
42	35Ш1, l=п.м.	110.94	65.30	7244.4	2024-00375-01-0-КР лист 10, 14
43	30Ш1, l=п.м.	63.05	56.80	3581.0	2024-00375-01-0-КР лист 10, 14
44	С22п, l=п.м.	23.55	21.00	494.6	2024-00375-01-0-КР лист 10, 14
45	С18п, l=п.м.	54.27	16.30	884.5	2024-00375-01-0-КР лист 10, 14
46	Л100х8, l=п.м.	65.22	12.25	798.9	2024-00375-01-0-КР лист 10, 14
47	-10х200, l=350, шт.	147	5.50	807.8	2024-00375-01-0-КР лист 10, 14
48	-10х160, l=60, шт.	8	2.64	21.1	2024-00375-01-0-КР лист 10, 14
49	-10х120, l=310, шт.	74	2.92	216.1	2024-00375-01-0-КР лист 10, 14
50	-10х300, l=185, шт.	12	4.36	52.3	2024-00375-01-0-КР лист 10, 14
51	-10х400, l=144, шт.	181	4.36	788.6	2024-00375-01-0-КР лист 10, 14
52	-10х160, l=210, шт.	4	2.64	10.6	2024-00375-01-0-КР лист 10, 14
53	-10х100, l=270, шт.	54	2.12	114.5	2024-00375-01-0-КР лист 10, 14
54	-10х140, l=358, шт.	52	1.18	61.2	2024-00375-01-0-КР лист 10, 14
55	-10х160, l=85, шт.	96	1.07	102.5	2024-00375-01-0-КР лист 10, 14
			Итого:	64873.3	
56	Бетон кл. В25 на мелком заполнителе (бетонная подушка); м³	10.5			2024-00375-01-0-КР лист 10, лист 14 сечение Г-Г
57	Сетка Ø5Врl 50х50 ; м²	46.3	6.16	285.2	2024-00375-01-0-КР лист 10, 14
58	профнастил Н75-750-0.8, м²	835.8	11.20	9361.0	2024-00375-01-0-КР лист 10, 14
59	Сетка Ø5Врl 100х100 ; м²	835.8	3.08	2574.3	2024-00375-01-0-КР лист 10, 14
60	Арматура Ø10А500С ; пм	1394.1	0.617	8601.7	2024-00375-01-0-КР лист 10, 14
61	Бетон (плита перекрытия) кл. В25; м³	101.1			2024-00375-01-0-КР лист 10, 14

Замена перекрытий в осях «1-16/В-М»
(2024-00375-01-0-КР.ТЧ. л.9) (продолжение)

№	Наименование вида работ	Объем работ			Обоснование объема работ
		Кол-во	Масса ед. кз.	Масса всех кз.	
	<u>Замена перекрытий над 3 этажом</u>				
62	45Ш1, l=п.м.	325.09	123.60	40181.4	2024-00375-01-0-КР лист 11, 14
63	35Ш1, l=п.м.	156.67	65.30	10230.6	2024-00375-01-0-КР лист 11, 14
64	30Ш1, l=п.м.	27.62	56.80	1568.8	2024-00375-01-0-КР лист 11, 14
65	Г22п, l=п.м.	9.00	21.00	189.0	2024-00375-01-0-КР лист 11, 14
66	Г18п, l=п.м.	63.85	16.30	1040.8	2024-00375-01-0-КР лист 11, 14
67	L100x8, l=п.м.	268.49	12.25	3289.0	2024-00375-01-0-КР лист 11, 14
68	-10x200, l=350, шт.	112	5.50	615.4	2024-00375-01-0-КР лист 11, 14
69	-10x160, l=210, шт.	6	2.64	15.8	2024-00375-01-0-КР лист 11, 14
70	-10x120, l=310, шт.	100	2.92	292.0	2024-00375-01-0-КР лист 11, 14
71	-10x300, l=185, шт.	8	4.36	34.9	2024-00375-01-0-КР лист 11, 14
72	-10x400, l=144, шт.	177	4.36	771.1	2024-00375-01-0-КР лист 11, 14
73	-10x100, l=270, шт.	30	2.12	63.6	2024-00375-01-0-КР лист 11, 14
74	-10x160, l=85, шт.	78	1.07	83.3	2024-00375-01-0-КР лист 11, 14
			Итого:	58375.6	
75	Бетон кл. В25 на мелком заполнителе (бетонная подушка); м³	9.0			2024-00375-01-0-КР лист 11, лист 14 сечение Г-Г
76	Сетка Ø5Врl 50x50 ; м²	35.3	6.16	217.3	2024-00375-01-0-КР лист 11, 14
77	профнастил Н75-750-0.8, м²	838.5	11.20	9391.3	2024-00375-01-0-КР лист 11, 14
78	Сетка Ø5Врl 100x100 ; м²	838.5	3.08	2582.6	2024-00375-01-0-КР лист 11, 14
79	Арматура Ø10А500С ; пм	13986.7	0.617	8629.8	2024-00375-01-0-КР лист 11, 14
80	Бетон (плита перекрытия) кл. В25; м³	101.5			2024-00375-01-0-КР лист 11, 14

						2024-00375-01-0-КР.ВОР	Лист
							10
Изм.	Кол.уч.	Лист	№ док.	Подпись	Дата		

Замена перекрытий в осях «1-16/В-М»
(2024-00375-01-0-КР.ТЧ. л.9) (продолжение)

№	Наименование вида работ	Объем работ			Обоснование объема работ
		Кол-во	Масса ед. кз.	Масса всех кз	
	<u>Замена перекрытий над 4 этажом</u>				
81	45Ш1, l=п.м.	331.68	123.60	40996.0	2024-00375-01-0-КР лист 12, 14
82	35Ш1, l=п.м.	116.58	65.30	7612.7	2024-00375-01-0-КР лист 12, 14
83	30Ш1, l=п.м.	62.16	56.80	3530.7	2024-00375-01-0-КР лист 12, 14
84	С22п, l=п.м.	9.78	21.00	205.4	2024-00375-01-0-КР лист 12, 14
85	С18п, l=п.м.	62.95	16.30	1026.1	2024-00375-01-0-КР лист 12, 14
86	L100x8, l=п.м.	85.70	12.25	1049.8	2024-00375-01-0-КР лист 12, 14
87	-10x200, l=350, шт.	104	5.50	571.5	2024-00375-01-0-КР лист 12, 14
88	-10x160, l=210, шт.	6	2.64	15.8	2024-00375-01-0-КР лист 12, 14
89	-10x120, l=310, шт.	60	2.92	175.2	2024-00375-01-0-КР лист 12, 14
90	-10x300, l=185, шт.	8	4.36	34.9	2024-00375-01-0-КР лист 12, 14
91	-10x400, l=144, шт.	175	4.36	762.4	2024-00375-01-0-КР лист 12, 14
92	-10x100, l=270, шт.	46	2.12	97.5	2024-00375-01-0-КР лист 12, 14
93	-10x160, l=85, шт.	80	1.07	85.4	2024-00375-01-0-КР лист 12, 14
			Итого:	56163.4	
94	Бетон кл. В25 на мелком заполнителе (бетонная подушка); м³	7.8			2024-00375-01-0-КР лист 12, лист 14 сечение Г-Г
95	Сетка Ø5Врl 50x50 ; м²	32.8	6.16	201.8	2024-00375-01-0-КР лист 12, 14
96	профнастил Н75-750-0.8, м²	857.1	11.20	9599.9	2024-00375-01-0-КР лист 12, 14
97	Сетка Ø5Врl 100x100 ; м²	857.1	3.08	2640.0	2024-00375-01-0-КР лист 12, 14
98	Арматура Ø10А500С ; пм	14295.8	0.617	8820.5	2024-00375-01-0-КР лист 12, 14
99	Бетон (плита перекрытия) кл. В25; м³	103.0			2024-00375-01-0-КР лист 12, 14

						2024-00375-01-0-КР.ВОР	Лист
							11
Изм.	Кол.уч.	Лист	№ док.	Подпись	Дата		

Замена перекрытий в осях «1-16/В-М»
(2024-00375-01-0-КР.ТЧ. л.9) (окончание)

№	Наименование вида работ	Объем работ			Обоснование объема работ
		Кол-во	Масса ед. кз.	Масса всех кз.	
	<u>Замена перекрытий над 5 этажом</u>				
100	45Ш1, l=п.м.	331.68	123.60	40996.0	2024-00375-01-0-КР лист 13, 14
101	35Ш1, l=п.м.	103.55	65.30	6761.8	2024-00375-01-0-КР лист 13, 14
102	30Ш1, l=п.м.	62.16	56.80	3530.7	2024-00375-01-0-КР лист 13, 14
103	С22п, l=п.м.	4.89	21.00	102.7	2024-00375-01-0-КР лист 13, 14
104	С18п, l=п.м.	77.66	16.30	1265.8	2024-00375-01-0-КР лист 13, 14
105	L100x8, l=п.м.	85.70	12.25	1049.8	2024-00375-01-0-КР лист 13, 14
106	-10x200, l=350, шт.	99	5.50	544.0	2024-00375-01-0-КР лист 13, 14
107	-10x160, l=210, шт.	5	2.64	13.2	2024-00375-01-0-КР лист 13, 14
108	-10x120, l=310, шт.	68	2.92	198.6	2024-00375-01-0-КР лист 13, 14
109	-10x300, l=185, шт.	8	4.36	34.9	2024-00375-01-0-КР лист 13, 14
110	-10x400, l=144, шт.	175	4.36	762.4	2024-00375-01-0-КР лист 13, 14
111	-10x100, l=270, шт.	49	2.12	103.9	2024-00375-01-0-КР лист 13, 14
112	-10x160, l=85, шт.	32	1.07	34.2	2024-00375-01-0-КР лист 13, 14
			Итого:	55397.9	
113	Бетон кл. В25 на мелком заполнителе (бетонная подушка); м³	8.3			2024-00375-01-0-КР лист 13, лист 14 сечение Г-Г
114	Сетка Ø5Врl 50x50 ; м²	31.2	6.16	192.1	2024-00375-01-0-КР лист 13, 14
115	профнастил Н75-750-0.8, м²	858.3	11.20	9613.0	2024-00375-01-0-КР лист 13, 14
116	Сетка Ø5Врl 100x100 ; м²	858.3	3.08	2643.6	2024-00375-01-0-КР лист 13, 14
117	Арматура Ø10А500С ; пм	14315.3	0.617	8832.5	2024-00375-01-0-КР лист 13, 14
118	Бетон (плита перекрытия) кл. В25; м³	103.1			2024-00375-01-0-КР лист 13, 14

Замена отдельных плит перекрытий в осях «18-21/А-К»
(2024-00375-01-0-КР.ТЧ. л.10)

№	Наименование вида работ	Объем работ			Обоснование объема работ
		Кол-во	Масса ед. кг.	Масса всех кг.	
	<u>Демонтаж монолитных участков и плит типа НВ (ПРТ) и вырубка отверстий в плитах ТТ</u>				
1	Бетон кл. В25 (демонтаж), м³	18.00	-	-	2024-00375-01-0-КР лист 15-18
2	Бетон кл. В25 (вырубка отверстий), м³	0.10	-	-	2024-00375-01-0-КР лист 15-18
	<u>Устройство монолитных участков плит</u>				
3	С24п, L=п.м.	254.5	24,00	6108.0	2024-00375-01-0-КР лист 15-18
4	Уголок L160x10, L=1200, шт.	40	29.60	1184.2	2024-00375-01-0-КР лист 15-18
5	-8x80, L=220	72	1.11	79.6	2024-00375-01-0-КР лист 15-18
6	-8x80, L=200	50	1.00	50.2	2024-00375-01-0-КР лист 15-18
7	-8x60, L=200	40	0.75	30.1	2024-00375-01-0-КР лист 15-18
			Итого:	7452.1	
8	Бетон кл. В25 (плиты δ=60/120мм), м³	10.4	-	-	2024-00375-01-0-КР лист 15-18
9	Подбетонка из ЦПР, δ=60, м³	0.18	-	-	2024-00375-01-0-КР лист 15-18
10	Профнастил Н75-750-0.8, м²	136.80	-	-	2024-00375-01-0-КР лист 15-18
11	Хим. анкер HILTI HIT-HY270, мл	-	-	-	2024-00375-01-0-КР лист 15-18
12	Шпилька М16, L, м.п.	14.4	-	-	L=72 шт.*0,2 м, где 72- количество отверстий, 0,2 - длина шпильки. 2024-00375-01-0-КР лист 15-18
13	Шпилька М16, L, м.п.	0.6	-	-	L=2 шт.*0,3 м, где 2- количество отверстий, 0,3 - длина шпильки. 2024-00375-01-0-КР лист 15-18
14	Гайка М16, шт.	74	-	-	2024-00375-01-0-КР лист 15-18

Замена лестницы в осях «11-13/Ж-Л»(2024-00375-01-0-КР.ТЧ. л.10)

№	Наименование вида работ	Объем работ			Обоснование объема работ
		Кол-во	Масса ед. кз.	Масса всех кз.	
1	Ø12 А500С, м.п	455.6	0.888	404.61	2024-00375-01-0-КР лист 25, 26
2	Ø8 А500С, м.п	216.90	0.395	85.68	2024-00375-01-0-КР лист 25, 26
3	Ø20 А500С, L=2910	12	7.176	86.11	2024-00375-01-0-КР лист 25, 26
4	Ø16 А500С, L=2910	10	4.592	45.92	2024-00375-01-0-КР лист 25, 26
5	Ø12 А500С, L=2910	4	2.584	10.34	2024-00375-01-0-КР лист 25, 26
6	Скоба из Ø8 А500С, L=725, шт.	62	0.29	17.76	2024-00375-01-0-КР лист 25, 26
7	Скоба из Ø8 А500С, L=770, шт.	40	0.30	12.17	2024-00375-01-0-КР лист 25, 26
8	Скоба из Ø8 А240, L=690, шт.	50	0.27	13.63	2024-00375-01-0-КР лист 25, 26
9	Скоба из Ø8 А240, L=1030, шт.	75	0.41	30.51	2024-00375-01-0-КР лист 25, 26
10	Сетка Ø5 Вр-I 100х100, м²	25.06	2.0	50.13	2024-00375-01-0-КР лист 25, 26
		Итого:		751.81	
11	Бетон В25, м³	5.22			2024-00375-01-0-КР лист 25, 26

Ремонт рустов плит перекрытий в пристройке в осях «18-21/А-К». Ремонт сколов бетона защитного слоя плит перекрытий, покрытия и внутренних лестничных маршей (2024-00375-01-0-КР.ТЧ. л.11)

№	Наименование вида работ	Объем работ			Обоснование объема работ
		Кол-во	Масса ед. кз.	Масса всех кз.	
	<u>Заделка рустов</u>				
1	Цементно-песчаный раствор М200, м³	6,48	-	-	V=810 п.м * 0.008м², где 810-протяженность рустов, 0.008-площадь сечения ЦПР М200; 2024-00375-01-0-КР листы 15-18, 23, ТЗК
2	Ремонтный состав Бирсс РСМ-2 М350 (или аналог), м³	1,13	-	-	V=0.0014 м²*810 п.м, где 2295-протяженность рустов, 0.0014-площадь сечения ремонтного состава; 2024-00375-01-0-КР листы 15-18, 23, ТЗК
	<u>Ремонтные работы при глубине скола до 30 мм</u>				
3	Ремонтный состав Бирсс РСМ-2 М350 (или аналог), м³	0,0015	-	-	V=0.03 м * 0.05 м²*1 м², где: 0.05-площадь разрушения бетона на лестницах, 1-площадь разрушения бетона плит. 2024-00375-01-0-КР лист 23, ТЗК дефек.бедомость п. 4,5,7

Замена бетонных оснований полов подвала с одновременным устройством гидроизоляции (начало) (2024-00375-01-0-КР.ТЧ. л.11)

№	Наименование вида работ	Объем работ			Обоснование объема работ
		Кол-во	Масса ед. кз	Масса всех кз	
1	Ø8A500с, l=п.м.	46.1	0.395	18.2	2024-00375-01-0-КР лист 24
2	Ø12A500с, l=п.м.	13306.7	0.888	11816.3	2024-00375-01-0-КР лист 24
3	Скоба, Ø8A500с, l=885, шт.	3757	0.35	1313.35	2024-00375-01-0-КР лист 24
4	Скоба, Ø8A500с, l=270, шт.	3618	0.11	385.86	2024-00375-01-0-КР лист 24
5	Скоба, Ø12A500с, l=1875, шт.	30	1.67	49.95	2024-00375-01-0-КР лист 24
6	Скоба, Ø8A500с, l=875, шт.	30	0.35	10.37	2024-00375-01-0-КР лист 24
7	Скоба, Ø8A500с, l=895, шт.	32	0.35	11.31	2024-00375-01-0-КР лист 24
8	Скоба, Ø6A240, l=240, шт.	28	0.05	1.49	2024-00375-01-0-КР лист 24
			Всего:	13606.9	
9	Бетон кл. В25, W6; м³	188.9	-	-	$V=V1+V2+V3+V4$, где: Плита пола толщиной 150 мм: $V1=800.15 \text{ м}^2 \cdot 0.15 \text{ м}$, где 800.15 – площадь плиты пола. Плита пола толщиной 350 мм: $V2=34.5 \text{ м}^2 \cdot 0.35 \text{ м}$, где 34.5 – площадь плиты пола. Плавающий пол толщиной 150 мм: $V3=361.35 \text{ м}^2 \cdot 0.15 \text{ м}$, где 361.35 – площадь плиты плавающего пола. Стены прямка: $V4=0.8 \text{ м} \cdot 3.2 \text{ м}^2$, где 3.2 м² – площадь стен, 0.8 м – высота стен. 2024-00375-01-0-КР лист 24
10	Сетка Ø5Вр1 100x100 ; м²	1196.0	3.08	3683.6	$S=834.64 \text{ м}^2 + 361.35 \text{ м}^2$, где 834.64 – площадь плиты пола, 361.35 – площадь плавающего пола. 2024-00375-01-0-КР лист 24
11	Жгут "Вилатерм" Ø20 (или аналог); м	548.4	-	-	$L=548.4 \text{ м}$ – Вилатерм Ø20 по периметру пола. 2024-00375-01-0-КР лист 24
12	Жгут "Вилатерм" Ø40 (или аналог); м	202.5	-	-	$L=202.5 \text{ м}$ – Вилатерм Ø40 по периметру плавающего пола. 2024-00375-01-0-КР лист 24
13	Пенополистирол Ø20 ; м³	1.6	-	-	2024-00375-01-0-КР лист 24
15	Planter standard (или аналог); м²	1196.0	-	-	$S=834.64 \text{ м}^2 + 361.35 \text{ м}^2$, где 834.64; 361.35 – площади устраиваемых полов. 2024-00375-01-0-КР лист 24
16	Минераловатная плита Rockwool Флор Баттс Оптима, тощ. 40 мм (или аналог); м³	1.2	-	-	$V=202.5 \text{ м} \cdot 0.04 \text{ м} \cdot 0.15 \text{ м}$, где 202.5 – площадь плавающего пола, 0.15 – высота сечения. 2024-00375-01-0-КР лист 24
	Устройство горизонтальной оклеечной гидроизоляции в подвале с учетом захода на стены				
17	Устройство горизонтальной оклеечной гидроизоляции в подвале, м²	1571.5	-	-	$S=1196 \text{ м}^2 + 751 \cdot 0.5 \text{ м}^2$, где 1196 – площадь пола, 751 – длина захода на стены шириной 0.5 м; 2024-00375-01-0-КР лист 24
18	Стяжка из цементно-песчаного раствора марки М200 толщиной 40мм, м³	47.8	-	-	$V=1196 \text{ м}^2 \cdot 0.04 \text{ м}$; 2024-00375-01-0-КР лист 24
19	Сетка Ø5Вр1 100x100 ; м²	1196.0	3.08	3683.7	2024-00375-01-0-КР лист 24
Изм.	Кол.уч.	Лист	№ док.	Подпись	Дата

2024-00375-01-0-КР.ВОР

Лист

15

Замена бетонных оснований полов подвала с одновременным устройством гидроизоляции (окончание)(2024-00375-01-0-КР.ТЧ. л.11)

№	Наименование вида работ	Объем работ			Обоснование объема работ
		Кол-во	Масса ед. кг.	Масса всех. кг	
	Устройство лестницы при перепаде отметки пола				
20	Ø8A500с, l=п.м.	33.8	0.395	13.3	2024-00375-01-0-КР лист 24
21	Ø12A500с, l=п.м.	27.1	0.888	24.1	2024-00375-01-0-КР лист 24
22	Скоба, Ø8A500с, l=935, шт.	18	0.37	6.65	2024-00375-01-0-КР лист 24
23	Скоба, Ø8A500с, l=880, шт.	24	0.35	8.34	2024-00375-01-0-КР лист 24
24	Скоба, Ø8A500с, l=1120, шт.	4	0.44	1.77	2024-00375-01-0-КР лист 24
			Всего:	54.16	
25	Бетон кл. В25, W6; м³	0.5	-	-	V=0.366 м²* 1.4 м, где 0.366 – площадь сечения лестницы, 1.4 – ширина лестницы; 2024-00375-01-0-КР лист 24
26	Planter standard ; м²	1.2	-	-	S=1.3 м*0.9 м, где 1.3 – длина Planter standard под лестницей, 0.9 – ширина Planter standard под лестницей; 2024-00375-01-0-КР лист 24
27	Песок (K _{упл} =0.95) ; м³	0.3	-	-	V=0.3 м²* 0.9 м, где 0.3 – площадь сечения засыпки, 0.9 – ширина засыпки; 2024-00375-01-0-КР лист 24
28	Кладка из полнотелого красного кирпича М150 на растворе М150 ; м³	0.2	-	-	V=0.3 м²* 0.25 м*2 шт., где 0.3-площадь стены, 0.25-толщина стены, 2-количество стен; 2024-00375-01-0-КР лист 24

Устройство вертикальной обмазочной гидроизоляции наружных стен подвала (2024-00375-01-0-КР.ТЧ. л.11)

№	Наименование вида работ	Объем работ			Обоснование объема работ
		Кол-во	Масса ед. кг.	Масса всех. кг	
1	Гидроизоляция цементная Пенетрон (или аналог), м²	620,4	-	-	S=162м*2.525м+74.3м*2.845м, где: 162 – длина наружных стен подвала в осях 1-19/А-М; 2.525 – высота наружных стен подвала в осях 1-19/А-М; 74.3 – длина наружных стен подвала в осях 19-21/А-М; 2.845 – высота наружных стен подвала в осях 19-21/А-М. 2024-00375-01-0-КР лист 24, Приложение

Замена входной группы со ступенями и пандусом в осях «А-В/8-13» вход №1 (начало) (2024-00375-01-0-КР.ТЧ. л.12)

№	Наименование вида работ	Объем работ			Обоснование объема работ
		Кол-во	Масса ед. кг.	Масса всех. кг	
	<u>Устройство плиты на отм. -0.080 с лестницей</u>				
1	Ø8A500с, l=п.м.	127.7	0.395	50.4	2024-00375-01-0-КР листы 27-30
2	Ø12A500с, l=п.м.	1047.9	0.888	930.5	2024-00375-01-0-КР листы 27-30
3	Скоба, Ø8A500с, l=705, шт.	79	0.28	22.00	2024-00375-01-0-КР листы 27-30
4	Скоба, Ø12A500с, l=1180, шт.	78	1.05	81.54	2024-00375-01-0-КР листы 27-30
5	Скоба, Ø8A500с, l=910, шт.	620	0.36	222.86	2024-00375-01-0-КР листы 27-30
			Итого:	1307.4	
6	Пенополистирол δ=50-100мм, м³	1.6	-	-	2024-00375-01-0-КР листы 27-30
7	Засыпка песком с послойным трамбованием до Купл.=0.95; м³	48.4	-	-	2024-00375-01-0-КР листы 27-30
8	Planter Standard (или аналог), м²	49.8	-	-	2024-00375-01-0-КР листы 27-30
9	Бетон кл. В25, не менее F200, не менее W4, м³	14.0	-	-	2024-00375-01-0-КР листы 27-30
	<u>Устройство плиты пандуса h=150мм</u>				
10	Ø8A500с, l=п.м.	436.7	0.395	172.5	2024-00375-01-0-КР листы 27-30
11	Ø12A500с, l=п.м.	445.2	0.888	395.3	2024-00375-01-0-КР листы 27-30
12	Скоба, Ø8A500с, l=660, шт.	318	0.26	82.90	2024-00375-01-0-КР листы 27-30
			Итого:	650.74	
13	Засыпка песком с послойным трамбованием до Купл.=0.95; м³	44.5	-	-	2024-00375-01-0-КР листы 27-30
14	Planter Standard (или аналог), м²	42.4	-	-	2024-00375-01-0-КР листы 27-30
15	Бетон кл. В25, не менее F200, не менее W4, м³	6.4	-	-	2024-00375-01-0-КР листы 27-30
	<u>Устройство колонн (4 шт.)</u>				
16	Ø16A500с, l=4125, шт.	18	6.51	117.2	2024-00375-01-0-КР листы 27-30
17	Ø16A500с, l=3715, шт.	6	5.86	35.2	2024-00375-01-0-КР листы 27-30
18	Хомут, Ø8A240, l=1450, шт	90	0.57	51.55	2024-00375-01-0-КР листы 27-30
19	Скоба, Ø12A500с, l=1170, шт.	12	1.04	12.47	2024-00375-01-0-КР листы 27-30
20	Скоба, Ø12A500с, l=1790, шт.	16	1.59	25.43	2024-00375-01-0-КР листы 27-30
			Итого:	241.8	
21	Бетон кл. В25, не менее F200, не менее W4, м³	2.1	-	-	2024-00375-01-0-КР листы 27-30

Замена входной группы со ступенями и пандусом в осях «А-В/8-13» вход №1 (окончание) (2024-00375-01-0-КР.ТЧ. л.12)

№	Наименование вида работ	Объем работ			Обоснование объема работ
		Кол-во	Масса ед. кз.	Масса всех кз.	
	<u>Устройство козырька с парапетом</u>				
22	Ø8A500с, l=п.м.	195.3	0.395	77.1	2024-00375-01-0-КР листы 27-30
23	Ø12A500с, l=п.м.	1271.8	0.888	1129.3	2024-00375-01-0-КР листы 27-30
24	Ø16A500с, l=2925,шт.	52	4.62	240.0	2024-00375-01-0-КР листы 27-30
25	Ø16A500с, l=5850,шт.	2	9.23	18.5	2024-00375-01-0-КР листы 27-30
26	Скоба, Ø8A500с, l=720,шт.	16	0.28	4.55	2024-00375-01-0-КР листы 27-30
27	Скоба, Ø8A500с, l=695,шт.	158	0.27	43.37	2024-00375-01-0-КР листы 27-30
28	Скоба, Ø8A500с, l=705,шт.	158	0.28	44.00	2024-00375-01-0-КР листы 27-30
29	Скоба, Ø12A500с, l=1180,шт.	80	1.05	83.83	2024-00375-01-0-КР листы 27-30
30	Скоба, Ø12A500с, l=1810,шт.	158	1.61	253.95	2024-00375-01-0-КР листы 27-30
31	Шпилька, Ø6A240, l=280,шт	79	0.06	4.91	2024-00375-01-0-КР листы 27-30
			Итого:	1899.6	
32	Бетон кл. В25, не менее F200, не менее W4, м³	15.8			2024-00375-01-0-КР листы 27-30

Установка металлического ограждения по периметру кровли (2024-00375-01-0-КР.ТЧ. л.12)

№	Наименование вида работ	Объем работ			Обоснование объема работ
		Кол-во	Масса ед. кз.	Масса всех кз.	
1	Металлическое ограждение, п.м	172.1	20.52	3531.5	2024-00375-01-0-КР лист 23, 38
2	Шпилька М8 на клевоом анкере HIT-HY 270 (или аналог), шт.	688	-	-	N=172 шт.*4, где 172-количество стоек ограждения с шагом 1000 мм, 4-количество шпилек на стойку; 2024-00375-01-0-КР лист 23, 38
	<u>Расход материалов на 1 п.м</u>				
	Труба □ 40х50х5 поручень, п.м	2.0	5.77	11.54	2024-00375-01-0-КР лист 23
	Труба □ 40х50х5 стойка с кронштейном, п.м	1.4	5.77	8.08	2024-00375-01-0-КР лист 23
	-5х150, l=150, шт.	1	0.9	0.9	2024-00375-01-0-КР лист 23
	<u>Итого:</u>			20.52	

						2024-00375-01-0-КР.ВОР	Лист
Изм.	Кол.уч.	Лист	№ док.	Подпись	Дата		18

Замена конструкций входа в осях «А-Г/18-19» вход №2 (начало)
(2024-00375-01-0-КР.ТЧ. л.13)

№	Наименование вида работ	Объем работ			Обоснование объема работ
		Кол-во	Масса ед. кг.	Масса всех кг	
	<u>Устройство плиты на отм. -0.980 с лестницей</u>				
1	Ø8A500с, l=п.м.	7.1	0.395	2.8	2024-00375-01-0-КР листы 31, 32
2	Ø12A500с, l=п.м.	562.8	0.888	499.8	2024-00375-01-0-КР листы 31, 32
3	Скоба, Ø8A500с, l=705, шт.	127	0.28	35.37	2024-00375-01-0-КР листы 31, 32
4	Скоба, Ø12A500с, l=1180, шт.	39	1.05	41.26	2024-00375-01-0-КР листы 31, 32
5	Скоба, Ø8A500с, l=910, шт.	36	0.36	12.94	2024-00375-01-0-КР листы 31, 32
			Итого:	592.1	
6	Пенополистирол δ=50-100мм, м³	2.0	-	-	2024-00375-01-0-КР листы 31, 32
7	Засыпка песком с послойным трамбованием до Купл.=0.95; м³	17.3	-	-	2024-00375-01-0-КР листы 31, 32
8	Planter Standard (или аналог), м²	26.7	-	-	2024-00375-01-0-КР листы 31, 32
9	Бетон кл. В25, не менее F200, не менее W4, м³	5.5	-	-	2024-00375-01-0-КР листы 31, 32
	<u>Устройство козырька с парапетом</u>				
11	Ø8A500с, l=п.м.	436.7	0.395	172.5	2024-00375-01-0-КР листы 31, 32
12	Ø12A500с, l=п.м.	445.2	0.888	395.3	2024-00375-01-0-КР листы 31, 32
13	Ø16A500с, l=11700, шт.	6	18.46	110.8	2024-00375-01-0-КР листы 31, 32
14	Скоба, Ø8A500с, l=705, шт.	127	0.28	35.37	2024-00375-01-0-КР листы 31, 32
15	Скоба, Ø12A500с, l=1180, шт.	39	1.05	41.26	2024-00375-01-0-КР листы 31, 32
16	Скоба, Ø8A500с, l=910, шт.	36	0.36	12.94	2024-00375-01-0-КР листы 31, 32
			Итого:	768.2	
17	Бетон кл. В25, не менее F200, не менее W4, м³	10.0	-	-	$V = 30.6\text{м}^2 \cdot 0.2\text{м} + 5.6\text{м}^2 \cdot 0.7\text{м}$, где 30.6-площадь плиты, 0.2-толщина плиты, 5.6-площадь парапета козырька, 0.7-высота парапета козырька. 2024-00375-01-0-КР листы 31, 32
	<u>Монтаж стоек С1</u>				
18	.п160x160x6, l=3855, шт	6	109.06	654.3	2024-00375-01-0-КР листы 31, 32
19	-12x250, l=250, шт.	12	5.89	70.7	2024-00375-01-0-КР листы 31, 32
20	Закладная деталь ЗД-1, шт	6	8.35	50.1	2024-00375-01-0-КР листы 31, 32
			Итого:	775.1	

Замена конструкций входа в осях «А-Г/18-19» (окончание)
(2024-00375-01-0-КР.ТЧ. л.13)

№	Наименование вида работ	Объем работ			Обоснование объема работ
		Кол-во	Масса ед. кг.	Масса всех. кг	
	<u>Монтаж деталей ЗД1</u>				
21	-14x250, l=250,шт.	6	6.87	41.21	2024-00375-01-0-КР листы 31, 32
22	∅16А500с, l=470,шт.	12	0.74	8.90	2024-00375-01-0-КР листы 31, 32
			Итого:	50.11	
	<u>Монтаж деталей ЗД2</u>				
23	-14x250, l=250,шт.	6	6.87	41.21	2024-00375-01-0-КР листы 31, 32
24	∅16А500с, l=815,шт.	24	1.29	30.87	2024-00375-01-0-КР листы 31, 32
			Итого:	72.08	

Замена перегородок с устройством фахверка и стальных каркасов
(2024-00375-01-0-КР.ТЧ. л.13)

№	Наименование вида работ	Объем работ			Обоснование объема работ
		Кол-во	Масса ед. кг.	Масса всех. кг	
	<u>Рамы</u>				
1	Рама в перегородке, шт.	49	115.05	5637.45	Листы 34-37, проемы в перегородках EI толщиной 120 мм(165 мм с учетом штукатурки)
2	Анкер М12 для пустотной плиты, шт.	-	-	294	N=6шт.*49; 2024-00375-01-0-КР лист 33
	<u>Устройство рамы в перегородке</u>				
3	С14п, l=п.м.	8.9	12.3	109.47	2024-00375-01-0-КР лист 33
4	L100x8, l=120, шт.	2	1.47	2.94	2024-00375-01-0-КР лист 33
5	-4x120, l=п.м.	0.7	3.77	2.64	2024-00375-01-0-КР лист 33
			Итого:	115.05	
6	Анкер М12 для пустотной плиты, шт.	6	-	-	2024-00375-01-0-КР лист 33

						2024-00375-01-0-КР.ВОР	Лист
							20
Изм.	Кол.уч.	Лист	N док.	Подпись	Дата		

Крепление оборудования в спортивном зале (2024-00375-01-0-КР.ТЧ. л.14)

№	Наименование вида работ	Объем работ			Обоснование объема работ
		Кол-во	Масса ед. кг.	Масса всех кг	
1	Стойка крепления	12	80.02	960.24	6 корзин в спортивном зале, 2 стойки на корзину. 2024-00375-01-0-КР лист 33
	<u>Расход материалов на 1 стойку крепления</u>				
2	Двутавр I12Б1, п.м	6,4	8,7	55.68	2024-00375-01-0-КР лист 33
3	L100x8, l=120, шт.	2	1.47	2.94	2024-00375-01-0-КР лист 33
4	-4x120x820, шт.	1	3.77	3.77	2024-00375-01-0-КР лист 33
5	-12x120, l=п.м.	156	11,30	17.63	2024-00375-01-0-КР лист 33
			Итого:	80.02	
6	Шпильки M16, l=750, шт.	7	-	-	2024-00375-01-0-КР лист 33
7	Гайки с шайбами M16, шт.	14	-	-	2024-00375-01-0-КР лист 33
8	Анкер M12 для пустотной плиты, шт.	2	-	-	2024-00375-01-0-КР лист 33
	<u>Расход материалов на крепление рамы корзины</u>				
	Труба □ 100x8, п.м	14.4	21.39	308.0	2024-00375-01-0-КР лист 33, Приложение
	L50x5, l=120, шт.	48	0.45	21.72	2024-00375-01-0-КР лист 33, Приложение

Ремонт кирпичных стен (2024-00375-01-0-КР.ТЧ. л.14) (начало)

№	Наименование вида работ	Объем работ			Обоснование объема работ
		Кол-во	Масса ед. кг.	Масса всех кг	
	<u>Ремонт кладки оштукатуриванием</u>				
1	φ8A500C (Лобщ.), п.м	17	0,395	6.7	Лобщ.=5м ² :0,3м, где: 5-площадь выветривания кирпичной кладки, подлежащая ремонту ТЗК дефект. ведомость, п.2; 0,3 - шаг анкеров из арматуры φ8A500C в шахматном порядке
2	Сетка φ3Bp1 50x50 ; м ²	5.0	2.00	10.0	ТЗК дефект. ведомость, п.2
3	Цементно-песчаный раствор марки M150 толщиной 30мм, м ³	0.15			V=5 м ² *0.03 м, где 5 - площадь выветривания кирпичной кладки, подлежащая ремонту ,ТЗК дефект. ведомость, п.2
	<u>Локальная замена кирпичной кладки</u>				
4	Кирпич керамический полнотелый красный, м ³	3,5			ТЗК дефект. ведомость, п.2

Ремонт кирпичных стен (2024-00375-01-0-КР.ТЧ. л.14) (окончание)

№	Наименование вида работ	Объем работ			Обоснование объема работ
		Кол-во	Масса ед. кг.	Масса всех. кг.	
	Ремонт трещин в кирпичной стене				
1	L120x8, l=п.м.	11.2	14.76	165.3	2024-00375-01-0-КР лист 20, ТЗК дефект. ведомость, п.2
2	-6x150, l=150, шт.	322	1.06	341.2	2024-00375-01-0-КР лист 20, ТЗК дефект. ведомость, п.2
			Итого:	506.6	
3	Шпильки M12, l=750*, шт.	161			2024-00375-01-0-КР лист 20, ТЗК дефект. ведомость, п.2
4	Гайки с шайбами M16, шт.	322			2024-00375-01-0-КР лист 20, ТЗК дефект. ведомость, п.2
5	Ø10A240, l=п.м.	515.2	0.617	317.9	2024-00375-01-0-КР лист 20, ТЗК дефект. ведомость, п.2
6	сжимы, Ø6A240, l=140, шт.	161	0.031	5.0	2024-00375-01-0-КР лист 20, ТЗК дефект. ведомость, п.2

Ремонт конструкций кровли здания в осях: «А-Г /18-19»
(2024-00375-01-0-КР.ТЧ. л.14)


№	Наименование вида работ	Объем работ			Обоснование объема работ
		Кол-во	Масса ед. кг.	Масса всех. кг.	
1	Стропила из бруса 80x180 l=п.м.	431.7	7.6	3294.87	$l = 378.7 \text{ п.м.} * 1.14$, где 378.7 – суммарная длина стропил в плане, 1.14 – учет наклона стропил, 2024-00375-01-0-КР лист 39
2	Доп. стойки из бруса 140x140 l=п.м.	72.0	10.4	747.94	$l = 3.6 \text{ п.м.} * 20 \text{ шт.}$, где 3.6 – длина одной стойки, 20 – количество стоек, 2024-00375-01-0-КР лист 39
			Итого:	4042.81	
3	Уголок крепежный 90x90x65x2 КУУ (крепление стропил).	316			2024-00375-01-0-КР лист 39
4	Шпильки M12 (крепление стропил), l=п.м.	15.8			2024-00375-01-0-КР лист 39
5	Гайки с шайбами M12, шт.	316			2024-00375-01-0-КР лист 39
6	Покрытие огне/биозащитным составом, м ²	1093.2			$S = 800.28 \text{ м}^2 + 175.56 \text{ м}^2 + 117.36 \text{ м}^2$, где 800.28 – площадь обмазки новых и существующих стропил 180x80 сечением, 175.56 – площадь обмазки новых и существующих стоек сечением 140x140, 117.36 – площадь обмазки существующего мауэрлата сечением 150x150 2024-00375-01-0-КР лист 39

						2024-00375-01-0-КР.ВОР	Лист
							22
Изм.	Кол.уч.	Лист	N док.	Подпись	Дата		


Приложения

						2024-00375-01-0-KP.BOP	Лист
							23
Изм.	Кол.уч.	Лист	N док.	Подпись	Дата		

Крепление рамы корзины

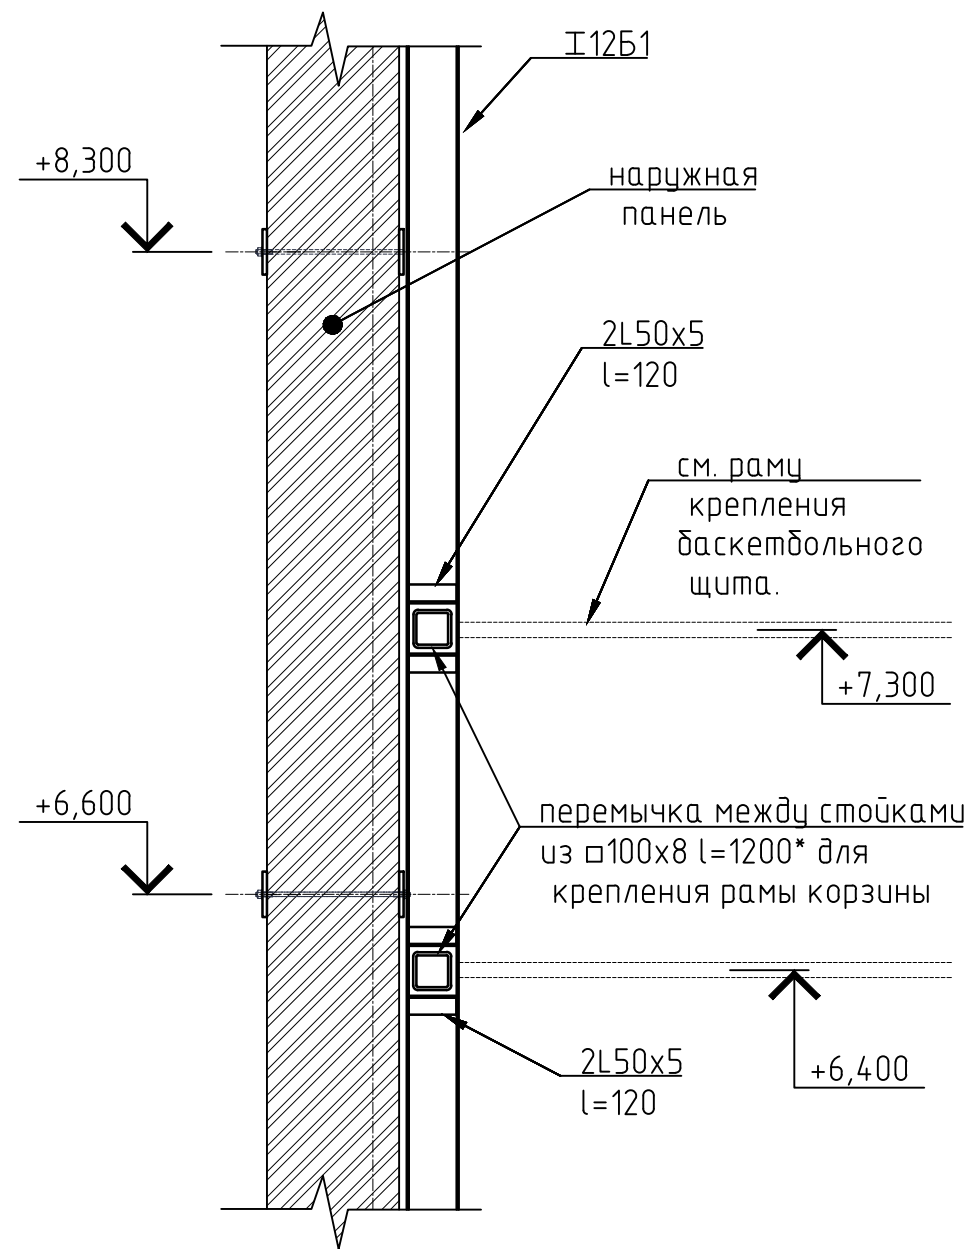

Устройство гидроизоляции наружных стен подвала

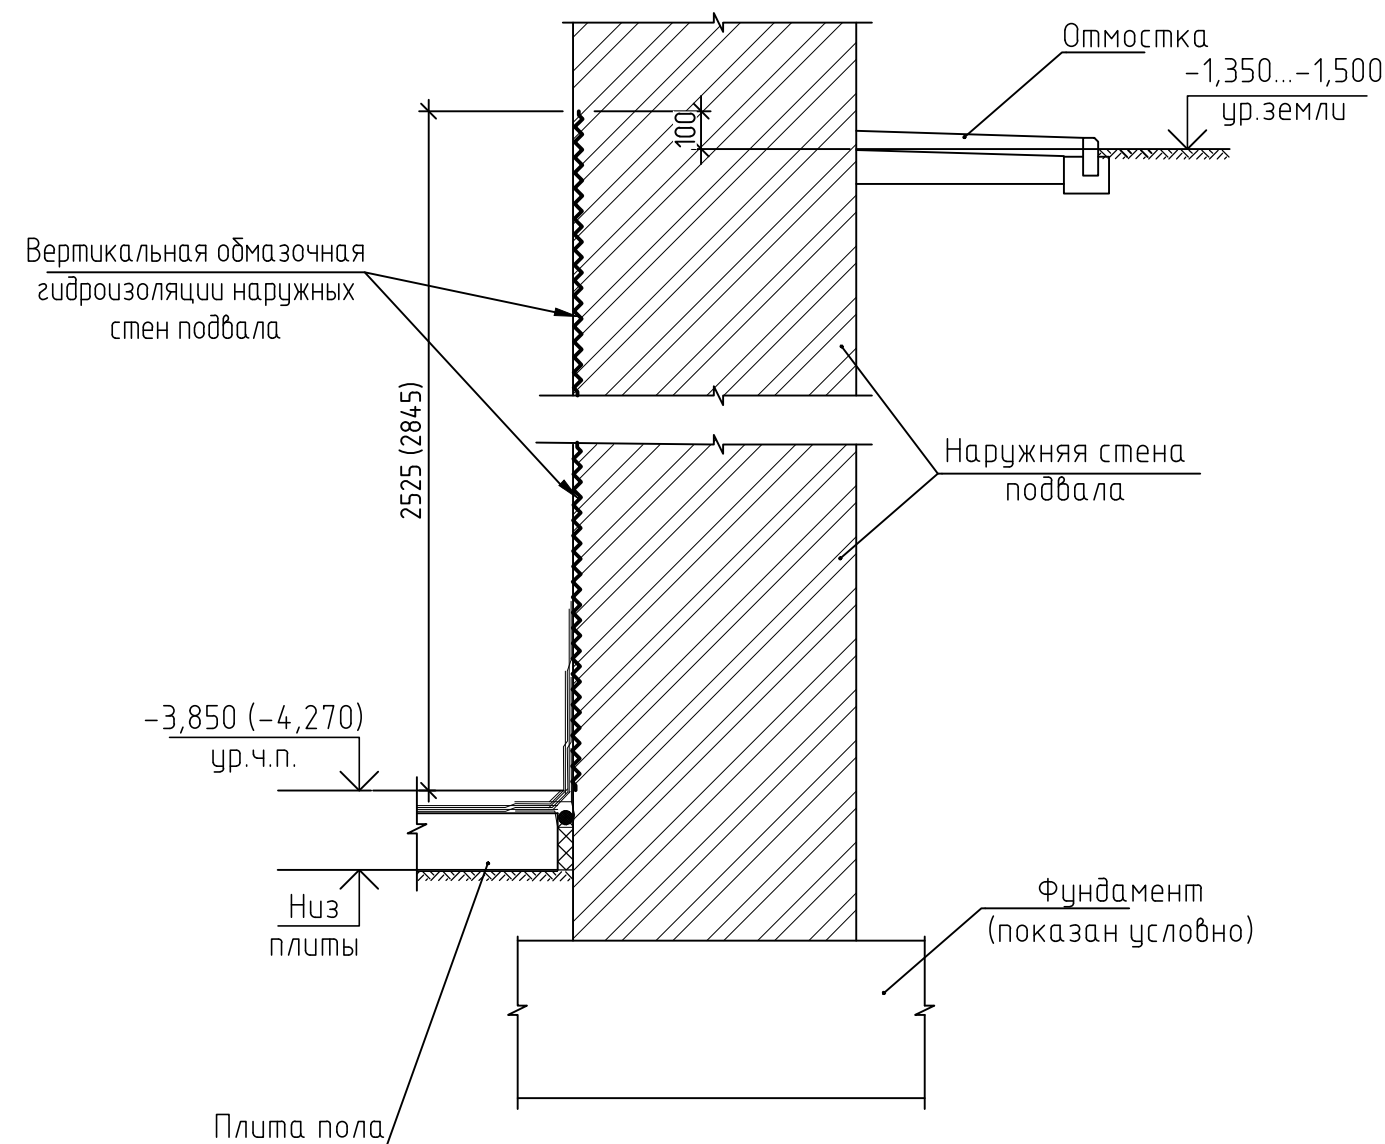

						2024-00375-01-0-КР.ВОР			
						Здания Государственного бюджетного общеобразовательного учреждения города Москвы "Школа № 1574", расположенного по адресу г. Москва, пер. Старопименовский, д. 5			
Изм.	Кол.уч.	Лист	№ док.	Подпись	Дата	Капитальный ремонт	Стадия	Лист	Листов
Разработал	Кулакова Е.Ю.							24	
Зав.сектором	Горшков Д.М.								
ГИП	Дашкевич К.С.					Крепление рамы корзины. Устройство гидроизоляции наружных стен подвала			
Н. контр.	Горшков Д.М.				10.25				



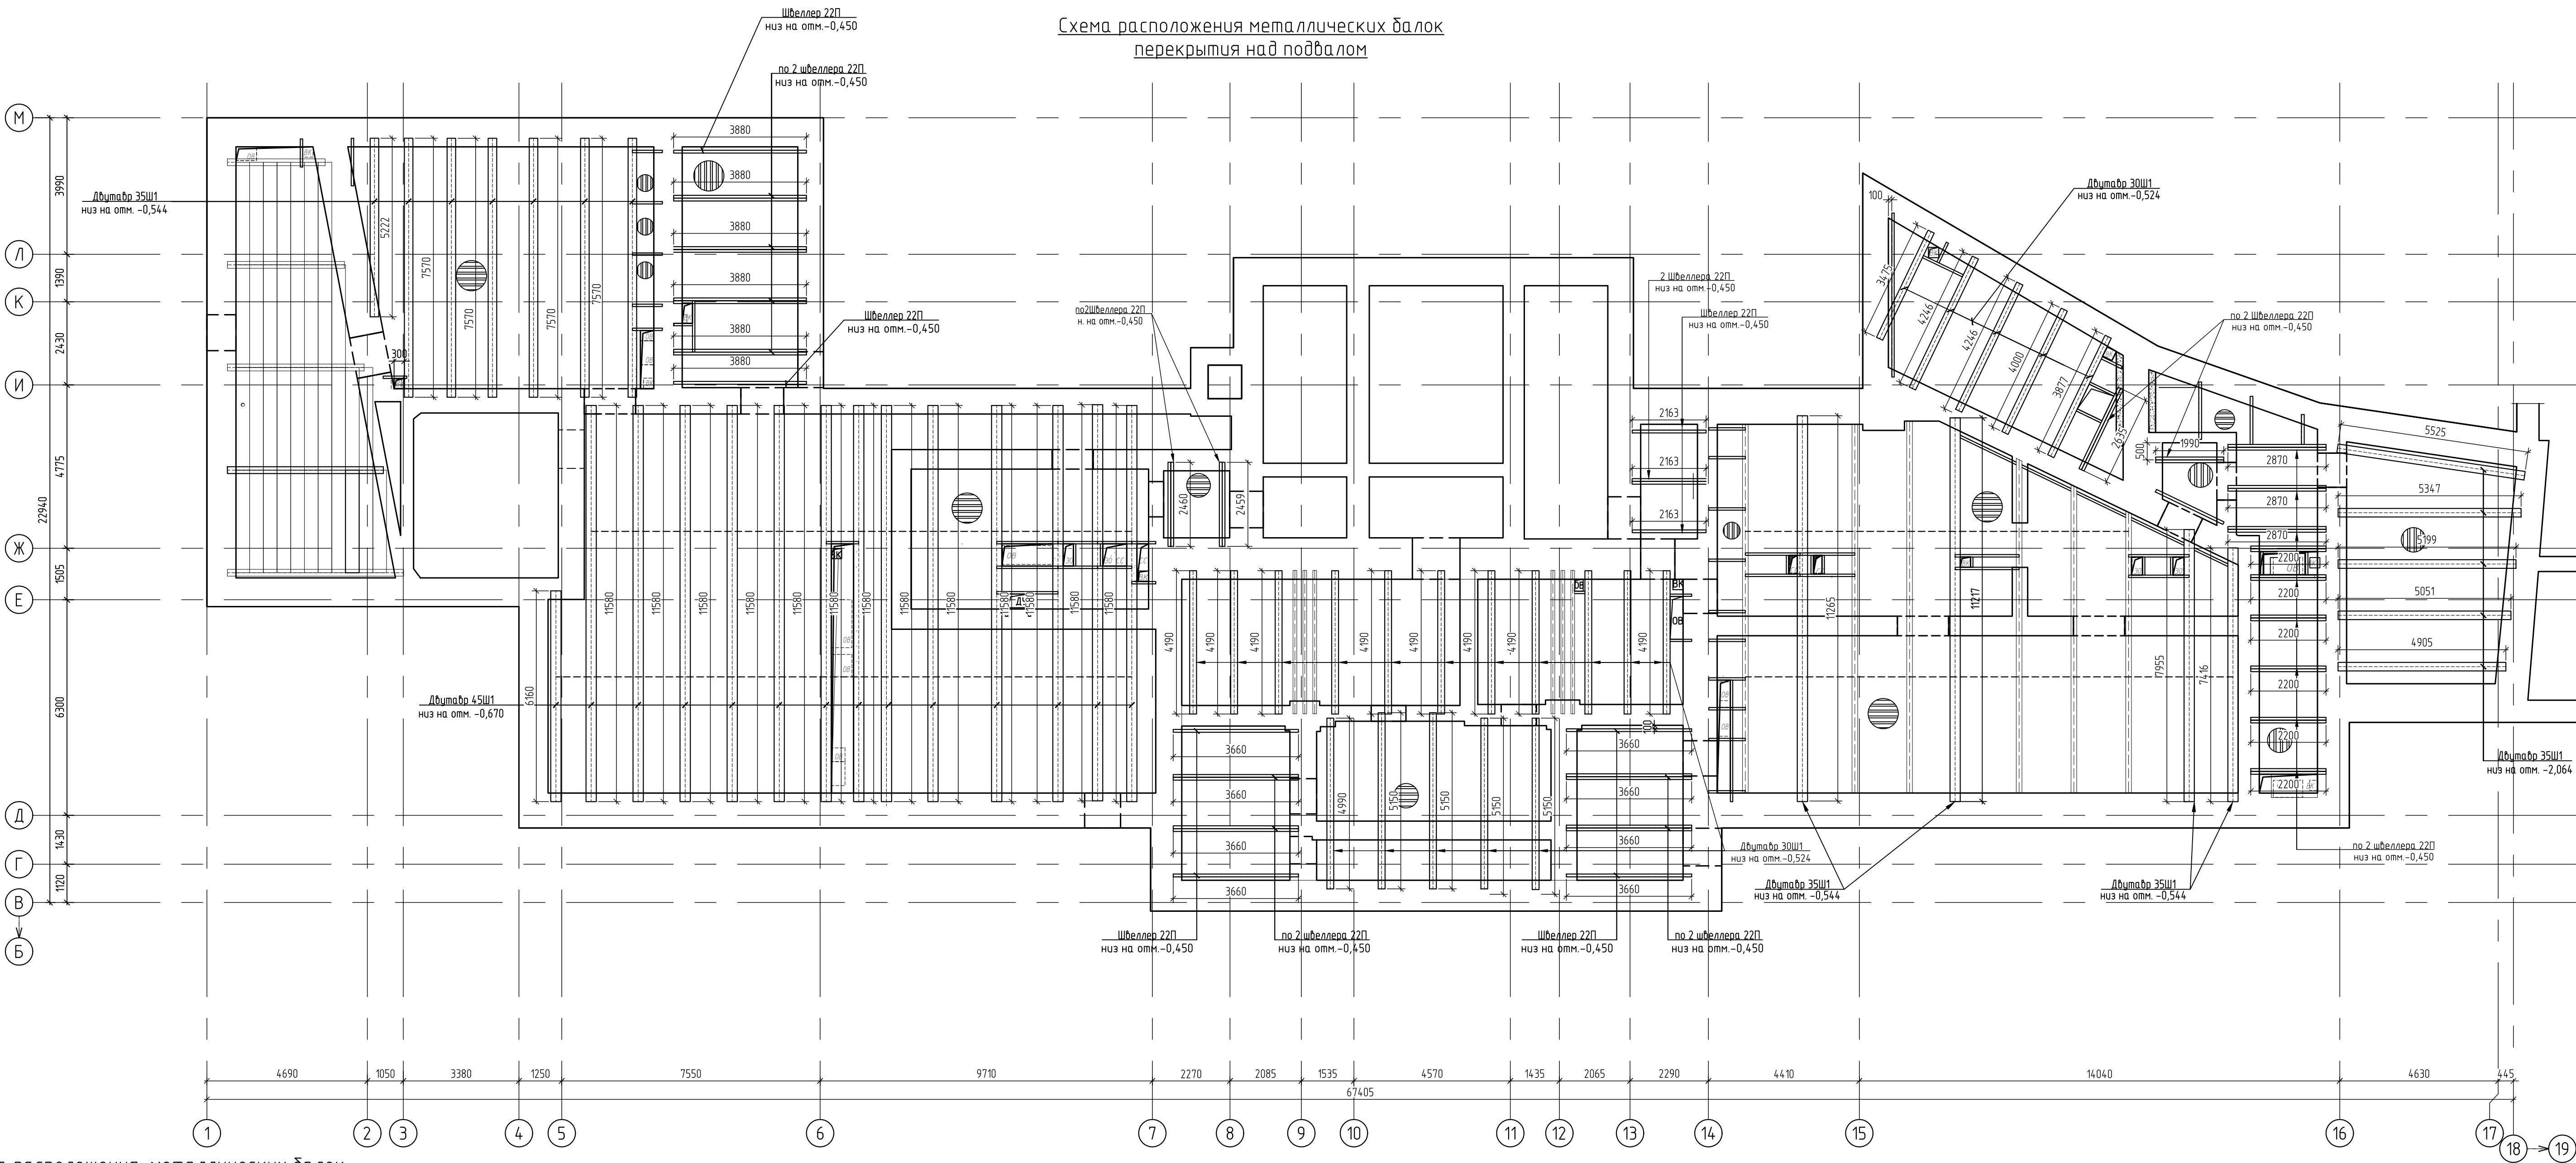


Схема расположения металлических балок перекрытия в осях 9-11 / Ж-Л на отм. -1,050


Схема расположения металлических балок перекрытия в осях 8-11 / Ж-К на отм. -3,850

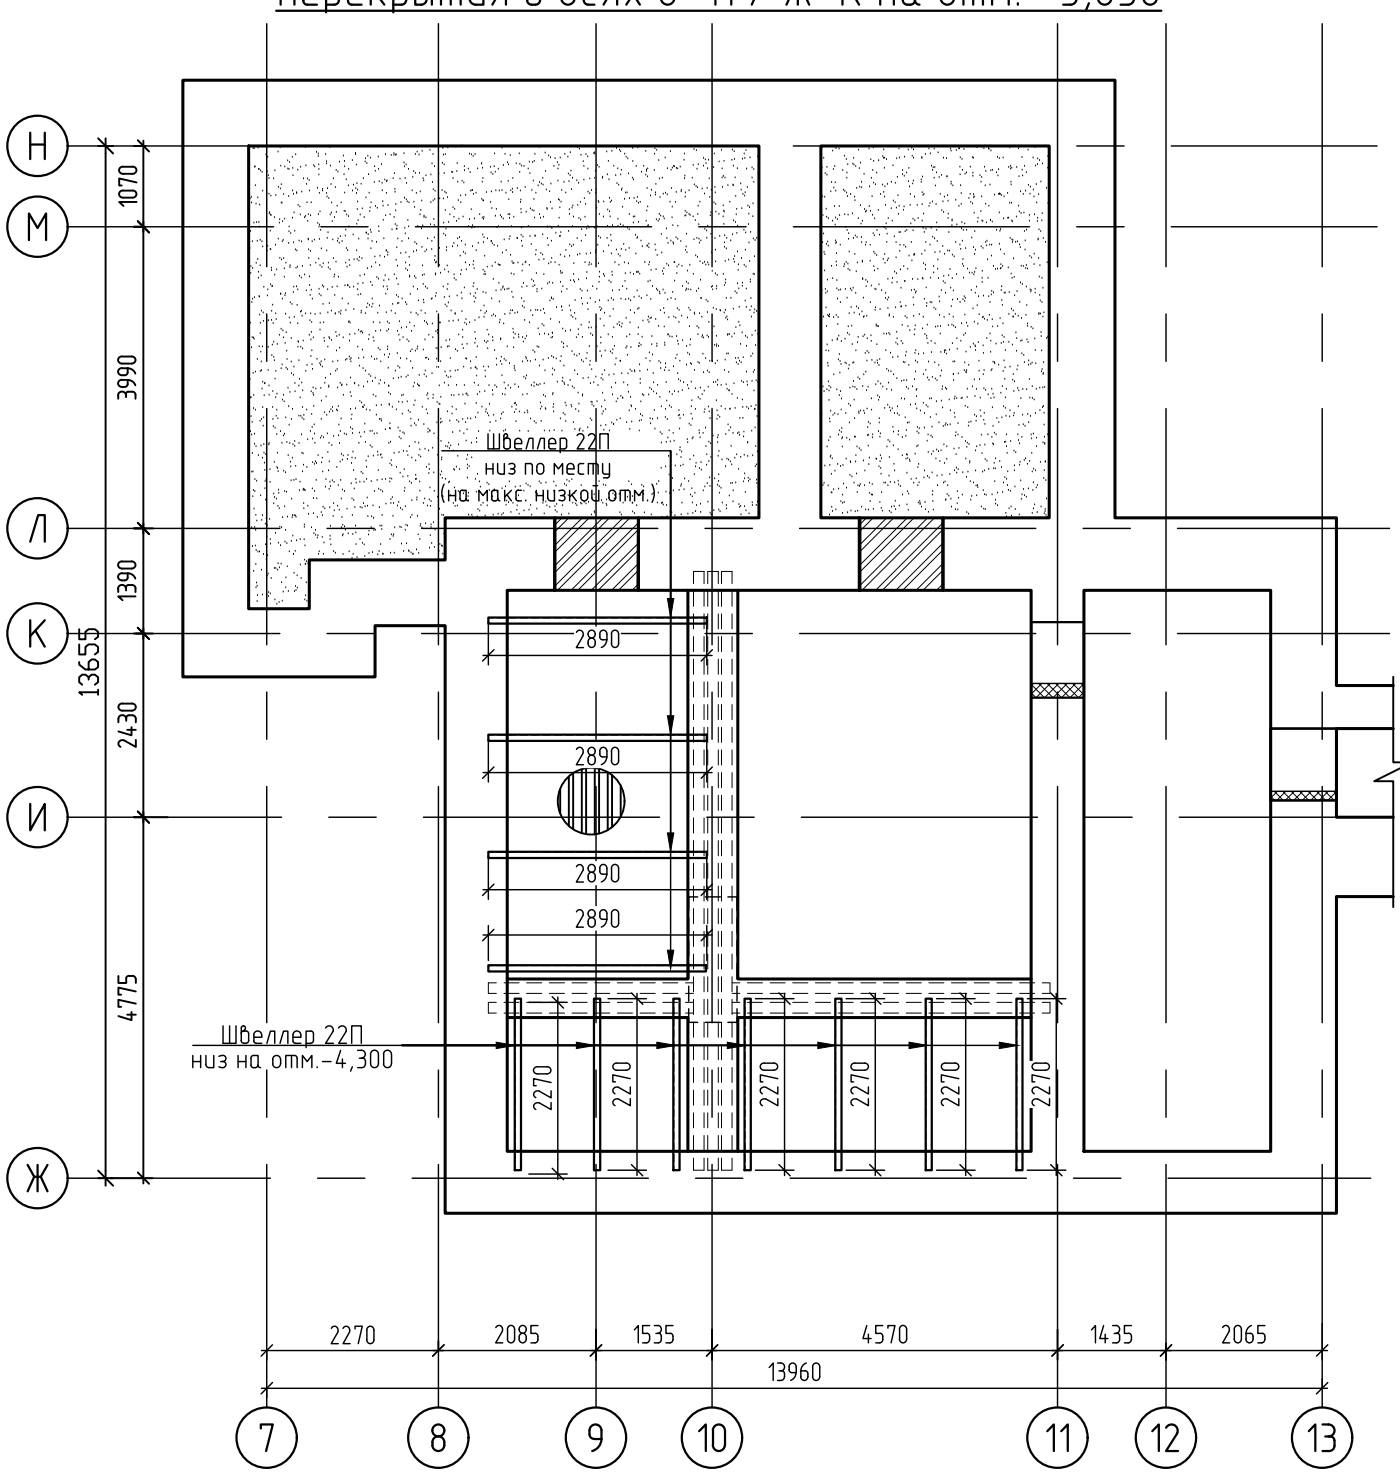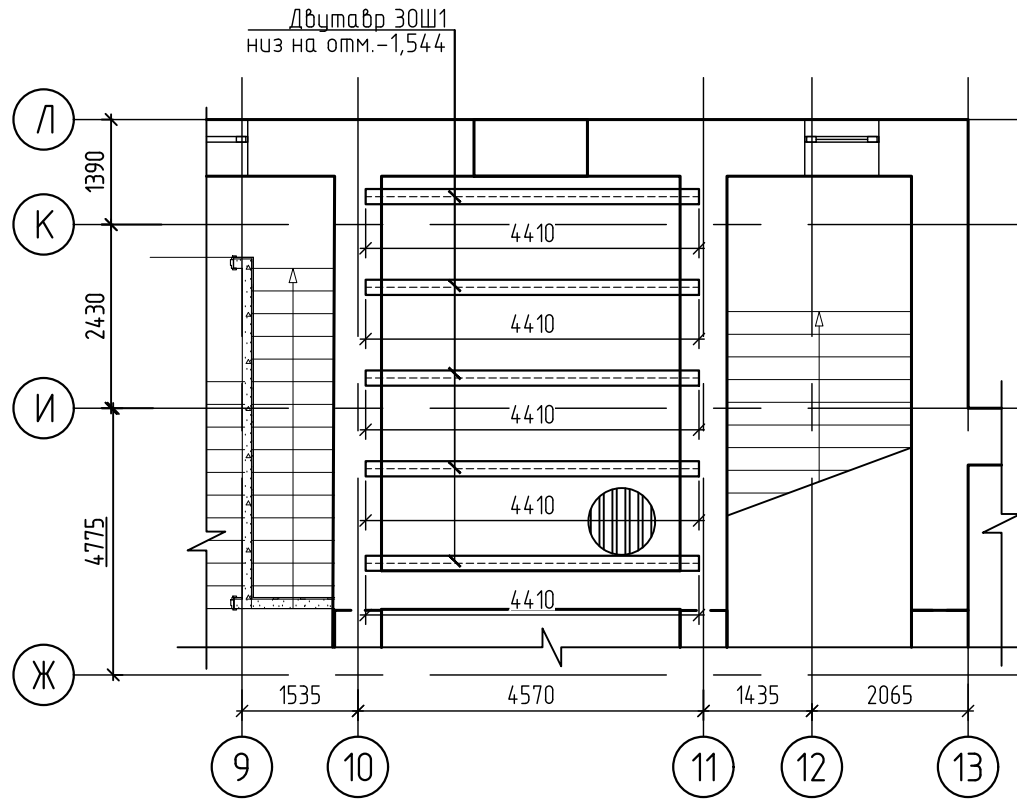

[illegible][illegible]

						2024-00375-01-0-КР.ВОР		
Изм.	Колуч	Лист	№ док.	Подпись	Дата	Здание Государственного бюджетного общеобразовательного учреждения города Москвы "Школа № 1574", расположенного по адресу: г. Москва, пер. Старопришибинский, д. 5		
Разработал			Кулакова Е.В.	<i>Кулакова Е.В.</i>		Капитальный ремонт	Страница	Лист
Зав.сектором			Горшкова Д.М.	<i>Горшкова Д.М.</i>			26	Листов
ГИП			Дашкевич К.С.	<i>Дашкевич К.С.</i>		Схема расположения металлических балок перекрытия над 1 этапом.	 МОСЖИЛ НИИПРОЕКТ	
Н. контр.			Горшкова Д.М.	<i>Горшкова Д.М.</i>	10-25			


Схема расположения металлических балок
перекрытия над 2 этажом

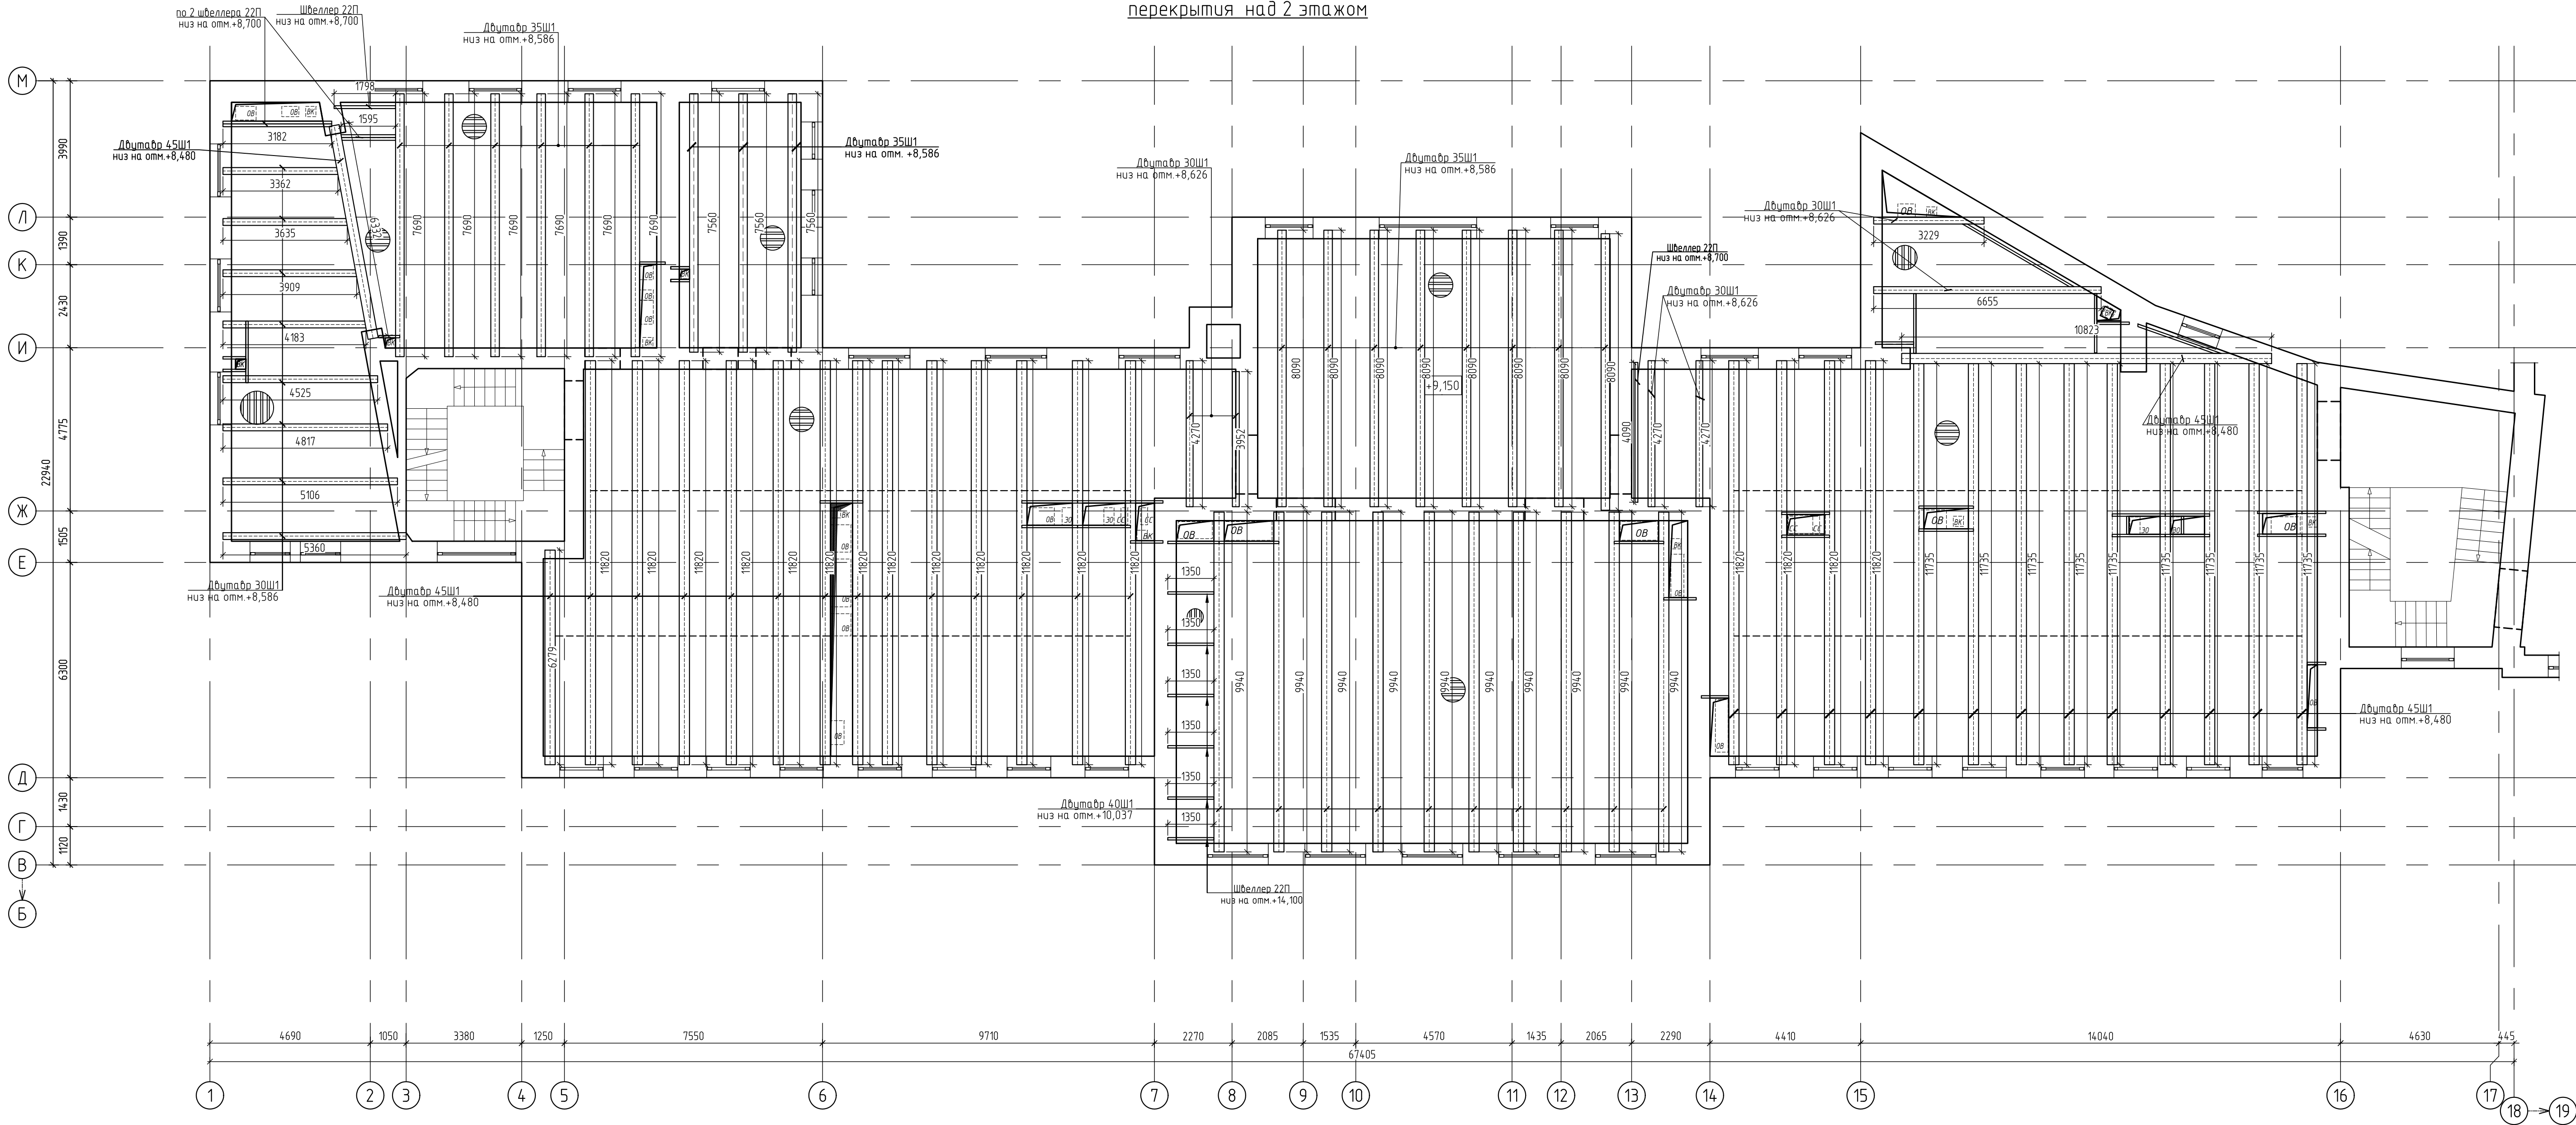

Согласовано	
Подпись и печать исполнителя	
Ид. № подл.	

2024-00375-01-0-КР.ВОР					
Здания Государственного бюджетного общеобразовательного учреждения города Москвы "Школа № 1574", расположенного по адресу: г. Москва, пер. Старопименовский, д. 5					
Капитальный ремонт			Стадия	Лист	Листов
ГИП			Дашкевич К.С.	27	
Н. контр.			Гаршков Д.М.	10.25	
Схема расположения металлических балок перекрытия над 2 этажом.			МОСЖИЛ НИИПРОЕКТ		
Копировал			Формат А1		


Схема расположения металлических балок
перекрытия над 3 этажом

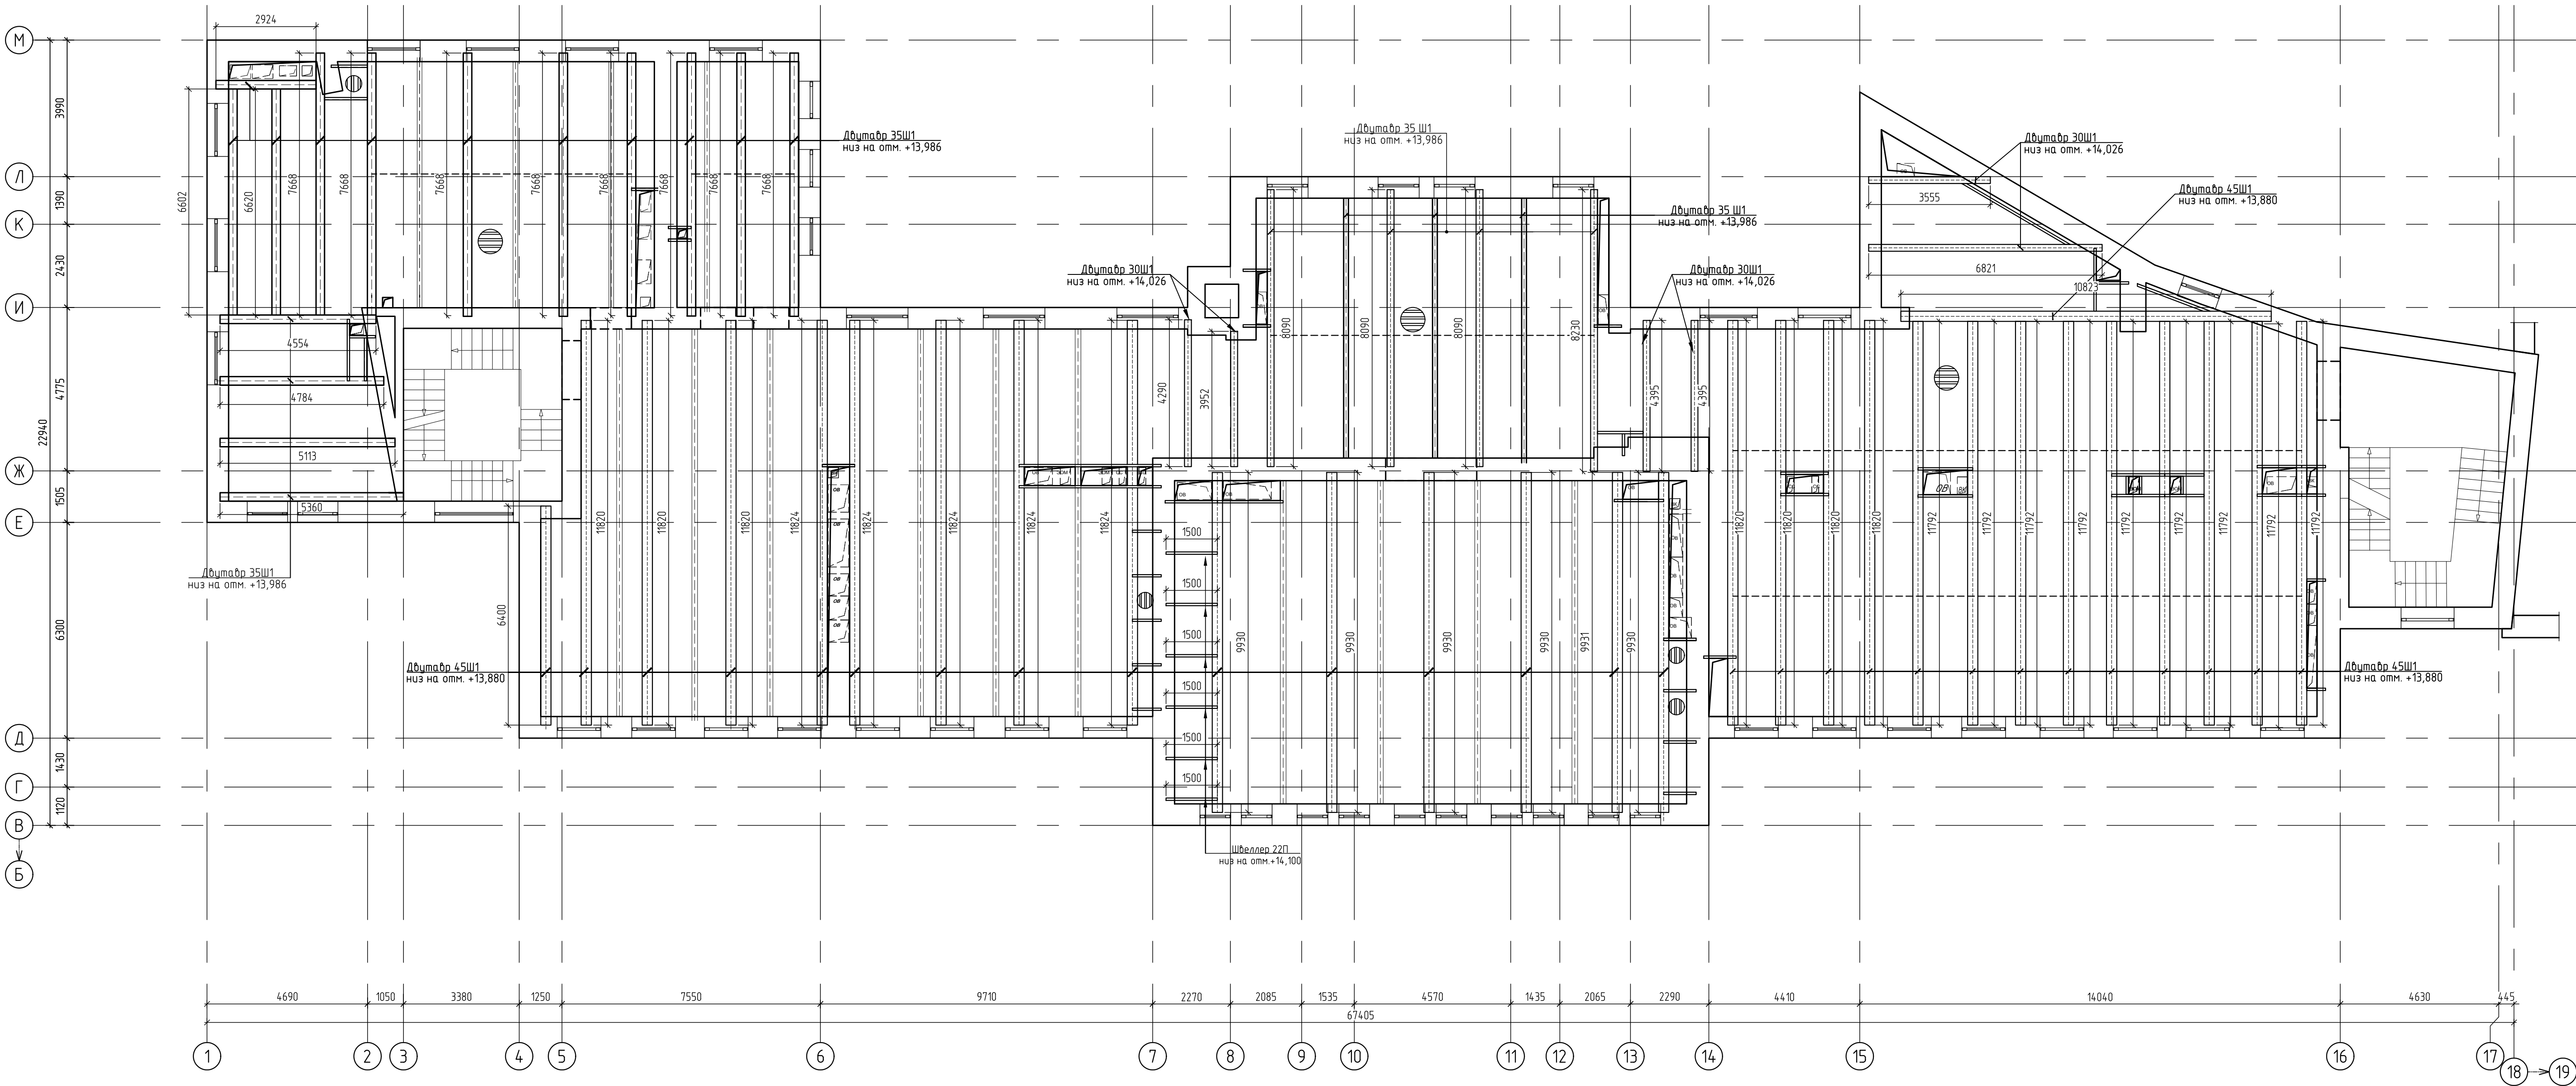

Согласовано	
Подпись Исполнителя	
Ид. № подл.	

2024-00375-01-0-КР.ВОР				
Здания Государственного бюджетного общеобразовательного учреждения города Москвы "Школа № 1574", расположенного по адресу г. Москва, пер. Старопименовский, д. 5				
Изм. Колуч.	Лист	№ док.	Подпись	Дата
Разработал	Кулакова Е.В.			
Заб.сектором	Горшков Д.М.			
ГИП	Дашкевич К.С.			
Н. контр.	Горшков Д.М.			10.25
Капитальный ремонт			Стадия	Лист
				28
Схема расположения металлических балок перекрытия над 3 этажом.			МОСЖИЛ НИИПРОЕКТ	
Копировал			Формат А1	


Схема расположения металлических балок
перекрытия над 4 этажом

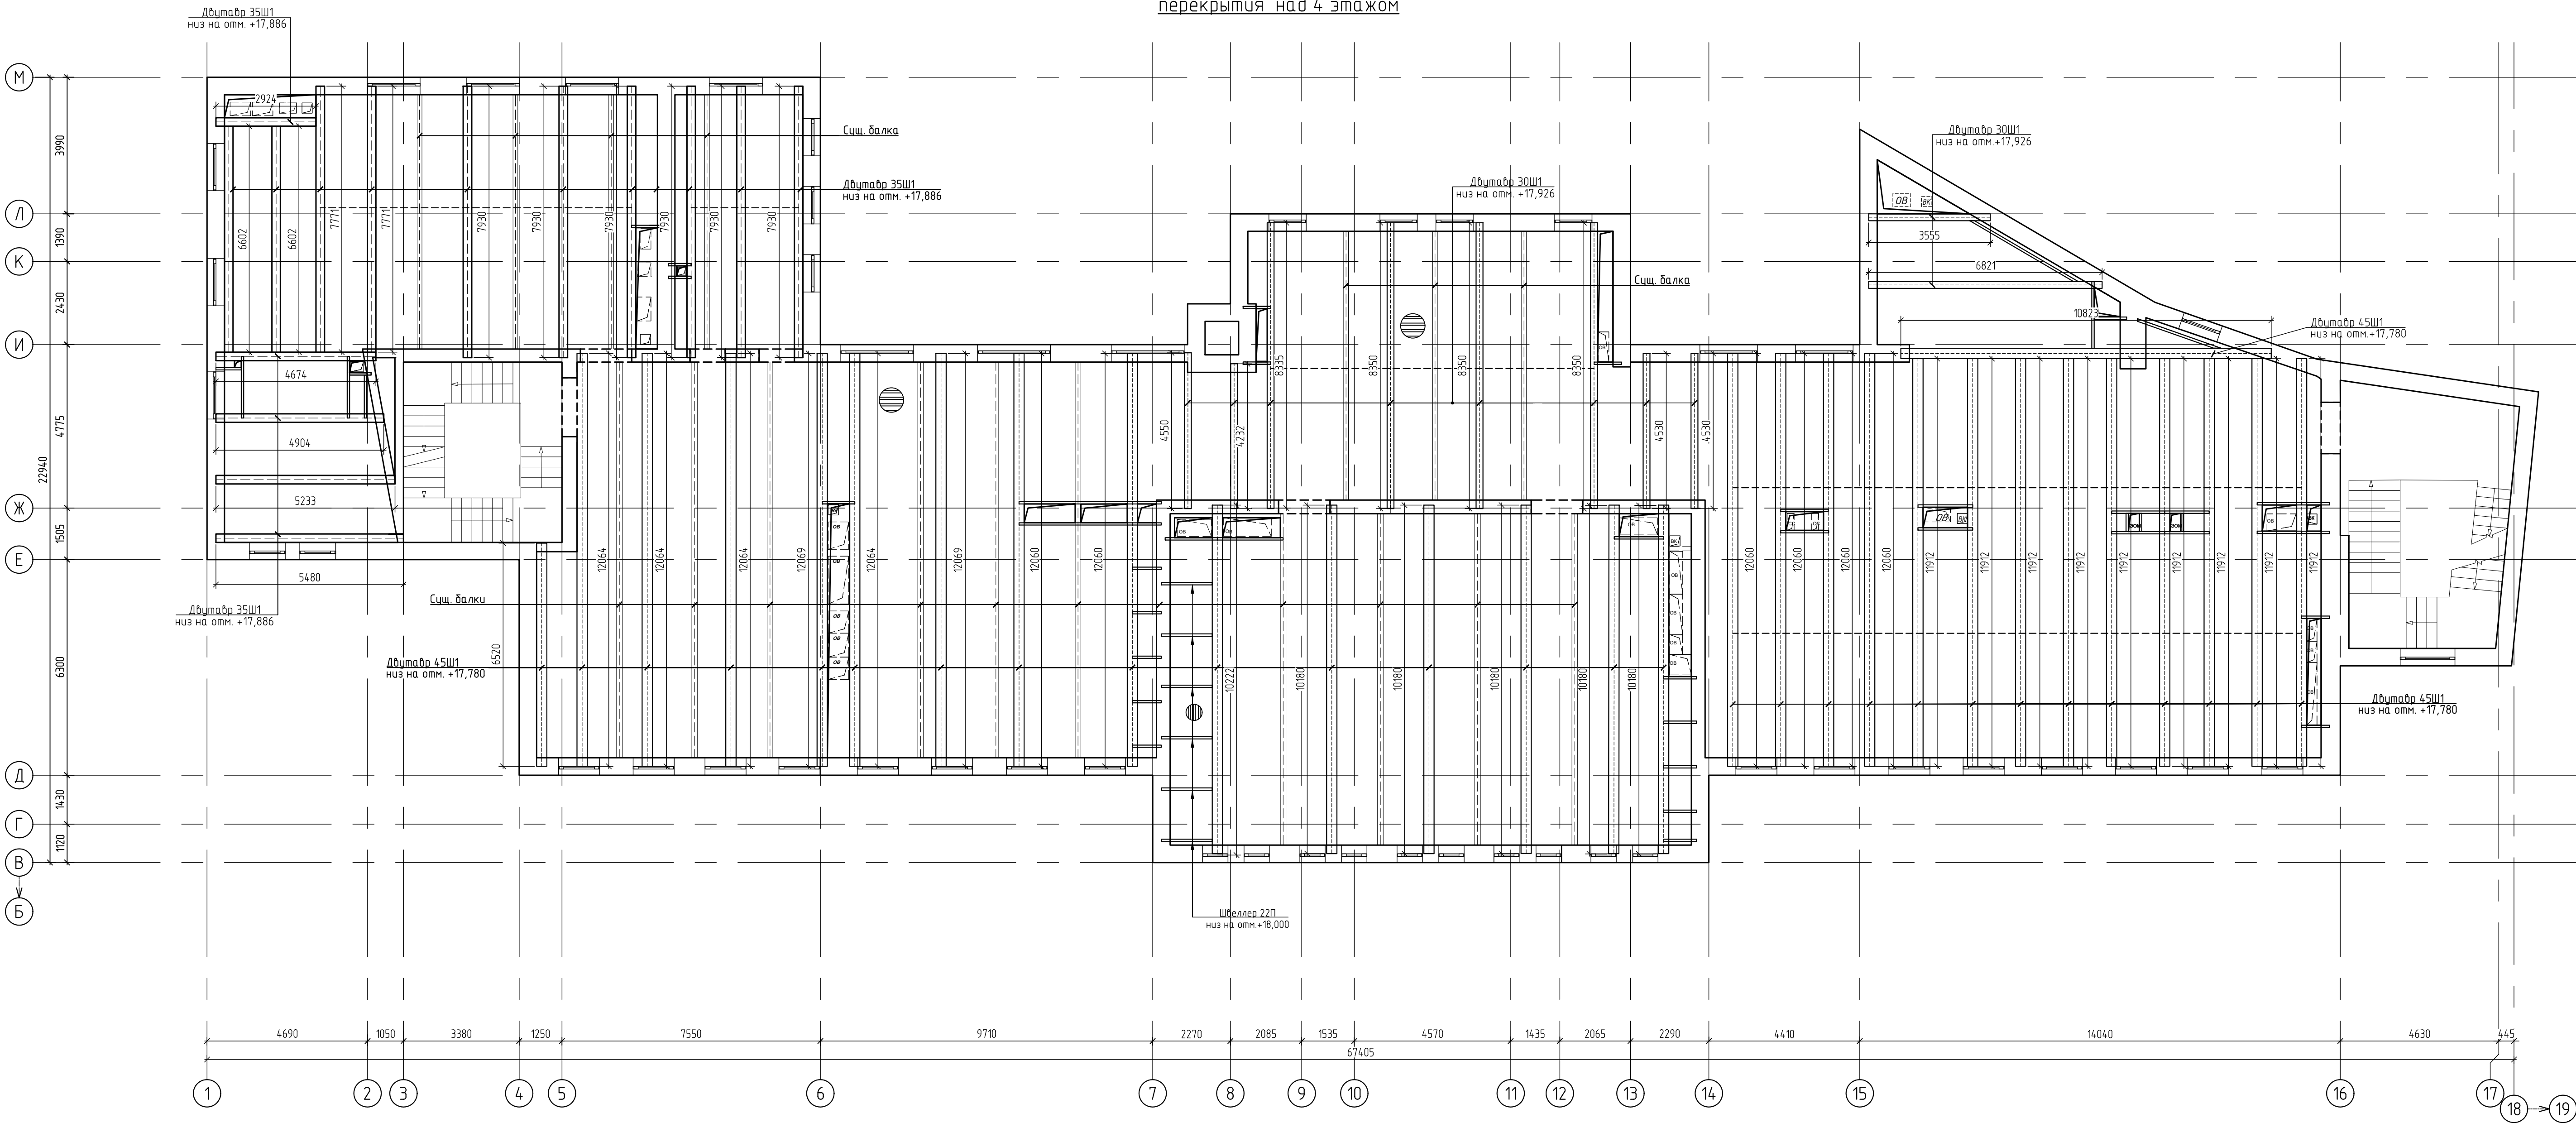

Согласовано	
Подпись и печать исполнителя	
Исх. № подл.	

2024-00375-01-0-КР.ВОР					
Здания Государственного бюджетного общеобразовательного учреждения города Москвы "Школа № 1574", расположенного по адресу г. Москва, пер. Старопименовский, д. 5					
Капитальный ремонт				Стадия	Лист
					29
Схема расположения металлических балок перекрытия над 4 этажом.					
Копировал					
Формат А1					

Схема расположения металлических балок
перекрытия над 5 этажом

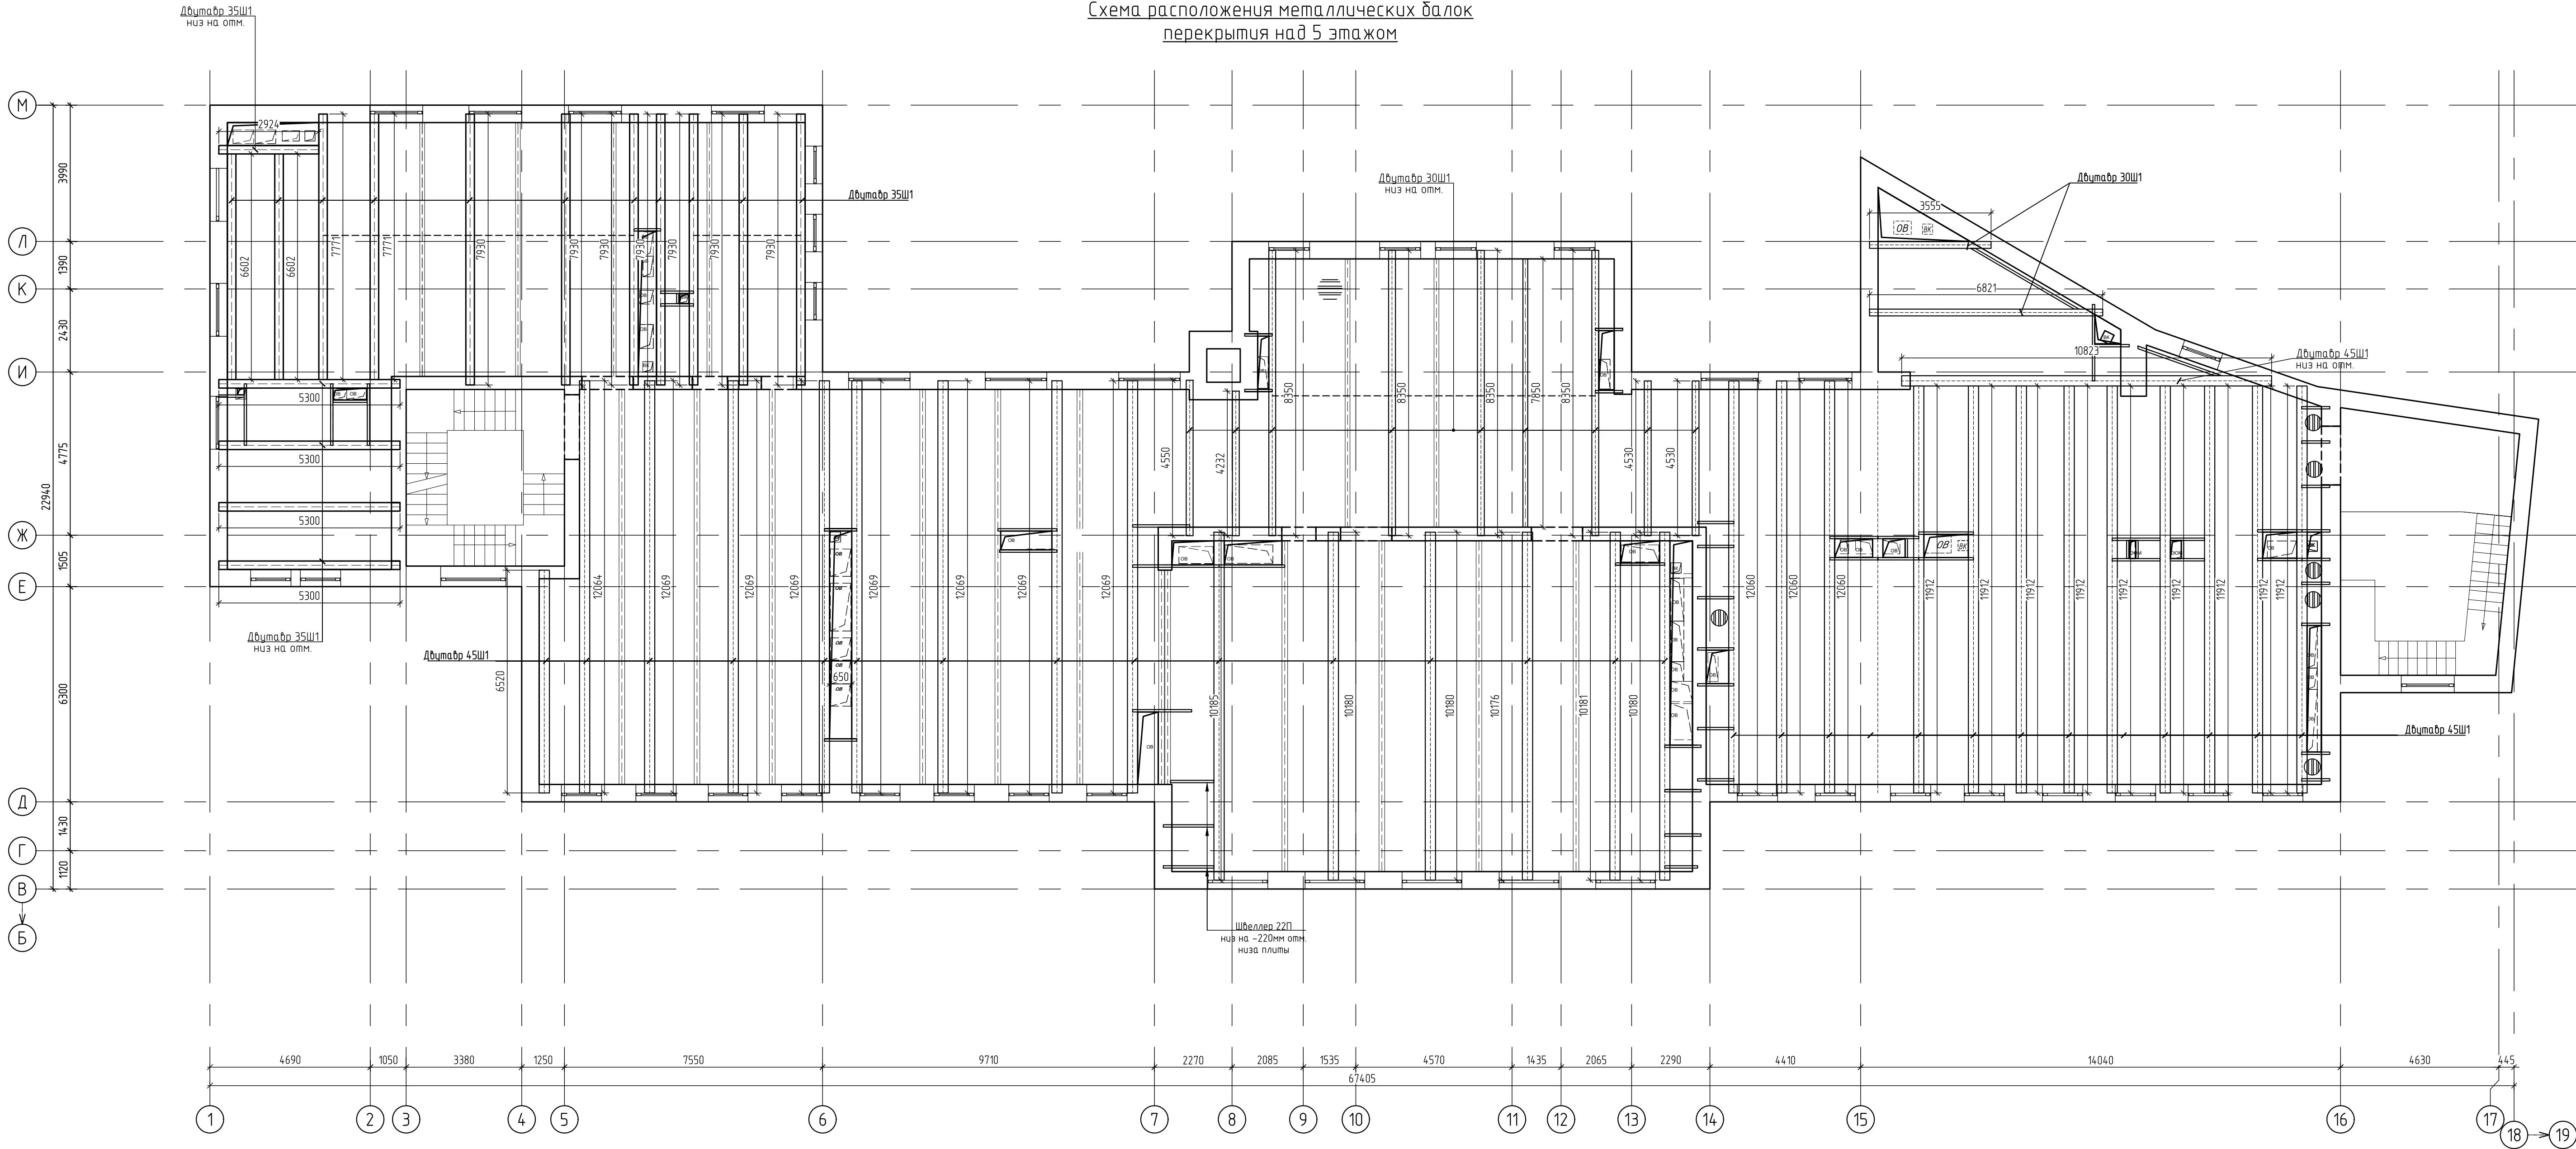

Согласовано	
Подпись и печать исполнителя	
Имя, № подл.	

2024-00375-01-0-КР.ВОР				
Здания Государственного бюджетного общеобразовательного учреждения города Москвы "Школа № 1574", расположенного по адресу: г. Москва, пер. Старопименовский, д. 5				
Изм. Колуч.	Лист № док.	Подпись	Дата	Капитальный ремонт
Разработал	Кулакова Е.В.	<i>Кулакова Е.В.</i>		Стадия
Заб. сектор	Гариков Д.М.	<i>Гариков Д.М.</i>		Лист
ГИП	Дашкевич К.С.	<i>Дашкевич К.С.</i>		Листов
Н. контр.	Гариков Д.М.	<i>Гариков Д.М.</i>	10.25	30
Схема расположения металлических балок перекрытия над 5 этажом.				МАСШТАБ 1:1
Копировал				Формат А1