



Департамент капитального ремонта города Москвы Государственное автономное учреждение города Москвы Московский научно-исследовательский и проектный институт жилищного хозяйства «МосжилНИИпроект» (ГАУ «МосжилНИИпроект»)

mgnp@mgnp.mos.ru +7 495 624 40 65 107078, г. Москва, ул. Каланчевская, д. 4/2, стр. 1

Арх. №

Капитальный ремонт здания Государственного бюджетного общеобразовательного учреждения города Москвы «Школа №1574», расположенного по адресу: г. Москва, пер. Старопименовский, д. 5

ПРОЕКТНАЯ ДОКУМЕНТАЦИЯ

Раздел 3. «Объемно-планировочные и архитектурные решения»

2024-00375-00-0-AP

Том 3

1 этап

2025

Капитальный ремонт здания Государственного бюджетного общеобразовательного учреждения города Москвы «Школа №1574», расположенного по адресу: г. Москва, пер. Старопименовский, д. 5

ПРОЕКТНАЯ ДОКУМЕНТАЦИЯ

Раздел 3. «Объемно-планировочные и архитектурные решения»

2024-00375-00-0-AP

Том 3

1 этап

Заместитель директора



11.12.24

Н.Р. Нигматулин

Главный инженер проекта

Н.М. Пильгуй

11.12.24

2025

[illegible]

А) ОПИСАНИЕ ВНЕШНЕГО ВИДА ОБЪЕКТА КАПИТАЛЬНОГО СТРОИТЕЛЬСТВА, ОПИСАНИЕ И ОБОСНОВАНИЕ ПРОСТРАНСТВЕННОЙ, ПЛАНИРОВОЧНОЙ И ФУНКЦИОНАЛЬНОЙ ОРГАНИЗАЦИИ ОБЪЕКТА КАПИТАЛЬНОГО СТРОИТЕЛЬСТВА	2
Б) ОБОСНОВАНИЕ ПРИНЯТЫХ ОБЪЕМНО-ПРОСТРАНСТВЕННЫХ И АРХИТЕКТУРНО-ХУДОЖЕСТВЕННЫХ РЕШЕНИЙ, В ТОМ ЧИСЛЕ В ЧАСТИ СОБЛЮДЕНИЯ ПРЕДЕЛЬНЫХ ПАРАМЕТРОВ РАЗРЕШЕННОГО СТРОИТЕЛЬСТВА, РЕКОНСТРУКЦИИ ОБЪЕКТА КАПИТАЛЬНОГО СТРОИТЕЛЬСТВА;	4
Б1) ОБОСНОВАНИЕ ПРИНЯТЫХ АРХИТЕКТУРНЫХ РЕШЕНИЙ В ЧАСТИ ОБЕСПЕЧЕНИЯ СООТВЕТСТВИЯ ЗДАНИЙ, СТРОЕНИЙ И СООРУЖЕНИЙ УСТАНОВЛЕННЫМ ТРЕБОВАНИЯМ ЭНЕРГЕТИЧЕСКОЙ ЭФФЕКТИВНОСТИ (ЗА ИСКЛЮЧЕНИЕМ ЗДАНИЙ, СТРОЕНИЙ, СООРУЖЕНИЙ, НА КОТОРЫЕ ТРЕБОВАНИЯ ЭНЕРГЕТИЧЕСКОЙ ЭФФЕКТИВНОСТИ НЕ РАСПРОСТРАНЯЮТСЯ).	13
Б2) ПЕРЕЧЕНЬ МЕРОПРИЯТИЙ ПО ОБЕСПЕЧЕНИЮ СОБЛЮДЕНИЯ УСТАНОВЛЕННЫХ ТРЕБОВАНИЙ ЭНЕРГЕТИЧЕСКОЙ ЭФФЕКТИВНОСТИ К АРХИТЕКТУРНЫМ РЕШЕНИЯМ, ВЛИЯЮЩИМ НА ЭНЕРГЕТИЧЕСКУЮ ЭФФЕКТИВНОСТЬ ЗДАНИЙ, СТРОЕНИЙ И СООРУЖЕНИЙ (ЗА ИСКЛЮЧЕНИЕМ ЗДАНИЙ, СТРОЕНИЙ, СООРУЖЕНИЙ, НА КОТОРЫЕ ТРЕБОВАНИЯ ЭНЕРГЕТИЧЕСКОЙ ЭФФЕКТИВНОСТИ НЕ РАСПРОСТРАНЯЮТСЯ).	13
Б3) ОПИСАНИЕ И ОБОСНОВАНИЕ ПРИНЯТЫХ АРХИТЕКТУРНЫХ РЕШЕНИЙ, НАПРАВЛЕННЫХ НА ПОВЫШЕНИЕ ЭНЕРГЕТИЧЕСКОЙ ЭФФЕКТИВНОСТИ ОБЪЕКТА КАПИТАЛЬНОГО СТРОИТЕЛЬСТВА.	14
В) ОПИСАНИЕ И ОБОСНОВАНИЕ ИСПОЛЬЗОВАННЫХ КОМПОЗИЦИОННЫХ ПРИЕМОВ ПРИ ОФОРМЛЕНИИ ФАСАДОВ И ИНТЕРЬЕРОВ ОБЪЕКТОВ КАПИТАЛЬНОГО СТРОИТЕЛЬСТВА	14
Г) ОПИСАНИЕ И ОБОСНОВАНИЕ РЕШЕНИЙ ПО ОТДЕЛКЕ ПОМЕЩЕНИЙ ОСНОВНОГО, ВСПОМОГАТЕЛЬНОГО, ОБСЛУЖИВАЮЩЕГО И ТЕХНИЧЕСКОГО НАЗНАЧЕНИЯ	14
Д) ОПИСАНИЕ АРХИТЕКТУРНЫХ РЕШЕНИЙ, ОБЕСПЕЧИВАЮЩИХ ЕСТЕСТВЕННОЕ ОСВЕЩЕНИЕ ПОМЕЩЕНИЙ С ПОСТОЯННЫМ ПРЕБЫВАНИЕМ ЛЮДЕЙ.	18
Е) ОПИСАНИЕ АРХИТЕКТУРНО-СТРОИТЕЛЬНЫХ МЕРОПРИЯТИЙ, ОБЕСПЕЧИВАЮЩИХ ЗАЩИТУ ПОМЕЩЕНИЙ ОТ ШУМА, ВИБРАЦИИ И ДРУГОГО ВОЗДЕЙСТВИЯ.	18
Ж) ОПИСАНИЕ РЕШЕНИЙ ПО СВЕТООГРАЖДЕНИЮ ОБЪЕКТА, ОБЕСПЕЧИВАЮЩИХ БЕЗОПАСНОСТЬ ПОЛЕТА ВОЗДУШНЫХ СУДОВ (ПРИ НЕОБХОДИМОСТИ)	19
З) ОПИСАНИЕ И ОБОСНОВАНИЕ ПРИНЯТЫХ ОБЪЕМНО-ПЛАНИРОВОЧНЫХ РЕШЕНИЙ ОБЪЕКТА КАПИТАЛЬНОГО СТРОИТЕЛЬСТВА, ОБЕСПЕЧИВАЮЩИХ В ТОМ ЧИСЛЕ СОБЛЮДЕНИЕ САНИТАРНО-ЭПИДЕМИОЛОГИЧЕСКИХ ТРЕБОВАНИЙ	19
З1) СВЕДЕНИЯ О НОМЕНКЛАТУРЕ, КОМПОНОВКЕ И ПЛОЩАДЯХ ОСНОВНЫХ ПРОИЗВОДСТВЕННЫХ, ЭКСПЕРИМЕНТАЛЬНЫХ, СБОРОЧНЫХ, РЕМОНТНЫХ И ИНЫХ ЦЕХОВ, А ТАКЖЕ ЛАБОРАТОРИЙ, СКЛАДСКИХ И АДМИНИСТРАТИВНО-БЫТОВЫХ ПОМЕЩЕНИЙ, ИНЫХ ПОМЕЩЕНИЙ ВСПОМОГАТЕЛЬНОГО И ОБСЛУЖИВАЮЩЕГО НАЗНАЧЕНИЯ - ДЛЯ ОБЪЕКТОВ ПРОИЗВОДСТВЕННОГО НАЗНАЧЕНИЯ.	20
З2) ОБОСНОВАНИЕ НОМЕНКЛАТУРЫ, КОМПОНОВКИ И ПЛОЩАДЕЙ ПОМЕЩЕНИЙ ОСНОВНОГО, ВСПОМОГАТЕЛЬНОГО, ОБСЛУЖИВАЮЩЕГО НАЗНАЧЕНИЯ И ТЕХНИЧЕСКОГО НАЗНАЧЕНИЯ - ДЛЯ ОБЪЕКТОВ НЕПРОИЗВОДСТВЕННОГО НАЗНАЧЕНИЯ.	20

Согласовано:			Е) ОПИСАНИЕ АРХИТЕКТУРНО-СТРОИТЕЛЬНЫХ МЕРОПРИЯТИЙ, ОБЕСПЕЧИВАЮЩИХ ЗАЩИТУ ПОМЕЩЕНИЙ ОТ ШУМА, ВИБРАЦИИ И ДРУГОГО ВОЗДЕЙСТВИЯ. 18					
			Ж) ОПИСАНИЕ РЕШЕНИЙ ПО СВЕТООГРАЖДЕНИЮ ОБЪЕКТА, ОБЕСПЕЧИВАЮЩИХ БЕЗОПАСНОСТЬ ПОЛЕТА ВОЗДУШНЫХ СУДОВ (ПРИ НЕОБХОДИМОСТИ) 19					
			З) ОПИСАНИЕ И ОБОСНОВАНИЕ ПРИНЯТЫХ ОБЪЕМНО-ПЛАНИРОВОЧНЫХ РЕШЕНИЙ ОБЪЕКТА КАПИТАЛЬНОГО СТРОИТЕЛЬСТВА, ОБЕСПЕЧИВАЮЩИХ В ТОМ ЧИСЛЕ СОБЛЮДЕНИЕ САНИТАРНО-ЭПИДЕМИОЛОГИЧЕСКИХ ТРЕБОВАНИЙ 19					
			31) СВЕДЕНИЯ О НОМЕНКЛАТУРЕ, КОМПОНОВКЕ И ПЛОЩАДЯХ ОСНОВНЫХ ПРОИЗВОДСТВЕННЫХ, ЭКСПЕРИМЕНТАЛЬНЫХ, СБОРОЧНЫХ, РЕМОНТНЫХ И ИНЫХ ЦЕХОВ, А ТАКЖЕ ЛАБОРАТОРИЙ, СКЛАДСКИХ И АДМИНИСТРАТИВНО-БЫТОВЫХ ПОМЕЩЕНИЙ, ИНЫХ ПОМЕЩЕНИЙ ВСПОМОГАТЕЛЬНОГО И ОБСЛУЖИВАЮЩЕГО НАЗНАЧЕНИЯ - ДЛЯ ОБЪЕКТОВ ПРОИЗВОДСТВЕННОГО НАЗНАЧЕНИЯ. 20					
			32) ОБОСНОВАНИЕ НОМЕНКЛАТУРЫ, КОМПОНОВКИ И ПЛОЩАДЕЙ ПОМЕЩЕНИЙ ОСНОВНОГО, ВСПОМОГАТЕЛЬНОГО, ОБСЛУЖИВАЮЩЕГО НАЗНАЧЕНИЯ И ТЕХНИЧЕСКОГО НАЗНАЧЕНИЯ - ДЛЯ ОБЪЕКТОВ НЕПРОИЗВОДСТВЕННОГО НАЗНАЧЕНИЯ..... 20					
Взам. инв. №	Подп. и дата							
Инв. № подл.	2024-00375-00-0-AP.T4							
	Изм.	Кол.уч.	Лист	№док.	Подп.	Дата		
	Разработал	Рахманова			02.25	Тектовая часть		
	Проверил	Уклеин			02.25			
ГИП	Пильгуй			02.25				
						Стадия	Лист	Листов
						П	1	22
						 МОСЖИЛ НИИПРОЕКТ		

Перечень нормативных документов, используемых при проектировании.

При разработке раздела учтены требования следующих нормативных документов:

Постановление Правительства РФ от 16.02.2008 N 87 "О составе разделов проектной документации и требованиях к их содержанию"

Федерального закон от 30.12.2009 №384-ФЗ «Технический регламент о безопасности зданий и сооружений»:

СП 118.13330.2022 «Общественные здания и сооружения»;

СП 29.13330.2011 «Полы». Актуализированная редакция СНиП 2.03.13-88;

СП 17.13330.2017 «Кровли». Актуализированная редакция СНиП II-26-76;

Постановление Правительства РФ от 26 декабря 2014 г. N 1521 "Об утверждении перечня национальных стандартов и сводов правил (частей таких стандартов и сводов правил), в результате применения которых на обязательной основе обеспечивается соблюдение требований;

Федерального закона "Технический регламент о безопасности зданий и сооружений";

СП 112.13330.2012 «Пожарная безопасность зданий и сооружений»;

СП 1.13130.2020 «Системы противопожарной защиты. Эвакуационные пути и выходы»;

СП 2.13130.2020 «Системы противопожарной защиты. Обеспечение огнестойкости объектов защиты»;

СП 4.13130.2013 «Системы противопожарной защиты. Ограничение распространения пожара на объектах защиты. Требования к объемно-планировочным и конструктивным решениям».

Общая часть.

Здание, подлежащее капитальному ремонту, является структурным подразделением Государственного бюджетного общеобразовательного учреждения города Москвы «ГБОУ Москвы «Школа № 1574» по адресу: г. Москва, пер. Старопимновский, д.5

Раздел "Объемно-планировочные и архитектурные решения" выполнен в соответствии с

Приказом Департамента капитального ремонта №01-12-1369/24 от 28.12.2024 «О внесении изменений в приказ Департамента образования и науки города Москвы от 11 июля 2024 № 01-12-712/24», Приложением №1 к приказу №01-12-1369/24 от 28.12.2024 - Адресный перечень объектов на 2025-2027 годы, на которых запланировано проведение ДКР Москвы мероприятий по капитальному ремонту в рамках реализации Государственной программы города Москвы, Технологическим заданием №2/28-1074 и приложением Стандарт «МОСКОВСКАЯ ШКОЛА. Модернизация объектов образования».

а) Описание внешнего вида объекта капитального строительства, описание и обоснование пространственной, планировочной и функциональной организации объекта капитального строительства

В соответствии с заданием на проектирование предусмотрен капитальный ремонт объекта социальной инфраструктуры города Москва.

Существующее здание школы построено в 1895 году по индивидуальному проекту в осях 1-17/А-К с последующей реконструкцией в 1952 году и пристройкой в осях 17-21/А-Л в 1973 году.

Здание 2х-5этажное сложной формы, с подвальным этажом, неэксплотируемой скатной кровлей.

За относительную отметку 0,000 принят уровень чистого пола первого этажа здания и соответствует абсолютной отметке +164.300. Верхняя отметка здания составляет +27,600/191,900.

Инв. № подл.	Подп. и дата	Взам. инв. №	а) Описание внешнего вида объекта капитального строительства, описание и обоснование пространственной, планировочной и функциональной организации объекта капитального строительства							
			В соответствии с заданием на проектирование предусмотрен капитальный ремонт объекта социальной инфраструктуры города Москва.							
			Существующее здание школы построено в 1895 году по индивидуальному проекту в осях 1-17/А-К с последующей реконструкцией в 1952 году и пристройкой в осях 17-21/А-Л в 1973 году.							
			Здание 2х-5этажное сложной формы, с подвальным этажом, неэксплотируемой скатной кровлей.							
За относительную отметку 0,000 принят уровень чистого пола первого этажа здания и соответствует абсолютной отметке +164.300. Верхняя отметка здания составляет +27,600/191,900.										
						2024-00375-00-0-АР.ТЧ				Лист
										2
Изм.	Кол.уч.	Лист	№док.	Подп.	Дата					

Высоты этажей (от пола до низа перекрытия):

Подвал (-2 уровень)– 2,410 м

Подвал (-1 уровень) – 2,930-3,370 в осях 1-17/А-К 2,960 - в осях 17-21/А-Л

1 этаж – 3,680 м в осях 1-17/А-К 3,960- в осях 17-21/А-Л

2 этаж – 4,950-6,370 м в осях 1-17/А-К 2,930-6440 - в осях 17-21/А-Л

3 этаж – 3,300-4,800 м в осях 1-17/А-К

4 этаж – 3,380 м в осях 1-17/А-К

5 этаж – 3,670-4,410 м в осях 1-17/А-К

Относительные отметки уровня чистого пола с подвального этажа по 5-й этажи проектом не изменяются.

Объемно-планировочные решения здания –коридорного типа с продольными и поперечными несущими стенами.

Фундаменты под несущие стены выполнены ленточными из глиняного кирпича и камня известняка. Под пристройкой выполнен так же ленточный фундамент из бетонных блоков ФБС и сборных ж/б плит.

Наружные стены – кирпичные.

Внутренние несущие стены выполнены из кирпича.

Основная часть перегородок выполнена из:

- В подвале из полнотельного кирпича толщиной 120 мм на цементно-песчаном растворе

- В наземной части из газобетонных блоков толщиной 120мм, плотностью D600

- Зашивки коммуникаций - каркасные перегородки из ГКЛВ.

Кровля в осях 17-21/А-Л плоская с внутренним водостоком и без чердачного пространства. Кровля в осях 1-17/А-К скатная из оцинкованных металлических листов по деревянной обрешетке.

Главный вход оборудован одномаршевой лестницей из десяти ступеней, высота подступенка 150мм, глубина проступи – 300мм и пандусом с уклоном не более 5%.

Поэтажное размещение помещений остаются без изменений:

В подвальном этаже (-2 уровень) (отм. -6,180) размещены:

Помещения для прокладки коммуникаций

В подвальном этаже (отм. -3,850/-4,270) размещены:

-Технические помещения: венткамеры, ИТП, электрощитовая, кроссовая, помещения для прокладки коммуникаций, насосная, узел ввода,.

-Помещения спортивного зала ЛФК, включая раздевальные (с душем и санузлами), снарядная

-Помещения общего пользования: коридоры, санузлы, умывальная

На 1 этаже (отм. ±0,000) размещены:

- Входная группа с тамбуром, гардеробами для обучающихся и учителей, комната охраны, с/у МГН

-Помещения медблока: Кабинет врача, туалет медблока, процедурный кабинет, место для приготовления дезинфицирующих растворов и хранения уборочного инвентаря

-Помещения общего пользования: коридоры, лестничные клетки, вестибюль;

-Административные и служебно-бытовые помещения: Административный кабинет

-Помещения пищеблока: обеденный зал, горячий цех, холодный цех, моечная столовой посуды, моечная кухонной посуды, доготовочный цех, кладовая сухих продуктов, помещения персонала с душем и санузлом, помещение временного хранения пищевых отходов, загрузочный цех;

-Учебные кабинеты: кабинеты материальной технологии

Инв. № подл.	Подп. и дата	Взам. инв. №	снарядная						
			- Помещения общего пользования: коридоры, санузлы, умывальная						
<u>На 1 этаже (отм. ±0,000) размещены:</u>									
- Входная группа с тамбуром, гардеробами для обучающихся и учителей, комната охраны, с/у МГН									
- Помещения медблока: Кабинет врача, туалет медблока, процедурный кабинет, место для приготовления дезинфицирующих растворов и хранения уборочного инвентаря									
- Помещения общего пользования: коридоры, лестничные клетки, вестибюль;									
- Административные и служебно-бытовые помещения: Административный кабинет									
- Помещения пищеблока: обеденный зал, горячий цех, холодный цех, моечная столовой посуды, моечная кухонной посуды, доготовочный цех, кладовая сухих продуктов, помещения персонала с душем и санузлом, помещение временного хранения пищевых отходов, загрузочный цех;									
- Учебные кабинеты: кабинеты материальной технологии									
						2024-00375-00-0-AP.TЧ			Лист
									3
Изм.	Кол.уч.	Лист	№ док.	Подп.	Дата				

Сантехнические помещения: санузлы для мальчиков и девочек, санузел персонала, ПУИ;
-Технические помещения: кросовая

На 2 этаже (отм. +4,350/3,300) размещены:

- Помещения общего пользования: коридоры, лестничные клетки;
- Зальные помещения: спортивный зал со снарядной, раздевальными (с душем и санузлами), актовый зал

-Учебные кабинеты: кабинеты, Творческая мастерская с кладовой, кабинет иностранного языка

-Административные и служебно-бытовые помещения: Рабочее пространство для учителей

-Сантехнические помещения: санузлы для мальчиков и девочек, санузел персонала, ПУИ;

-Технические помещения: кроссовая.

На 3 этаже (отм. +9,150) размещены:

-Помещения общего пользования: коридоры, лестничные клетки;

-Учебные кабинеты: Кабинеты, информационный библиотечный центр, кабинет иностранного языка

1
-Административные и служебно-бытовые помещения: кабинет для индивидуальных занятий

-Сантехнические помещения: санузлы для мальчиков и девочек, санузел персонала, ПУИ;

-Технические помещения: серверная

На 4 этаже (отм. +14,550) размещены:

-Помещения общего пользования: коридоры, лестничные клетки;

-Учебные кабинеты: кабинеты русского языка и литературы, кабинет истории, кабинеты математики, кабинет биологии с лаборантской

-Сантехнические помещения: санузлы для мальчиков и девочек, ПУИ;

-Административные и служебно-бытовые помещения: кабинет для индивидуальных занятий , административный кабинет

На 5 этаже (отм. +18,450) размещены:

-Помещения общего пользования: коридоры, лестничные клетки;

-Учебные кабинеты: Кабинет иностранного языка, кабинет химии с лаборантской, кабинет информационных технологий, кабинет географии, кабинет русского и литературы, кабинет физики с лаборантской

-Сантехнические помещения: санузлы для мальчиков и девочек, ПУИ;

-Технические помещения: серверная

б) Обоснование принятых объемно-пространственных и архитектурно-художественных решений, в том числе в части соблюдения предельных параметров разрешенного строительства, реконструкции объекта капитального строительства;

В соответствии с Задаанием на проектирование настоящими проектными решениями, проводимым в рамках капитального ремонта, не предусматривается изменение существующего функционального назначения здания и помещений, конструктивных и объемно-планировочных решений, в том числе параметров путей эвакуации и эвакуационных выходов, а также не предусматривается изменение технологических решений помещений (этажей) и технико-экономических показателей. Проектные решения соответствуют существующему состоянию здания и ранее разработанной и утвержденной проектной документации и остаются без изменений.

Инв. № подл.	Подп. и дата	Взам. инв. №	б) Обоснование принятых объемно-пространственных и архитектурно-художественных решений, в том числе в части соблюдения предельных параметров разрешенного строительства, реконструкции объекта капитального строительства;								
			В соответствии с Заданием на проектирование настоящими проектными решениями, проводимым в рамках капитального ремонта, не предусматривается изменение существующего функционального назначения здания и помещений, конструктивных и объемно-планировочных решений, в том числе параметров путей эвакуации и эвакуационных выходов, а также не предусматривается изменение технологических решений помещений (этажей) и технико-экономических показателей. Проектные решения соответствуют существующему состоянию здания и ранее разработанной и утвержденной проектной документации и остаются без изменений.								
			Изм.	Кол.уч.	Лист	№док.	Подп.	Дата	2024-00375-00-0-AP.TЧ		Лист
											4

- замена облицовки ступеней и горизонтальных площадок керамогранитной плиткой на клее 600х600х11 мм противоскользящей по выравнивающей цементно- песчаной стяжке толщ. 20 мм;
- замена ограждения в спуски в подвал из нержавеющей полированной стали высотой 900 мм;
- замена ограждения из нержавеющей стали, расстояние между стойками 100 мм на комбинированном ограждение (подпорная стенка с ограждением из нержавеющей стали) общей высотой 1200 мм.

Входные площадки:

- замена существующей железобетонной лестницы крыльца и пандуса в существующих габаритных размерах на аналогичную главной входной группы см. раздел КР.
- замена горизонтальных поверхностей входных площадок, пандуса керамогранитной плитки на термообработанный гранит 600х300х30 мм в облицовке горизонтальных площадок, ступеней, наклонных частей пандуса и подступенков толщиной 600х300х20 мм;
- замена ограждения на входных площадках на ограждение из нержавеющей полированной стали высотой 1200 мм, поручни на высоте 900 мм и 500 мм с не травмирующим завершением, заполнение ограждения из вертикальных ригелей с шагом не более 100 мм;
- замена ограждения на пандусе на ограждение из нержавеющей полированной стали высотой 1200 мм, поручни на высоте 900 и 700 мм с не травмирующим завершением, заполнение ограждения из вертикальных ригелей с шагом не более 100 мм;
- замена вертикальных поверхностей входных площадок оштукатуривание цементно-песчаным раствором по оцинкованной сетке и облицовкой керамогранитной плиткой 600х600х11 мм на клее;
- замена подшивки горизонтальных поверхностей козырьков входных групп на металлический сайдинг шириной 200 мм;
- замена отливов из оцинкованной стали с заводской окраской парапетных стенок ж/б козырьков;
- замена наружного водостока с козырьков – труба водосточная из оцинкованной стали с полимерным покрытием, Ø 100 мм;
- замена металлических грязезащитных решеток в тамбурах в входных группах.

Кровля в осях 1-17/А-К :

- замена стропил и обрешетки скатной кровли (см. КР)
- Замена оцинкованных листов кровли
- Замена водосточной системы: желоб по периметру тропи и трубы водоотвода
- Замена ограждения кровли (высота 0,6м)
- устройство снегоудержателей
- Замена металлической стремянки П1-1

Замена существующего пирога покрытия чердака:

- гидроизоляция 2 слоя;
- грунтовка
- Цементно-песчаная стяжка 50мм
- диффузионная мембрана
- минераловатные плиты в два слоя 120-160 кг/м³ 200мм

Кровля в осях 17-21/А-Л :

Замена существующего пирога покрытия плоской кровли:

Тип 1:

- существующая ж/б плита
- пароизоляция - 3 мм
- минеральный утеплитель, плотность 115-160кг/м³ (2 слоя) - 200 мм
- уклонообразующий слой из керамзитового гравия - 30-270 мм

Инв. № подл.	Подп. и дата	Взам. инв. №	замена существующего пирога покрытия чердака: - гидроизоляция 2 слоя; - грунтовка - Цементно-песчаная стяжка 50мм - диффузионная мембрана - минераловатные плиты в два слоя 120-160 кг/м3 200мм											
			Кровля в осях 17-21/А-Л : Замена существующего пирога покрытия плоской кровли: Тип 1: -существующая ж/б плита -пароизоляция - 3 мм -минеральный утеплитель, плотность 115-160кг/м3 (2 слоя) - 200 мм -уклонообразующий слой из керамзитового гравия - 30-270 мм											
												2024-00375-00-0-АР.ТЧ		Лист
														6
Изм.	Кол.уч.	Лист	№док.	Подп.	Дата									

-диффузионная мембрана - 1 мм
-стяжка из цементно-песчаного раствора М 150, армированная сеткой 5 Вр-1 100х100 - 50 мм
-грунтовка
-гидроизоляционный битумный материал с полимерной пленкой - 1 слой
-гидроизоляционный битумный материал с крупнозернистой посыпкой с лицевой стороны и полимерной пленкой - 1 слой.
- Замена покрытия парапета кровли из оцинкованной стали;
-замена отливов из оцинкованной стали вент-шахт;
-очистка поверхности парапета от старого покрытия;
-грунтовка и окраска внутренней бетонной поверхности парапета фасадной краской в 2 слоя;
-замена зонтов для вентиляционных шахт из оцинкованной стали;
-замена кровельных аэраторов;
-замена водосточных воронок;

Замена существующего пирога покрытия кровли Тип 2 (Кровля холодных козырьков):
- ж/б плита
-уклонообразующий слой из керамзитового гравия с проливкой цементным молочком - 30-150 мм
-стяжка из цементно-песчаного раствора М 150, армированная сеткой 5 Вр-1 200х200 - 50 мм
-Праймер битумный
-гидроизоляционный битумный материал с полимерной пленкой -2 слоя
-гидроизоляционный битумный материал с крупнозернистой посыпкой с лицевой стороны и полимерной пленкой - 1 слой.
Замена покрытия парапета кровли из оцинкованной стали;
-замена отливов из оцинкованной с порошковой окраской стали парапетов
-очистка кирпичной поверхности парапета от старого покрытия;
-оштукатуривание поверхности парапета цементно пепечаной штукатуркой
-грунтовка и окраска внутренней кирпичной поверхности парапета фасадной краской в 2 слоя;
- замена металлического ограждения кровли (при высоте парапета менее 600мм) высота ограждения кровли 0,6 м;
-замена зонтов для вентиляционных шахт из оцинкованной стали;
-замена кровельных аэраторов;
-замена водосточных воронок;
-замена ходовых дорожек на ходовой настил из ЦПС шириной 1200мм

Замена наружных дверных блоков на аналогичные:

-Наружный дверной блок (выходы из подвала) дверь однопольная металлическая глухая, утепленная, с уплотнением в притворах, оборудованная устройством для самозакрывания. Дверная коробка и полотно - сталь толщиной 1,2 мм, покрытие порошковая окраска, цвет RAL7016;. Порог стационарный плоский 14 мм. Петли каплевидные на подшипниках регулируемые. Замок с сердцевиной ключ-барашек, 100 000 циклов открываний. Цвет замка и цилиндра - никель, цвет круглой накладки на цилиндр - матовый хром. Ручка нажимная типа U-form из нержавеющей стали.

-Наружный дверной блок (выход из лестничных клеток) дверь двупольная (однопольная/полуторная, с боковыми фрамугами) светопрозрачная. Дверь из теплого алюминиевого профиля толщиной 70мм, стеклопакет 32мм, со стороны улицы мультифункциональное закаленное 6мм, терморамка черного цвета толщиной18мм, с заполнением аргоном, безопасный триплекс из 2 стекол толщиной 4мм с двумя пленками внутри по 0,76мм. Порошковая окраска RAL 7016, без

Инв. № подл.	Подл. и дата	Взам. инв. №							Лист
Изм.	Кол.уч.	Лист	№док.	Подп.	Дата	2024-00375-00-0-AP.TЧ			7

замка, доводчик дверной на обе створки со скользящей тягой с регулируемым усилием, скользящая тяга с синхронизацией доводчиков, порог 14мм, Ручки – «антипаника» на основную и пассивную створку двери по ходу эвакуации, с обратной стороны оборудовать основную створку двери нажимной ручкой, электромагнитная защелка нормально-открытая, косой ригель электромагнитной защелки

-Наружный дверной блок (главный вход (тамбур)) двери в светопрозрачные полуторные Дверь из теплого алюминиевого профиля толщиной 70мм, стеклопакет 32мм, со стороны улицы мультифункциональное закаленное 6мм, терморамка черного цвета толщиной 18мм, с заполнением аргоном, безопасный триплекс из 2 стекол толщиной 4мм с двумя пленками внутри по 0,76мм. Порошковая окраска RAL 7016, без замка, доводчик дверной на обе створки со скользящей тягой с регулируемым усилием, скользящая тяга с синхронизацией доводчиков, электромагнитная защелка нормально-открытая, косой ригель электромагнитной защелки, на доборном полотне электромеханический замок с установкой в верхний профиль полотна

Ручки –«антипаника» на второстепенную створку двери по ходу эвакуации, с обратной стороны основную створку оборудовать штангой из нержавеющей стали с сердцевиной ключ-барашек с покраской всех элементов в RAL7016.

-Люк выхода на кровлю - распашной металлический противопожарный 2-го типа с пределом огнестойкости EI30, с уплотнением в притворах, дверная коробка и полотно – сталь с порошковой окраской, размер не менее 600х800 мм.

Оконные и витражные заполнения:

-замена существующих оконных блоков на аналогичные в соответствии с ГОСТ 30674- 2023

Оконный блок из ПВХ профиля армированного (не менее 70мм); Цвет профиля RAL 7016, окрашенный в массу или ламинированный с 2-х сторон; Стеклопакет двухкамерный толщиной 40мм, наружное стекло закаленное(СПД 4М1-12-4М1-12-4М) с мягким селективным покрытием; Внутренне стекло класс защиты SM1; Низкоэмальсинное покрытие внутреннего стекла; Ручка оконная с полимерным покрытием RAL7016; Противовзломные штапики, подставочный профиль; замки безопасности (в нижней части фрамуги на тросике или с "язычком" для возможности проветривания помещения); москитная сетка на одну створку; коэффициент сопротивления теплопередаче не менее 0,61 м2С/Вт; коэффициент звукоизоляции 17дБА ручки на высоте не более 1,7м от ч.п

Оконные блоки в санузлах оклеить матовой пленкой (изнутри) пленка на внутренний слой стекла стеклопакета (в заводских условиях)

При устройстве окна с подоконником мене 550мм нижнее остекление с классом защиты SM4

-замена существующих противопожарных оконных блоков по ГОСТ 30674-99 и ГОСТ 30698-2014:

Витраж из алюминиевого профиля, порошковая окраска профиля RAL7016, заполнение двухкамерным стеклопакетом (огнестойкое стекло Pyrothane100 (6,8,10мм) AGC Flat Glass-14-И4-14-И4) с мягким селективным покрытием, толщиной 42 мм

-замена наружных витражей на витражи из алюминиевого профиля.

Заполнение двухкамерным стеклопакетом, класс защиты остекления SM4 (ГОСТ 30862-2014) с бронированной пленкой толщиной 600 микрон. Порошковая окраска профиля RAL7016. Индивидуального изготовления. Двери в составе наружных витражей оборудованы стационарным порогом h=14 мм. Ручки - «антипаника» на пассивную створку двери по ходу эвакуации, основную створку оборудовать с обеих сторон вертикальной нержавеющей хромированной штангой во всю высоту полотна и комплектом замка (фурнитуры) с сердцевиной ключ-барашек с покраской всех элементов (кроме штанги) в RAL7016, штанга окрашивается в RAL7047;

Взам. инв. №	Витраж из алюминиевого профиля, порошковая окраска профиля RAL7016, заполнение двухкамерным стеклопакетом (огнестойкое стекло Pyrothane100 (6,8,10мм) AGC Flat Glass-14-И4-14-И4) с мягким селективным покрытием, толщиной 42 мм							
Подп. и дата	-замена наружных витражей на витражи из алюминиевого профиля. Заполнение двухкамерным стеклопакетом, класс защиты остекления CM4 (ГОСТ 30862-2014) с бронированной пленкой толщиной 600 микрон. Порошковая окраска профиля RAL7016. Индивидуального изготовления. Двери в составе наружных витражей оборудованы стационарным порогом h=14 мм. Ручки - «антипаника» на пассивную створку двери по ходу эвакуации, основную створку оборудовать с обеих сторон вертикальной нержавеющей хромированной штангой во всю высоту полотна и комплектом замка (фурнитуры) с сердцевиной ключ-барашек с покраской всех элементов (кроме штанги) в RAL7016, штанга окрашивается в RAL7047;							
Инд. № подл.							2024-00375-00-0-AP.TЧ	Лист
								8
Изм.	Кол.уч.	Лист	№ док.	Подп.	Дата			

- замена москитной сетки на одну поворотно-откидную створку;
- замена металлических рольставней в помещениях пищеблока;
- замена оконных откосов: улучшенная штукатурка по стекловолоконной сетке, шпаклевка, финишная шпаклевка в 2 слоя, грунтовка, окраска стен;
- замена ПВХ подоконных досок на подоконник с экраном радиаторов, березовая фанера толщиной 24 мм, фасад из МДФ 12 мм, окраска с обеих сторон, материалы с зафальцованными краями и отшлифованными поверхностями, противопожарная обработка, и замена ПВХ подоконных досок на подоконник из керамогранита 600х600х9 мм. Подоконники окон второго света – улучшенная штукатурка, шпаклевка. Грунтовка, окраска.

Заменяемые окна в наружных стенах коридоров и зальных помещений, не оборудованных противодымной вентиляцией, предусмотрены в соответствии с п. 8.5 СП 7.13130.2013. Заменяемые окна в коридорах предусмотрены открываемыми с расположением верхней кромки не ниже 2,5 м и нижней кромки не выше 1,5 м от уровня пола из расчета: одно открываемое окно шириной не менее 1,6 м на каждые 30 м коридора. Заменяемые окна в помещениях предусмотрены с аналогичными открываемыми проёмами из расчета: не менее 0,24 м на 1 м длины наружного ограждения помещений при максимально расстоянии от его внутренних ограждений не более 20 м. Запорные устройства или механизмы таких окон предусмотрены доступными для свободного открывания и неограниченного ручного открывания заполнений таких проемов при расположении соответствующих конструктивных элементов (рычагов, ручек и др.) не выше 1,7 м от уровня пола.

Внутренние виды работ.

Стены и перегородки:

- расчистка, обработка существующих стен подвала противогрибковым средством;
- расчистка, локальная обработка противогрибковым средством с устройством звукоизоляции из минераловатных плит толщиной 100 мм и штукатурного слоя по сетке с подготовкой с последующей покраской несущих стен помещений подвала: ИТП/Водомерный узел, Венткамера, Насосная
- замена ненесущих перегородок в помещениях подвала на перегородки из кирпича с устройством штукатурного слоя с грунтовкой глубокого проникновения с подготовкой под финишную отделку;
- расчистка, локальная обработка противогрибковым средством и ремонт штукатурного слоя несущих стен с подготовкой под финишную отделку 1-5 этаж;
- замена ненесущих перегородок в помещениях на 1-5 этажах на перегородки из газобетонных блоков с подготовкой под финишную отделку;
- устройство усиления существующих дверных проемов во всех несущих внутренних и наружных стенах (см. в раздел КР);
- замена зашивки инсталляции в санузлах листами ГКЛВ в 2 слоя по металлическому каркасу с подготовкой под финишную отделку;
- замена Т-образного профиля из нержавеющей стали на стыках двух типов напольных покрытий, цвет матовый хром;
- замена модульных сантехнических перегородок в санузлах высотой 2000 мм, 200 мм от уровня пола, на перегородки из влагостойкого HPL пластика толщиной 12 мм (цвет под дерево), на алюминиевом профиле);
- устройство ограждения из кубообразных реек в помещении обеденного зала и входной зоны из алюминия, сечение 80х80 мм с шагом между рейками 80 мм, цвет по дерево, группа горючести НГ;

Полы:

Существующая конструкция полов подвала демонтируется.

Инв. № подл.	Подп. и дата	Взам. инв. №	наружных стенах (см. в раздел КР); -замена зашивки инсталляции в санузлах листами ГКЛВ в 2 слоя по металлическому каркасу с подготовкой под финишную отделку; -замена Т-образного профиля из нержавеющей стали на стыках двух типов напольных покрытий, цвет матовый хром; -замена модульных сантехнических перегородок в санузлах высотой 2000 мм, 200 мм от уровня пола, на перегородки из влагостойкого HPL пластика толщиной 12 мм (цвет под дерево), на алюминиевом профиле); -устройство ограждения из кубообразных реек в помещении обеденного зала и входной зоны из алюминия, сечение 80х80 мм с шагом между рейками 80 мм, цвет по дерево, группа горючести НГ; <u>Полы:</u> Существующая конструкция полов подвала демонтируется.						
Изм.	Кол.уч.	Лист	№док.	Подп.	Дата	2024-00375-00-0-AP.TЧ			Лист
									9

- Устройство нового бетонного основания выполняется на существующей отметке, общая толщина конструкции основания сохраняется существующей;
- замена основания полов в цокольном этаже – цементно-песчаная стяжка 40-60мм с устройством обмазочной гидроизоляции и покрытием керамогранитной плиткой
- замена основания полов на 1-5 этажах (цементно-песчаная стяжка 40-60мм армированная сеткой 5BP1 100x100 с устройством гидроизоляции с заведением на стены в помещениях с мокрыми процессами) с заменой напольных покрытий (керамогранитная плитка, линолеум, дизайн-плитка ПВХ, спортивный паркет, ковровое покрытие);
- замена напольного плинтуса на 1-5 этажах (керамогранитный, коннелюрный, ПВХ, вентилируемый деревянный);

Потолки:

- расчистка, обработка ж/б плит потолка подвала противогрибковым средством;
- расчистка, локальная обработка противогрибковым средством с устройством звукоизоляции из минераловатных плит толщиной 100 мм и штукатурного слоя по сетке с подготовкой с последующей покраской потолка помещений подвала: ИТП/Водомерный узел, Венткамера
- расчистка, локальная обработка противогрибковым средством и ремонт штукатурного слоя потолка с последующей покраской помещений 1-5 этажа (потолки с окраской, потолки с подвесными декоративными подвесными панелями, грильято);
- расчистка запотолочного пространства и заменой подвесных потолков (кассетный акустический, кассетный алюминиевый) помещений 1-5 этажа;
- устройство ниш для рулонных штор из ГВЛ

Ограждения лестниц:

- замена ограждений: нержавеющая сталь, расстояние между стойками 100 мм, высота ограждения 1200 мм, поручни на высоте 900 мм и 500 мм. Горизонтальные завершения поручней длиной 300 мм. На лестничных площадках последних этажей предусмотрен повышенный уровень ограждения (до перекрытия). Замена ограждений предусматривается в существующих габаритах и не уменьшает существующие геометрические параметры путей эвакуации по лестницам. При этом расстояние между маршами (ограждениями) составляет не менее 75 мм для прокладки пожарных рукавов. Марши и площадки лестничных клеток не подлежат замене, а их ширина остается в прежних габаритах;
- замена внутренних металлических ограждений оконных проемов на промежуточных площадках лестничных клеток из нержавеющей полированной стали высотой 1200 мм, заполнение ограждения из вертикальных ригелей с шагом не более 100 мм.
- замена ограждений на металлическое с покраской в помещениях цокольного этажа: Венткамера, ИТП

Двери внутренние:

Двери эвакуационных выходов из поэтажных коридоров, холлов, фойе, вестибюлей и лестничных клеток не должны иметь запоров, препятствующих их свободному открыванию изнутри без ключа (п.4.2.7 СП 1.13130.2020, ст.6 № 123-ФЗ). При установке СКУД на дверях должно обеспечиваться автоматическое открывание запоров дверей по сигналу систем противопожарной защиты здания. Все двупольные двери эвакуационных выходов оборудовать "Антипаникой", при этом обе створки должны быть активными. Двери эвакуационных выходов из помещений с принудительной противодымной защитой, в том числе из коридоров, должны быть оборудованы приспособлениями для самозакрывания (координаторов последовательного закрывания) и уплотнением в притворах (п.4.2.7 СП 1.13130.2020, ст.6 № 123-ФЗ).

-В учебных кабинетах, в обеденном зале:

Дверной блок алюминиевый остекленный с телескопической алюминиевой дверной коробкой с алюминиевыми доборами, площадь остекления двери не менее 70% от площади

Взам. инв. №		Подп. и дата		Венткамера, ИПП			
Инв. № подл.				<u>Двери внутренние:</u>			
				Двери эвакуационных выходов из поэтажных коридоров, холлов, фойе, вестибюлей и лестничных клеток не должны иметь запоров, препятствующих их свободному открыванию изнутри без ключа (п.4.2.7 СП 1.13130.2020, ст.6 № 123-ФЗ). При установке СКУД на дверях должно обеспечиваться автоматическое открывание запоров дверей по сигналу систем противопожарной защиты здания. Все двупольные двери эвакуационных выходов оборудовать "Антипаникой", при этом обе створки должны быть активными. Двери эвакуационных выходов из помещений с принудительной противодымной защитой, в том числе из коридоров, должны быть оборудованы приспособлениями для самозакрывания (координаторов последовательного закрывания) и уплотнением в притворах (п.4.2.7 СП 1.13130.2020, ст.6 № 123-ФЗ). -В учебных кабинетах, в обеденном зале: Дверной блок алюминиевый остекленный с телескопической алюминиевой дверной коробкой с алюминиевыми доборами, площадь остекления двери не менее 70% от площади			
						2024-00375-00-0-AP.TЧ	Лист
							10
Изм.	Кол.уч.	Лист	№док.	Подп.	Дата		

дверного полотна, размер наличника коробки по петлевой стороне не менее 55х9мм, с обратной стороны 68х9, RAL 7016, толщина профиля дверного полотна 64мм, заполнение дверного полотна - стекло-триплекс с 2-х сторон с закаленными стеклами 4мм, замок механический роликовый замок с цилиндровым механизмом, доводчик дверной со скользящей тягой с регулируемым усилием EN-1-4, встроенным фиксатором в открытом положении и встроенным ограничителем угла открывания дверного полотна, RAL 7016, петли роликовые регулируемые, звукоизоляция 32 дБ. ручка - с обеих сторон вертикальная штанга во всю высоту полотна ; замки с цилиндровым механизмом и личинкой "ключ-барашек", выпадающий порог

-В административных кабинетах, санузлы и душевые в раздевальнях, в санузлах для МГН, раздевальных при спортзалах, в комнате личной гигиены девочек д:

Дверной блок алюминиевый остекленный с телескопической алюминиевой дверной коробкой с алюминиевыми доборами, площадь остекления двери не менее 70% от площади дверного полотна, размер наличника коробки по петлевой стороне не менее 55х9мм, с обратной стороны 68х9, RAL 7016, толщина профиля дверного полотна 64мм, заполнение дверного полотна - стекло-триплекс с 2-х сторон с закаленными стеклами 4мм, замок механический роликовый замок с цилиндровым механизмом, доводчик дверной со скользящей тягой с регулируемым усилием EN-1-4, встроенным фиксатором в открытом положении и встроенным ограничителем угла открывания дверного полотна, RAL 7016, петли роликовые регулируемые, класс безопасности CM4, звукоизоляция 32 дБ - нержавеющая сталь. Цилиндр под замок: ключ-ключ. Ручка - с обеих сторон вертикальная штанга во всю высоту полотна ; замки с цилиндровым механизмом и личинкой "ключ-ключ"; Оклеить матовой пленкой (изнутри) пленка на внутренний слой стекла стеклопакета (в заводских условиях); Видимый профиль не более 70мм; выпадающий порог

-В коридорах (при делении коридора на части) и на лестничных клетках:

Дверной блок алюминиевый остекленный с телескопической алюминиевой дверной коробкой с алюминиевыми доборами, площадь остекления двери не менее 70% от площади дверного полотна, размер наличника коробки по петлевой стороне не менее 55х9мм, с обратной стороны 68х9, RAL 7016, толщина профиля дверного полотна 64мм, заполнение дверного полотна - стекло-триплекс с 2-х сторон с закаленными стеклами 4мм, замок механический роликовый замок с цилиндровым механизмом, доводчик дверной со скользящей тягой с регулируемым усилием EN-1-4, встроенным фиксатором в открытом положении и встроенным ограничителем угла открывания дверного полотна, RAL 7016, петли роликовые регулируемые, звукоизоляция 32 дБ, нажимная ручка снаружи и ручка антипаника на обе створки; оборудовать устройством координаторов последовательного закрывания; Видимый профиль не более 70мм; выпадающий порог

-В электрощитовой, серверной:

Дверной блок металлический сталь толщиной 1,2мм, полотно и коробка окрашены порошковой краской, порог плоский 3, 14мм, с притвором 13/24 и 23/41, автоматический; петли каплевидные 2 шт на сворку на подшипниках регулируемые, доводчик типа DL77/ Dorma TS 68, выдерживающий 100 000 циклов открываний, цвет замка и цилиндра никель/хром, устойчива к влажной убоке -В помещениях пищеблока дверь однопольная, глухая, ПВХ толщина не менее 40 мм. Без порога. Фурнитура: петли врезные цилиндрические усиленные, врезной замок с цилиндровым механизмом с нажимной ручкой Inox, нержавеющая сталь, ограничитель.

-В санузлах и душевых персонала пищеблока и медблока:

Дверь композитная глухая из ПВХ 1,5мм, влагостойкая 100%, коробка, наличник, полотно, толщина полотна 38-42мм, обвязка полотна лвл-брус, Торец гладкий, без порога, зазор от пола до полотна 20-30мм, коробка телескопическая, наличники ПВХ с двух сторон, цвет белый, замок с язычком, круглая накладка на цилиндр толщиной не менее 9-10мм, цвет матовый никель, ручка нажимная раздельная на квадратной розетке, выдерживающая 100 000 циклов открываний, петли накладные бабочки, цвет хром, замок с цилиндром ключ/вертушка, доводчик накладной типа DL Smart с функцией задержки в открытом положении HOLD OPEN с рычажной тягой ФОП для ММГН, выдерживающий 100 000 циклов открываний

Инв. № подл.	Подп. и дата	Взам. инв. №	порошковой краской, порог плоский 3, 1 мм, с притвором TS/27 и 23/71, автоматический, петли каплевидные 2 шт на сворку на подшипниках регулируемые, доводчик типа DL77/ Dorma TS 68, выдерживающий 100 000 циклов открываний, цвет замка и цилиндра никель/хром, устойчива к влажной убоке -В помещениях пищеблока дверь однопольная, глухая, ПВХ толщина не менее 40 мм. Без порога. Фурнитура: петли врезные цилиндрические усиленные, врезной замок с цилиндровым механизмом с нажимной ручкой Inox, нержавеющая сталь, ограничитель. -В санузлах и душевых персонала пищеблока и медблока: Дверь композитная глухая из ПВХ 1,5мм, влагостойкая 100%, коробка, наличник, полотно, толщина полотна 38-42мм, обвязка полотна лвл-брус, Торец гладкий, без порога, зазор от пола до полотна 20-30мм, коробка телескопическая, наличники ПВХ с двух сторон, цвет белый, замок с язычком, круглая накладка на цилиндр толщиной не мнее 9-10мм, цвет матовый никель, ручка нажимная раздельная на квадратной розетке, выдерживающая 100 000 циклов открываний, петли накладные бабочки, цвет хром, замок с цилиндром ключ/вертушка, доводчик накладной типа DL Smart с функцией задержки в открытом положении HOLD OPEN с рычажной тягой ФОП для ММГН, выдерживающий 100 000 циклов открываний					
Изм.	Кол.уч.	Лист	№ док.	Подп.	Дата	2024-00375-00-0-AP.TЧ		Лист
								1

Двери пищеблока:

Дверь композитная глухая из ПВХ 1,5мм, влагостойкая 100%, коробка, наличник, полотно, толщина полотна 38-42мм, обвязка полотна лвл-брус, Торец гладкий, без порога, зазор от пола до полотна 20-30мм, коробка телескопическая, наличники ПВХ с двух сторон, цвет белый, замок с язычком, круглая накладка на цилиндр толщиной не менее 9-10мм, цвет матовый никель, ручка нажимная раздельная на квадратной розетке, выдерживающая 100 000 циклов открываний, петли накладные бабочки, цвет хром, замок с цилиндром ключ/вертушка, доводчик накладной типа DL Smart с функцией задержки в открытом положении HOLD OPEN с рычажной тягой ФОП для ММГН, выдерживающий 100 000 циклов открываний с отбойной пластиной на уровне ног и рук

-В помещениях хранения и технических помещениях категории В3:

- Дверь двупольная (или однопольная) металлическая глухая противопожарная, материал дверной коробки и полотна - сталь толщиной 1,2мм, замкнутая по периметру коробка, порог единый с коробкой, полотно и коробка окрашены порошковой краской, RAL 7016, петли каплевидные 2 шт на створку на подшипниках регулируемые, ручки нажимные на декоративной планке U-form(нержавеющая сталь) цвет замка и цилиндра никель/хром, выпадающий порог Дверь противопожарная 2- го типа с пределом огнестойкости EI30.

-В вент камерах двери противопожарные 2 типа

- в насосной, в помещении водомерного узла, в снарядной, в помещениях хранения категории В4, ИТП :

- Дверной блок металлический сталь толщиной 1,2мм, полотно и коробка окрашены порошковой краской, RAL7016, порог плоский 14мм, с притвором 13/24 и 23/41, автоматический; петли каплевидные 2 шт на сворку на подшипниках регулируемые, доводчик типа DL77/ Dorma TS 68, выдерживающий 100 000 циклов открываний, цвет замка и цилиндра никель/хром, устойчива к влажной убоке

На противопожарных дверях и дверях, выходящих в коридор с дымоудалением, необходимо предусматривается установка с приспособлением для самозакрывания (доводчиков)

Трансформируемые перегородки:

-замена существующих трансформируемых перегородок на аналогичные.

Раздвижная модульная устойчивая каркасная конструкция с заполнением звукоизоляционными панелями (плотностью не менее 35 кг/м3, группа горючести - НГ). Перемещение панелей на бесшумных подвесах, в системе направляющих профилей, с использованием ограничителей хода. Для проведения учебных процессов в каждой из двух частей помещения, разделяемого трансформируемой перегородкой, обеспечены нормативные параметры расстановки оборудования, уровни естественной и искусственной освещенности, отопления, вентиляции и звукопоглощения.

Внутренние витражи:

Перегородка светопрозрачная с двойным остеклением, толщина перегородки 75мм, видимая часть нащельника 26мм, RAL 7016(муар) стекло M1, класс защиты CM4, оклеен защитной пленкой с 2 сторон, для противопожарного исполнения- профиль с эндотермическим расширением и терморазрывом, в порошковой полиэфирной ераске, стекло многослойное противопожарное прозрачное серии СПМ дверь в составе : Дверной блок алюминиевый остекленный, площадь остекления двери не менее 70% от площади дверного полотна, размер наличника коробки по петлевой стороне не менее 55х9мм, с обратной стороны 68х9, RAL 7016, толщина профиля дверного полотна 64мм, заполнение дверного полотна - стекло-триплекс с 2-х сторон с закаленными стеклами4мм, замок механический роликовый замок с цилиндрическим механизмом, доводчик дверной сос кользящей тягой с регулируемым усилием EN-1-4, встроенным фиксатором в окрытом положении и встроенным ограничителем угла открывания дверного полотна, RAL 7016, без дверного порога, вертикальная ручка скоба на всю высоту двери, крепление ручек выполнить из нержавеющей стали толщиной 5мм AISI304 со шлифованной поверхностью. Поручень с диаметром трубы 32-35мм, и толщиной стенки не менее

Инв. № подл.	Подп. и дата	Взам. инв. №	Перегородка светопрозрачная с двойным остеклением, толщина перегородки 75мм, видимая часть нащельника 26мм, RAL 7016(муар) стекло M1, класс защиты CM4, оклеен защитной пленкой с 2 сторон, для противопожарного исполнения- профиль с эндотермическим расширением и терморазрывом, в порошковой полиэфирной ераске, стекло многослойное противопожарное прозрачное серии СПМ дверь в составе : Дверной блок алюминиевый остекленный, площадь остекления двери не менее 70% от площади дверного полотна, размер наличника коробки по петлевой стороне не менее 55х9мм, с обратной стороны 68х9, RAL 7016, толщина профиля дверного полотна 64мм, заполнение дверного полотна - стекло-триплекс с 2-х сторон с закаленными стеклами4мм, замок механический роликовый замок с цилиндрическим механизмом, доводчик дверной сос кользящей тягой с регулируемым усилием EN-1-4, встроенным фиксатором в окрытом положении и встроенным ограничителем угла открывания дверного полотна, RAL 7016, без дверного порога, вертикальная ручка скоба на всю высоту двери, крепление ручек выполнить из нержавеющей стали толщиной 5мм AISI304 со шлифованной поверхностью. Поручень с диаметром трубы 32-35мм, и толщиной стенки не менее					
			2024-00375-00-0-AP.TЧ					
			Изм.	Кол.уч.	Лист	№док.	Подп.	Дата

Лист
12

3мм, петли роликовые регулируемые, класс безопасности СМ4, звукоизоляция 32 дб и оборудованы устройством последовательного закрывани.

61) Обоснование принятых архитектурных решений в части обеспечения соответствия зданий, строений и сооружений установленным требованиям энергетической эффективности (за исключением зданий, строений, сооружений, на которые требования энергетической эффективности не распространяются).

Выбор данных решений обусловлен следующими факторами:

- территориальное расположение проектируемого объекта – выбор климатических параметров, расчеты приведенных сопротивлений теплопередаче ограждающих конструкций, расчеты энергетических параметров здания, выполненных с учетом размещения объекта;
- функциональное назначение проектируемого объекта – выбор параметров внутреннего воздуха, архитектурных, функционально – технологических, конструктивных и инженерных решений выполнено согласно назначению и использованию данного объекта;
- действующая нормативная документация – проектными решениями учтены требования нормативных документов по обеспечению соответствия здания требованиям энергетической эффективности и требованиям оснащенности их приборами учета используемых энергетических ресурсов.

62) Перечень мероприятий по обеспечению соблюдения установленных требований энергетической эффективности к архитектурным решениям, влияющим на энергетическую эффективность зданий, строений и сооружений (за исключением зданий, строений, сооружений, на которые требования энергетической эффективности не распространяются).

Ограждающие конструкции проектируемого здания разработаны с учетом нормативных требований по энергоэффективности, см. Раздел ЭЭ. В проектных решениях применяются современные материалы, имеющие высокие теплоизоляционные свойства:

- Утепление стен чердака (кирпичные стены толщиной 400мм) в осях 7-14/Д-Ж минераловатными плитами 110кг/м³ толщиной 100мм
- утепление наружных стен фасада минеральными плитами, плотность 110 кг/м³, 150 мм, с нахлестом на оконные и витражные блоки d_н=20мм;
- утепление наружных стен отапливаемого подвала на высоту 300 мм от ур.з. и наружных стен в уровне прямков плитами из пеностекла, плотность 90 кг/м³, толщиной 150 мм;
- наружные стены отапливаемого подвала, заглубленные в грунт, не утепляются
- утепление кровли (перекрытия над третьим и четвертым этажом) минеральный утеплитель, плотность 115/160 кг/м³. толщиной 200 мм в 2 слоя
- утепление стен тамбура минеральным утеплителем толщиной 100 мм, плотностью 80-125 кг/м³;
- утепление потолка тамбура минераловатным утеплителем 130кг/м³ толщиной 200мм в 2 слоя с последующим оштукатуриванием
- утепление парапетов утепленных покрытий на высоту минимум 500 мм,
- замена оконных блоков в ПВХ профиле с двухкамерным стеклопакетом с мягким селективным покрытием. Приведенное сопротивление теплопередаче оконного блока из ПВХ профилей с двухкамерным стеклопакетом с сопротивлением теплопередаче расчетное RR_o 0,618 (м² · °C)/Вт;

Инв. № подл.	Подп. и дата	Взам. инв. №	- утепление наружных стен отапливаемого подвала на высоту 300 мм от ур.з. и наружных стен в уровне прямков плитами из пеностекла, плотность 90 кг/м3, толщиной 150 мм; - наружные стены отапливаемого подвала, заглубленные в грунт, не утепляются - утепление кровли (перекрытия над третьим и четвертым этажом) минеральный утеплитель, плотность 115/160 кг/м3. толщиной 200 мм в 2 слоя - утепление стен тамбура минеральным утеплителем толщиной 100 мм, плотностью 80-125 кг/м3; -утепление потолка тамбура минераловатным утеплителем 130кг/м3толщиной 200мм в 2 слоя с последующим оштукатуриванием - утепление парапетов утепленных покрытий на высоту минимум 500 мм, - замена оконных блоков в ПВХ профиле с двухкамерным стеклопакетом с мягким селективным покрытием.Приведенное сопротивление теплопередаче оконного блока из ПВХ профилей с двухкамерным стеклопакетом с сопротивлением теплопередаче расчетное R_{Ro} 0,618 (м2 ·°C)/Вт;					
Изм.	Кол.уч.	Лист	№док.	Подп.	Дата	2024-00375-00-0-AP.TЧ		Лист
								13

- утепление чердачного перекрытия минераловатными плитами плотностью 115/160 толщиной 200мм в 2 слоя с устройством цп стяжки 50мм

- утепление стен холодного чердака на высоту минимум 500 мм

г) Описание и обоснование решений по отделке помещений основного, вспомогательного, обслуживающего и технического назначения

Взам. инв. №	Предусматривается ремонт фасада по сертифицированной системе «Мокрый фасад» ТН-ФАСАД с оштукатуриванием тонким штукатурным слоем и окраской, фасады гладкие. Внешний облик здания не изменяется и соответствует функциональному назначению здания: общеобразовательная организация, школа. Решения интерьеров и выбор отделочных материалов обусловлены функциональным назначением помещений, организационной структурой здания и полностью удовлетворяет требования в части пожарной безопасности.																					
	Отделка интерьеров проектируемых зданий выполнена в строгом соответствии с едиными требованиями к зонированию, наружной и внутренней отделке школ Москвы Стандарт «МОСКОВСКАЯ ШКОЛА. Модернизация объектов образования». В отделке интерьеров преобладают светлые оттенки отделки и мягкие цветовые переходы.																					
Подп. и дата																						
Инв. № подл.	г) Описание и обоснование решений по отделке помещений основного, вспомогательного, обслуживающего и технического назначения																					
	<table border="1"> <tr> <td></td> <td></td> <td></td> <td></td> <td></td> <td></td> </tr> <tr> <td></td> <td></td> <td></td> <td></td> <td></td> <td></td> </tr> <tr> <td>Изм.</td> <td>Кол.уч.</td> <td>Лист</td> <td>№док.</td> <td>Подп.</td> <td>Дата</td> </tr> </table>																	Изм.	Кол.уч.	Лист	№док.	Подп.
Изм.	Кол.уч.	Лист	№док.	Подп.	Дата																	
2024-00375-00-0-AP.TЧ					Лист 14																	

Предусмотрена полная внутренняя отделка помещений основного, вспомогательного, обслуживающего и технического назначения в соответствии с заданием на проектирование, функциональным назначениям и требованиям СП 2.4. 3648-20.

Отделка полов:

Венткамеры, ИТП/Водомерный узел, электрощитовые (цокольный этаж), помещения пищеблока (Пл-2.2) –

керамогранитная плитка Цвет: "под бетон", Поверхность: матовая
Способ обработки: ректифицированная, Коэффициент противоскольжения: не ниже R9,
Формат: 600х600 мм, Толщина: 9 мм

Вестибюль, коридоры, коридор медблока, (цокольный этаж)(Пл-1) –
керамогранит крупноформатный Цвет: "под бетон", Поверхность: матовая, Способ
обработки: ректифицированная, Коэффициент противоскольжения: не ниже R9

Укладка: со смещением на 1/2 по длиной стороне, Формат: 1195х600 мм, Толщина: 9 мм;

Обеденный зал (1 этаж) –
керамогранит, Цвет: "под бетон", Поверхность: матовая
Способ обработки: ректифицированная, Коэффициент противоскольжения: не ниже R9
Формат: 600х600 мм, Толщина: 9 мм; плинтус керамогранитный заваляцованный (RAL в
цвет пола), высота 95 мм;

Лестничных клетки (Пл-2.3)-
керамогранит, Цвет: "под камень". Поверхность: матовая
Способ обработки: ректифицированная, Коэффициент противоскольжения: не ниже R9
Площадки- 600х600х9 мм, ступень заваляцованная с противоскользящей насечкой
600х300х9 мм, подступенок 600х145х9 мм, плинтус керамогранитный заваляцованный (RAL в
цвет пола) высота 95 мм;

Специализированные учебные кабинеты, фонд хранения библиотеки (Пл-5) –
дизайн - плитка ПВХ (текстура серый бетон с отпечатками, иловый бетон, темно-серый
бетон, коэффициент противоскольжения R10). Тип укладки: "зиг-заг" 500х500х2,55 мм с
защитным слоем не ниже 0,8 мм; плинтус гибкий из ПВХ, высота 100 мм. Для устройства
подиума в кабинетах, высотой 200 мм, предусматривается фальшпол из плит 600х600х30 мм из
сульфата кальция на опорах, толщиной 187,45 мм, с покрытием дизайн - плиткой ПВХ
500х500х2,55 мм;

Актового зала плитка ПВХ с показателями пожарной опасности не выше В2,Д2,Т2,РП1

Учебные кабинеты, гардеробная комната (для учителей), кабинет для индивидуальных
занятий, серверные, кроссовые, раздевальные, универсальные учебные кабинеты, артистические,
снарядные, кладовая инвентаря, (Пл-5.2)–

дизайн - плитка ПВХ (текстура натуральный бетон, коэффициентпротивоскольжения
R10) 500х500х2,55 мм с защитным слоем не ниже 0,8 мм; плинтус гибкий из ПВХ, высота 100
мм. Для устройства подиума в кабинетах, высотой 200 мм, предусматривается фальшпол из плит
600х600х30 мм из сульфата кальция на опорах, толщиной 187,45 мм, с покрытием дизайн -
плиткой ПВХ 500х500х2,55 мм;

Коридоры (2-4 этаж) (Пл5.2) –
дизайн-плитка ПВХ (текстура натуральный бетон, коэффициент противоскольжения R10)
500х500х2,55 мм с защитным слоем не ниже 0,8 мм; плинтус гибкий из ПВХ, высота 100 мм с
показателями пожарной опасности не выше В2,Д3,Т2,РП2 ;

Санузлы, ПУИ (1-4 этаж) (Пл-2)

Инв. № подл.	Подп. и дата	Взам. инв. №	учебные кабинеты, гардеробная комната (для учителей), кабинет для индивидуальных занятий, серверные, кроссовые, раздевальные, универсальные учебные кабинеты, артистические, снарядные, кладовая инвентаря, (Пл-5.2)– дизайн - плитка ПВХ (текстура натуральный бетон, коэффициентпротивоскольжения R10) 500х500х2,55 мм с защитным слоем не ниже 0,8 мм; плинтус гибкий из ПВХ, высота 100 мм. Для устройства подиума в кабинетах, высотой 200 мм, предусматривается фальшпол из плит 600х600х30 мм из сульфата кальция на опорах, толщиной 187,45 мм, с покрытием дизайн - плиткой ПВХ 500х500х2,55 мм; Коридоры (2-4 этаж) (Пл5.2) – дизайн-плитка ПВХ (текстура натуральный бетон, коэффициент противоскольжения R10) 500х500х2,55 мм с защитным слоем не ниже 0,8 мм; плинтус гибкий из ПВХ, высота 100 мм с показателями пожарной опасности не выше В2,Д3,Т2,РП2 ; Санузлы, ПУИ (1-4 этаж) (Пл-2)					
			2024-00375-00-0-AP.T4					
			Изм.	Кол.уч.	Лист	№ док.	Подп.	Дата

Лист 15

– керамогранит крупноформатный Цвет: "под бетон", Поверхность: матовая
Способ обработки: ректифицированная, Коэффициент противоскольжения: не ниже R9
Формат: 600х600 мм, Толщина: 9 мм

Кабинет для учителей, административный кабинет, комната инструктора(Пл-5.1)
- дизайн- плитка ПВХ (текстура дерево, коэффициент противоскольжения R10)
1000х200х2,55 мм с защитным слоем не ниже 0,8 мм; плинтус гибкий из ПВХ, высота 100 мм с показателями пожарной опасности не выше В2,Д2,Т2,РП1;

Душевые, тамбур (пл-2.1)
– керамогранит,Цвет: "под бетон",Поверхность: матовая
Способ обработки: ректифицированная,Коэффициент противоскольжения: не ниже R10BC
Формат: 600х600 мм,Толщина: 9 мм плинтус керамогранитный, (RAL в цвет пола), высота 95 мм;

Процедурный (прививочный) кабинет, кабинет врача (Пл-4)–
линолеум толщ. 2 мм Спортивные залы – спортивный паркет 300х1800х20 мм, с показателями пожарной опасности не выше В2,Д2,Т2,РП1 плинтус вентилируемый.

Спортзал/гимнастический зал (Пл-6):
Паркетная доска 14мм Порода дерева: дуб, 5 слоев лака.
Размер (ДхШ): 2266*188мм, Толщина верхнего слоя: 14мм,, Ценный слой дуба: 3,5 - 4мм,
Ударопоглощение: 60%, ертикальный отскок мяча: 88%, Скольжение: 86

Отделка стен:

Венткамеры, ИТП/Водомерный узел, помещения пищеблока – окраска стен акриловой водно-дисперсионной моющейся краской RAL 9010 (влагостойкая, с содержанием противогрибковых добавок, устойчивая к влажной обработке с применением моющих и дезинфицирующих средств);

Лестничные клетки - окраска стен силикатной антивандальной краской группы горючести НГ;

Коридоры – окраска стен акриловой водно-дисперсионной моющейся краской краска с показателями пожарной опасности не выше Г1,В1,Д2,Т2;

Обеденный зал - окраска стен акриловой водно-дисперсионной моющейся краской, плитка керамическая 200х500х10; 285х85х10; 400х1200х10 мм (цвет бежевый, белый, под дерево) с показателями пожарной опасности не выше Г1,В1,Д2,Т2;

Актальный зал - окраска стен акриловой водно-дисперсионной моющейся краской, с показателями пожарной опасности не выше Г1,В1,Д2,Т2;

Учебные классы, лаборантские – окраска стен акриловой водно-дисперсионной моющейся краской, плитка керамическая 200х85х9,2 мм;

Умывальные - плитка керамическая 285х85х9 мм (цвет белый);

Санузлы, ПУИ – керамогранит крупноформатный 600х600х9 мм, мозаика стеклянная 23х23

Душевые – керамогранит крупноформатный 1195х600х9 мм, мозаика стеклянная 23х23

Помещения пищеблока – плитка керамическая 200х200х6,9 мм

Инв. № подл.	Подп. и дата	Взам. инв. №					2024-00375-00-0-АР.ТЧ		Лист
									16
			Изм.	Кол.уч.	Лист	№ док.	Подп.	Дата	

Технические помещения, кроссовые— простая окраска стен акриловой водно-дисперсионной моющейся краской RAL 9010;

Спортивные залы – окраска стен акриловой водно-дисперсионной моющейся краской (RAL 9010, RAL 9002) с показателями пожарной опасности не выше Г1,В1,Д2,Т2, стеновые протекторы.

Отделка потолков:

Венткамеры, ИТП/Водомерный узел, помещения пищеблока (цокольный этаж)
- окраска матовой акриловой водно-дисперсионной моющейся (RAL 9003, устойчивая к влажной обработке с применением моющих и дезинфицирующих средств);

Коридоры, обеденный зал (1 этаж)
– окраска потолка и коммуникаций (RAL 9003), акустические панели подвесные из минерального волокна с показателями пожарной опасности не выше Г1,В1,Д2,Т2. Каркасом подвесных акустических панелей служат металлические тросики. Данная конструкция позволяет беспрепятственно снять подвешенные элементы подвесного потолка, обеспечивая доступ в запотолочное пространство.

Помещения пищеблока (1 этаж) –
окраска потолка и коммуникаций (RAL 9003)

Коридоры (2-4 этаж) –
окраска потолка и коммуникаций (RAL 9011) с показателями пожарной опасности не выше Г1,В1,Д2,Т2, акустические панели подвесные из минерального волокна. Каркасом подвесных акустических панелей служат металлические тросики. Данная конструкция позволяет беспрепятственно снять подвешенные элементы подвесного потолка, обеспечивая доступ в запотолочное пространство.

Учебные классы, лаборантские –
кассетный акустический потолок 1200х600 мм;

Санузлы–
грильято 50х50 мм;

Вестибюль
грильято 100х100 мм группы горючести НГ

тамбур –
грильято 100х100 мм;

Технические помещения, кроссовые –
окраска потолка и коммуникаций (RAL 9003);

Лестничные клетки –
окраска потолка и коммуникаций силикатной краской (RAL9003) группы горючести НГ;

Спортивные залы – о
краска потолка и коммуникаций (RAL 9003) с показателями пожарной опасности не выше Г1,В1,Д2,Т2

Инв. № подл.	Взам. инв. №	Подп. и дата	тамбур – грильято 100х100 мм;					
			Технические помещения, кроссовые – окраска потолка и коммуникаций (RAL 9003);					
			Лестничные клетки – окраска потолка и коммуникаций силикатной краской (RAL9003) группы горючести НГ;					
			Спортивные залы – о краска потолка и коммуникаций (RAL 9003) с показателями пожарной опасности не выше Г1,В1,Д2,Т2					
						2024-00375-00-0-AP.TЧ		Лист
								17
Изм.	Кол.уч.	Лист	№док.	Подп.	Дата			

Уста новку ОЗДС необходимо проводить при наличии документов, подтверждающих качество и безопасность продукции (товаров) в случаях необходимости такого документа в соответствии с правовыми актами Таможенного союза и законодательства Российской Федерации.

31) Сведения о номенклатуре, компоновке и площадях основных производственных, экспериментальных, сборочных, ремонтных и иных цехов, а также лабораторий, складских и административно-бытовых помещений, иных помещений вспомогательного и обслуживающего назначения - для объектов производственного назначения.


Объект не является производственным. Данный пункт не разрабатывается

32) Обоснование номенклатуры, компоновки и площадей помещений основного, вспомогательного, обслуживающего назначения и технического назначения - для объектов непроизводственного назначения.


Номенклатура, компоновка и площади здания обусловлены функциональным назначением здания. Планировочные решения по школе соответствуют действующим правилам и нормам СП 118.13330.2022 «Общественные здания и сооружения»; ТСН 31- 306- 2004 г. Москвы «Общеобразовательные учреждения»; СП 251.1325800.2016 «Здания общеобразовательных организаций. Правила проектирования»;

Проведение работ по капитальному ремонту здания школы предусматривает сохранение существующей функциональной схемы размещения помещений.

Инв. № подл.	Подп. и дата	Взам. инв. №							2024-00375-00-0-AP.TЧ		Лист
											20
Изм.	Кол.уч.	Лист	№док.	Подп.	Дата						

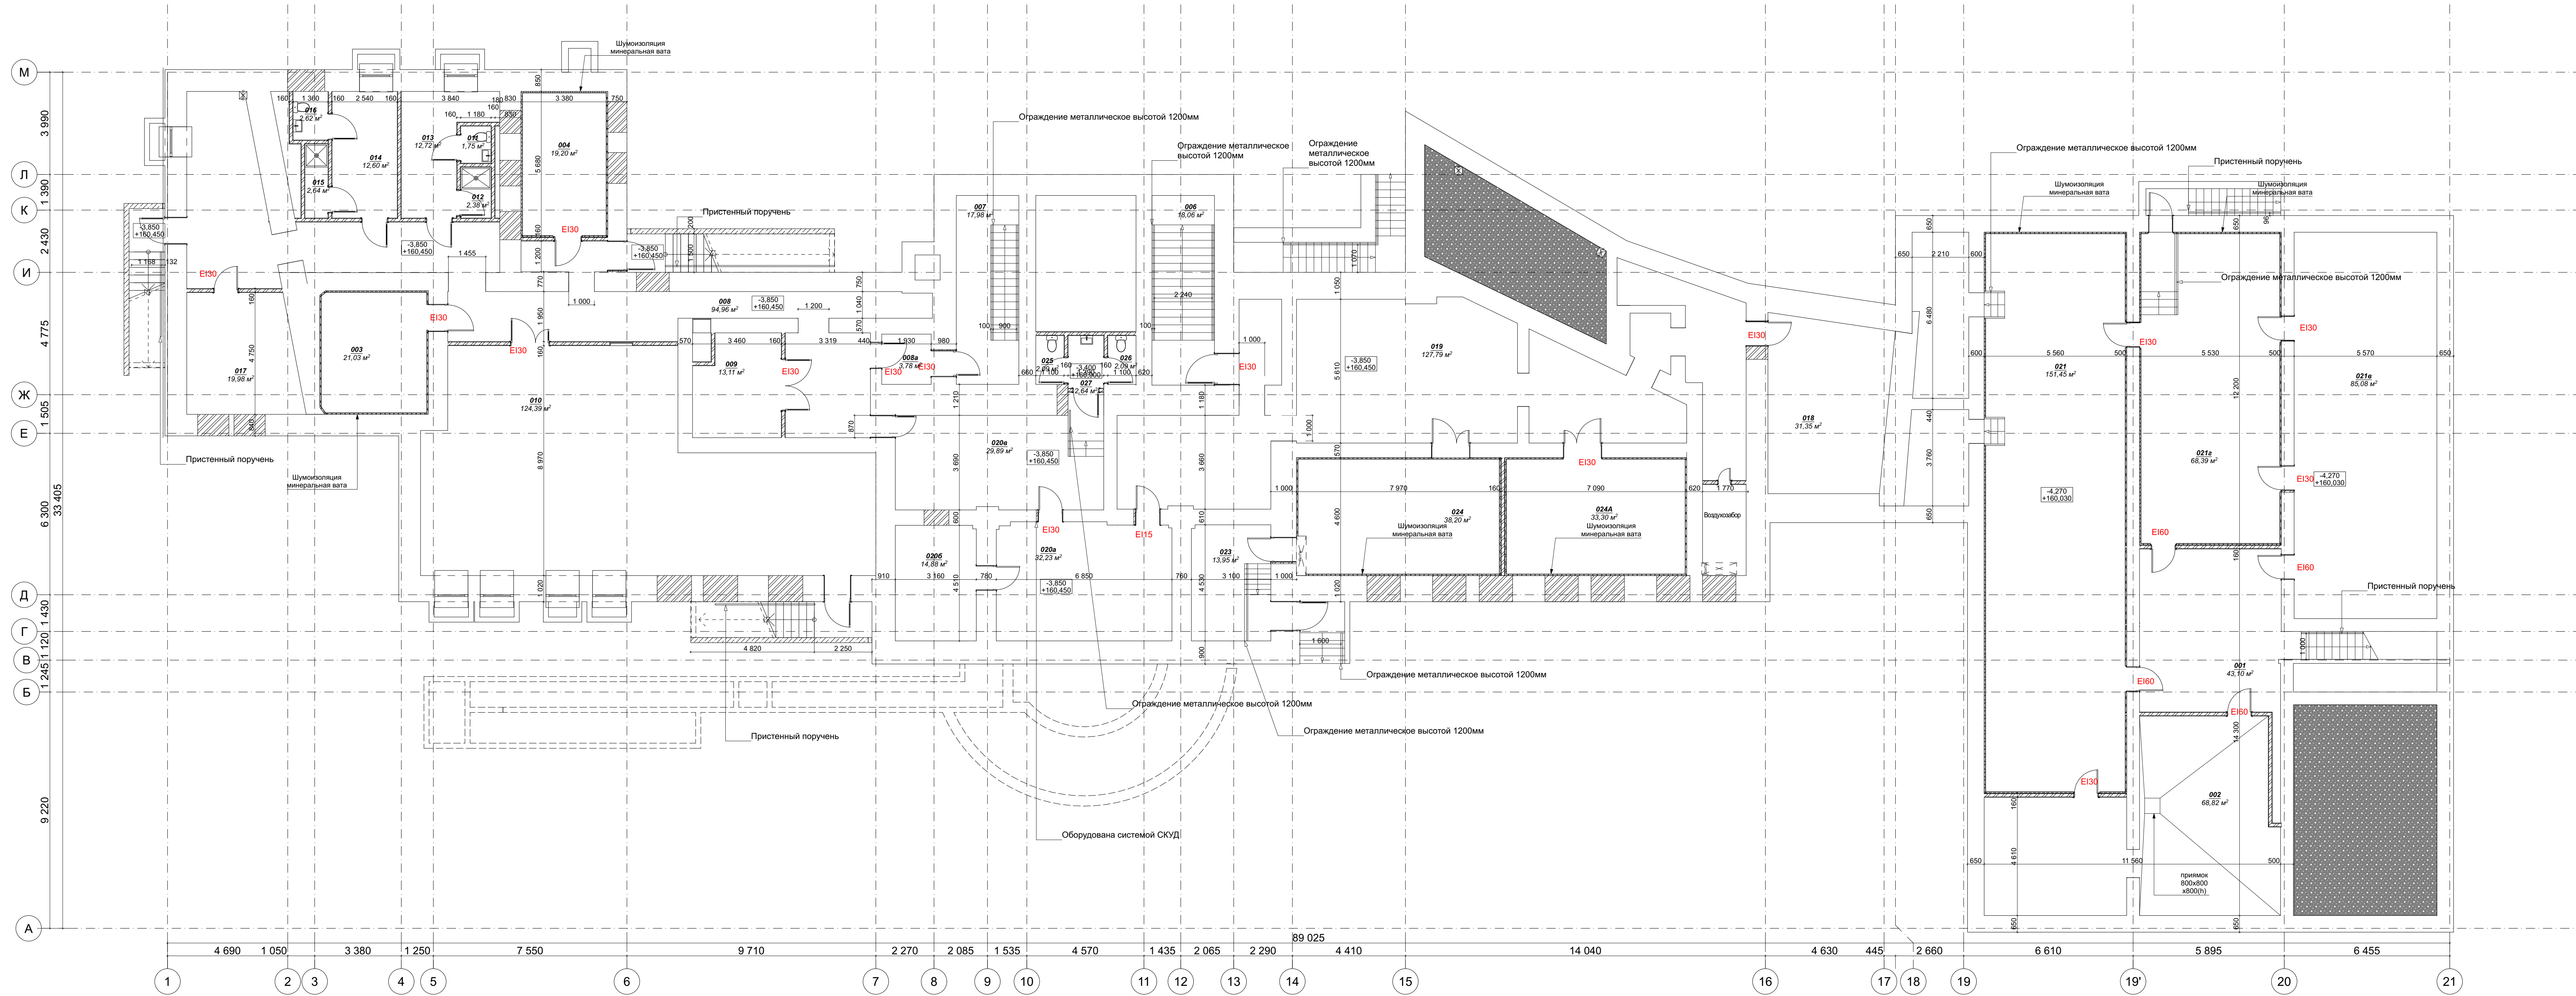


Экспликация помещений подвального этажа			
Номер помеще-ния	Наименование	Площадь, м2	Кат. пом.еще-ния
001	Лестничная клетка	43,10	
002	ИТП	68,82	B4
003	Венткамера	21,03	B4
004	Венткамера	19,20	B4
006	Лестничная клетка тип Л1	18,06	
007	Технологическая лестница	17,98	
008	Коридор	94,96	
008a	Тамбур-шлюз	3,78	
009	Складская	13,11	B3
010	Зал ЛБК	124,39	
011	Санузел	1,75	
012	Душевая	2,38	
013	Раздевальня (не более 5 чел)	12,72	
014	Раздевальня (не более 5 чел)	12,60	
015	Душевая	2,64	
016	Санузел	2,62	
017	Электрощитовая	19,98	B3
018	Подсобное помещение	31,35	B3
019	Коридор	127,79	
020a	Коридор	32,23	
020b	Помещение для прокладки коммуникаций	14,88	B4
020в	Коридор	29,89	
021	Венткамера	151,45	B4
021a	Помещение для прокладки коммуникаций	85,08	B4
021r	Венткамера	68,39	B3
023	Узел ввода	13,95	Д
024	Насосная	38,20	Д
024A	Венткамера	33,30	B4
025	Санузел	2,09	
026	Санузел	2,09	
027	Умывальная	2,64	
		1112,45 м²	

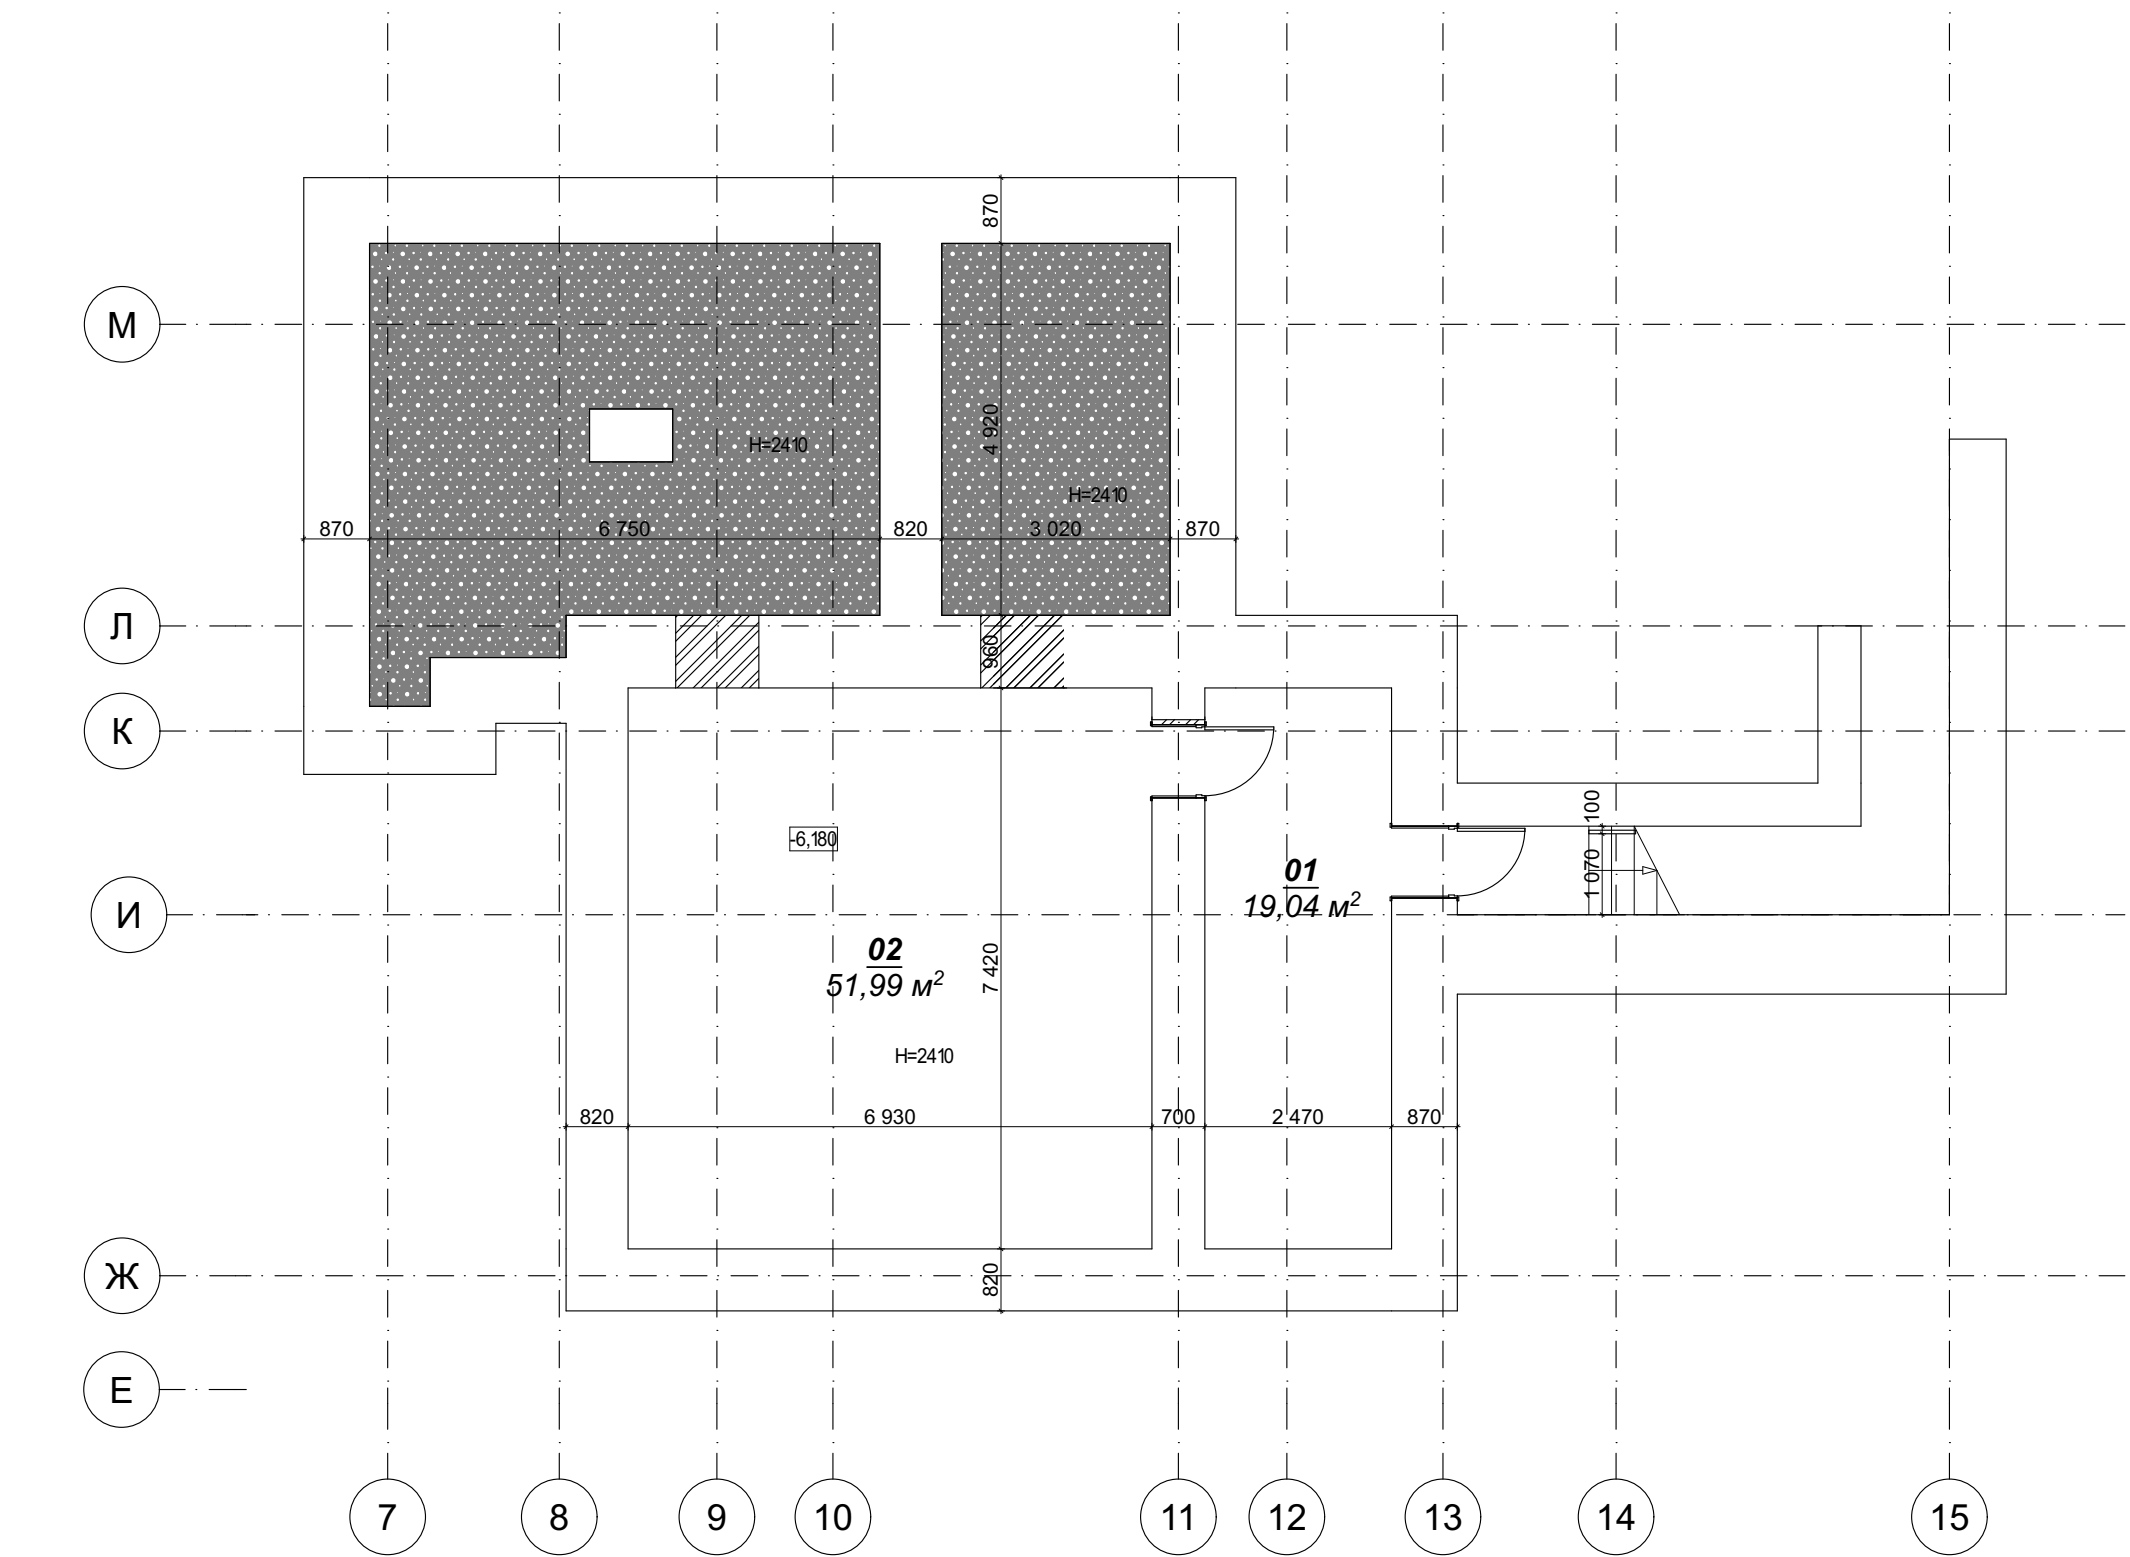


Экспликация помещений подполья			
Номер помеще-ния	Наименование	Площадь, м2	Кат. пом.еще-ния
01	Тамбур	19,04	
02	Помещение для прокладки коммуникаций	51,99	B4
		71,03 м²	

Условные обозначения			
	Существующие стены		
	Восстановление кирпичной кладки		
	Утеплитель минераловатный		
	Замена перекрытий из плитного железобетона, толщина 120мм		
	Замена перекрытий из железобетона, толщина 120мм, плотность 2400		
	Замена обшивки на ГВЛ		
	Замена внутренних перегородок		
	Номер помещения		
	Отметка чистого пола		


						2024-00375-00-0-AP		
						Здания Государственного бюджетного общеобразовательного учреждения города Москвы "Школа № 1574", расположенного по адресу: Москва, пер. Староименный, д. 5		
Имя	Кол-во	Лист	Издок	Подп.	Дата			
Иванов	1	1	1	И.И.	11.25			
Григорьев	1	1	1	Г.Г.	11.25			
						Капитальный ремонт		
						Страница	Лист	Листов
						1	1	
И.И. Кондр.	1	1	1	И.И.	11.25	План подвала; план подполья		
						 МОСЖИЛНИИПРОЕКТ		

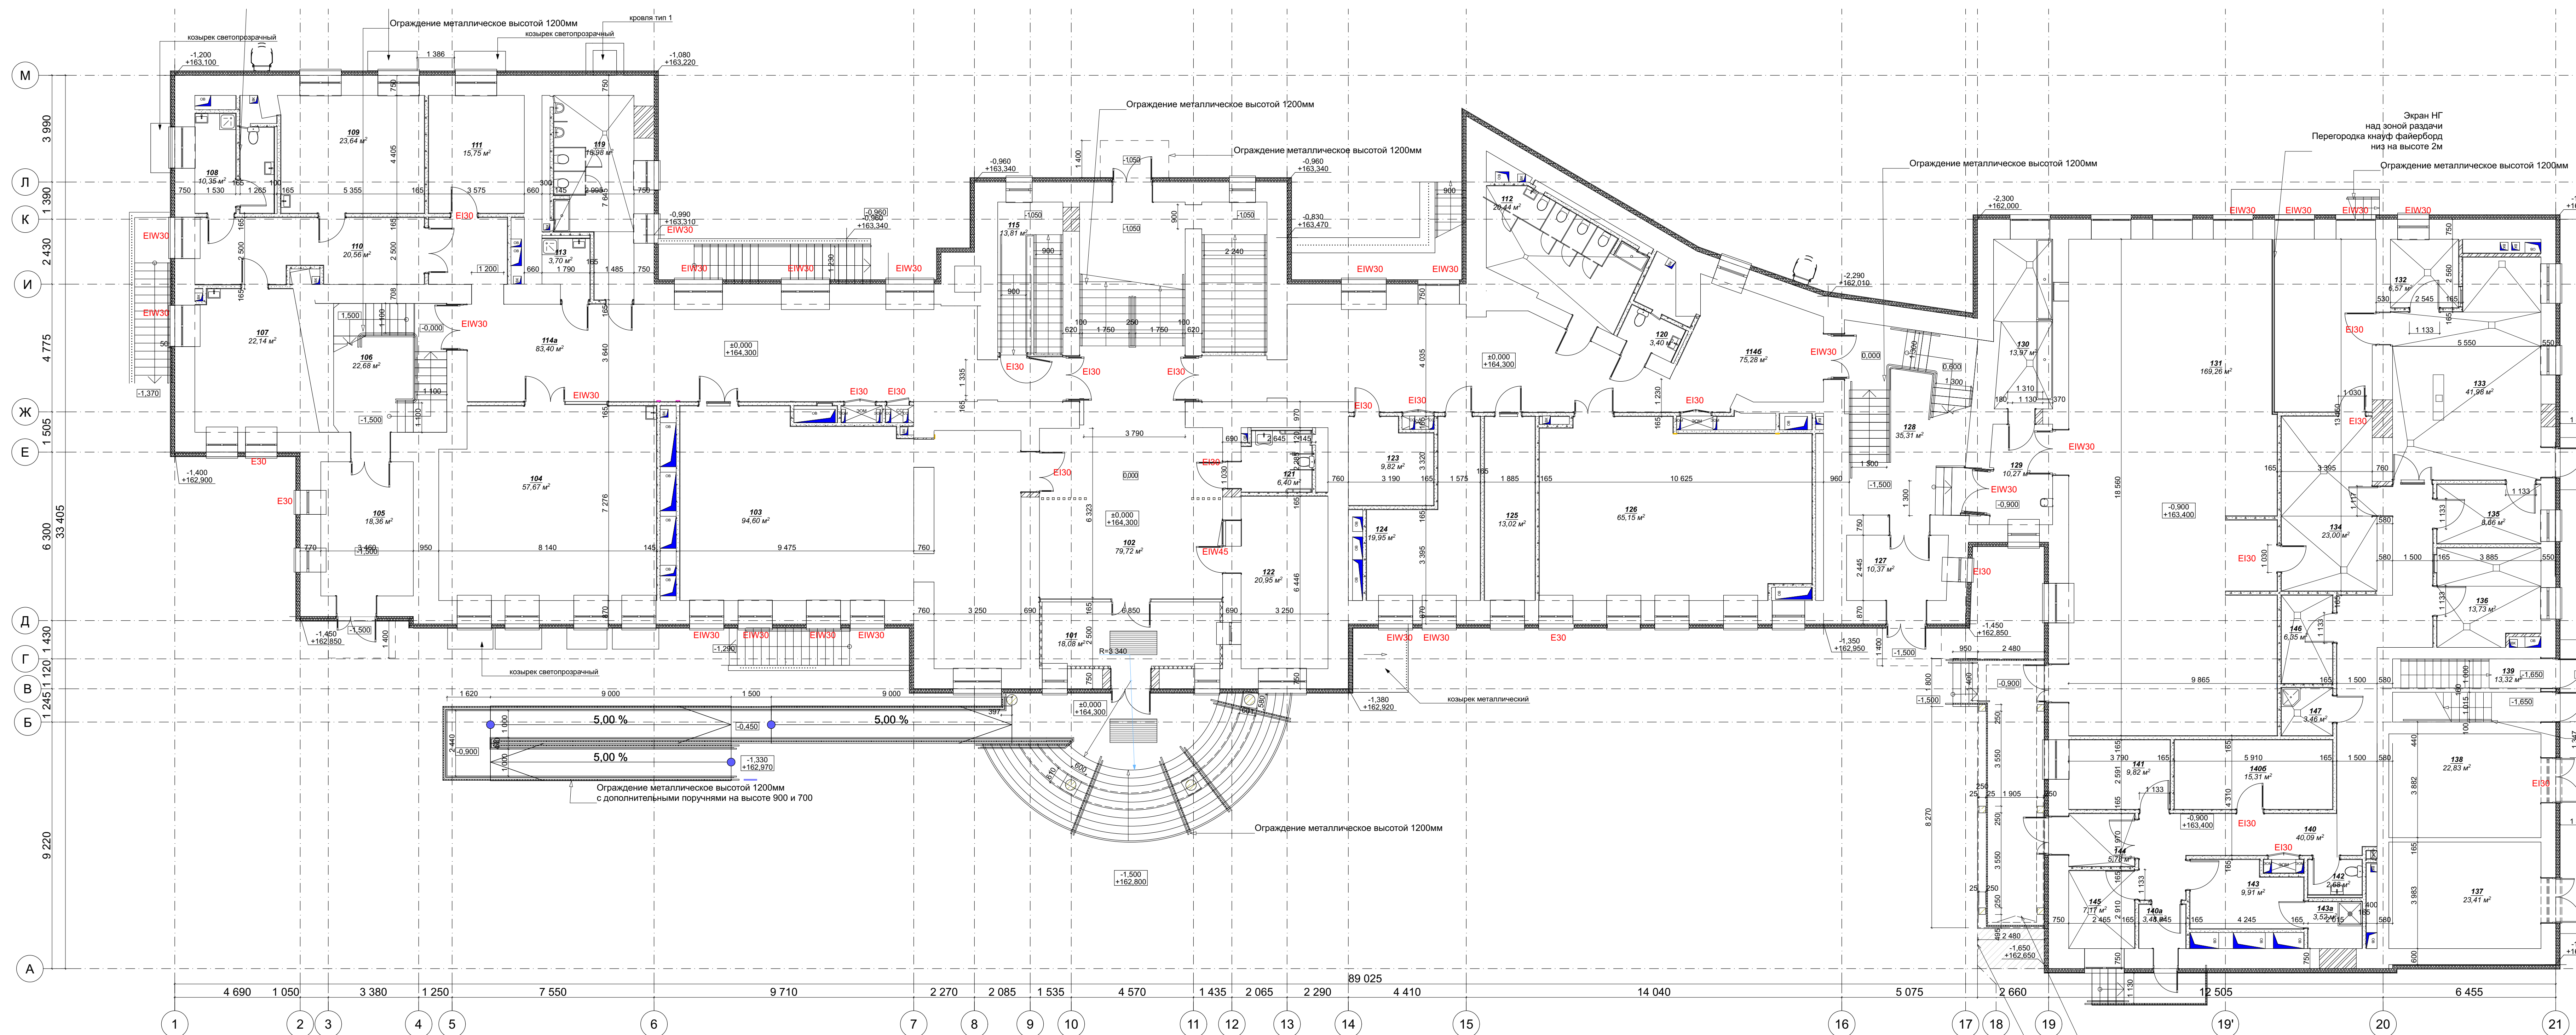


Экспликация помещений 1 этажа			
Номер помещения	Наименование	Площадь, м2	Кат. помещ.
101	Тамбур	18,08	
102	Вестиболь	79,72	
103	Гардеробная для обучающихся	94,60	
104	Учебный кабинет	57,67	
105	Тамбур	18,36	
106	Лестничная клетка тип Н2	22,68	
107	Процедурный (прививочный) кабинет	22,14	
108	Место для приготовления дезинфицирующих растворов и хранения уборочного инвентаря	10,35	B4
109	Кабинет врача	23,64	
110	Зона ожидания посетителей	20,56	
111	Кладовая	15,75	B3
112	Санузел для девочек с комнатой личной гигиены	20,44	
113	ПУИ	3,70	B4
114a	Коридор	83,40	
114b	Коридор	75,28	
115	Технологическая лестница	13,81	
119	Санузел для мальчиков	18,98	
120	Санузел для персонала	3,40	
121	Санузел для МГН	6,40	
122	Комната охраны	20,95	
123	Кроссовая	9,82	B4
124	Административный кабинет тип 1	19,95	
125	Гардеробная комната для учителей	13,02	
126	Учебный кабинет	65,15	
127	Тамбур	10,37	
128	Лестничная клетка тип Л1	35,31	
129	Коридор	10,27	
130	Умывальная	13,97	
131	Обеденный зал	169,26	
132	Холодный цех	6,57	B4
133	Горячий цех	41,98	B3
134	Моечная столовой посуды	23,00	B4
135	Моечная кухонной посуды	8,66	B4
136	Догоготовочный цех	13,73	B3
137	Техническое помещение (электрошитовая)	23,41	B3
138	Техническое помещение (электрошитовая)	22,83	B3
139	Лестничная клетка тип Л1	13,32	
140	Коридор	40,09	
140a	Тамбур	3,48	
140b	помещение холодильного оборудования	15,31	B3
141	Кладовая сухих продуктов	9,82	B4
142	Санузел	2,68	
143	Помещение для персонала	9,91	
143a	Душ	3,52	
144	Загрузочный цех	5,78	B4
145	Кладовая и моечная оборотной тары	7,17	B4
146	Помещение для временного хранения пищевых отходов	6,35	B4
147	ПУИ	3,46	B4
		1 238,10 м²	

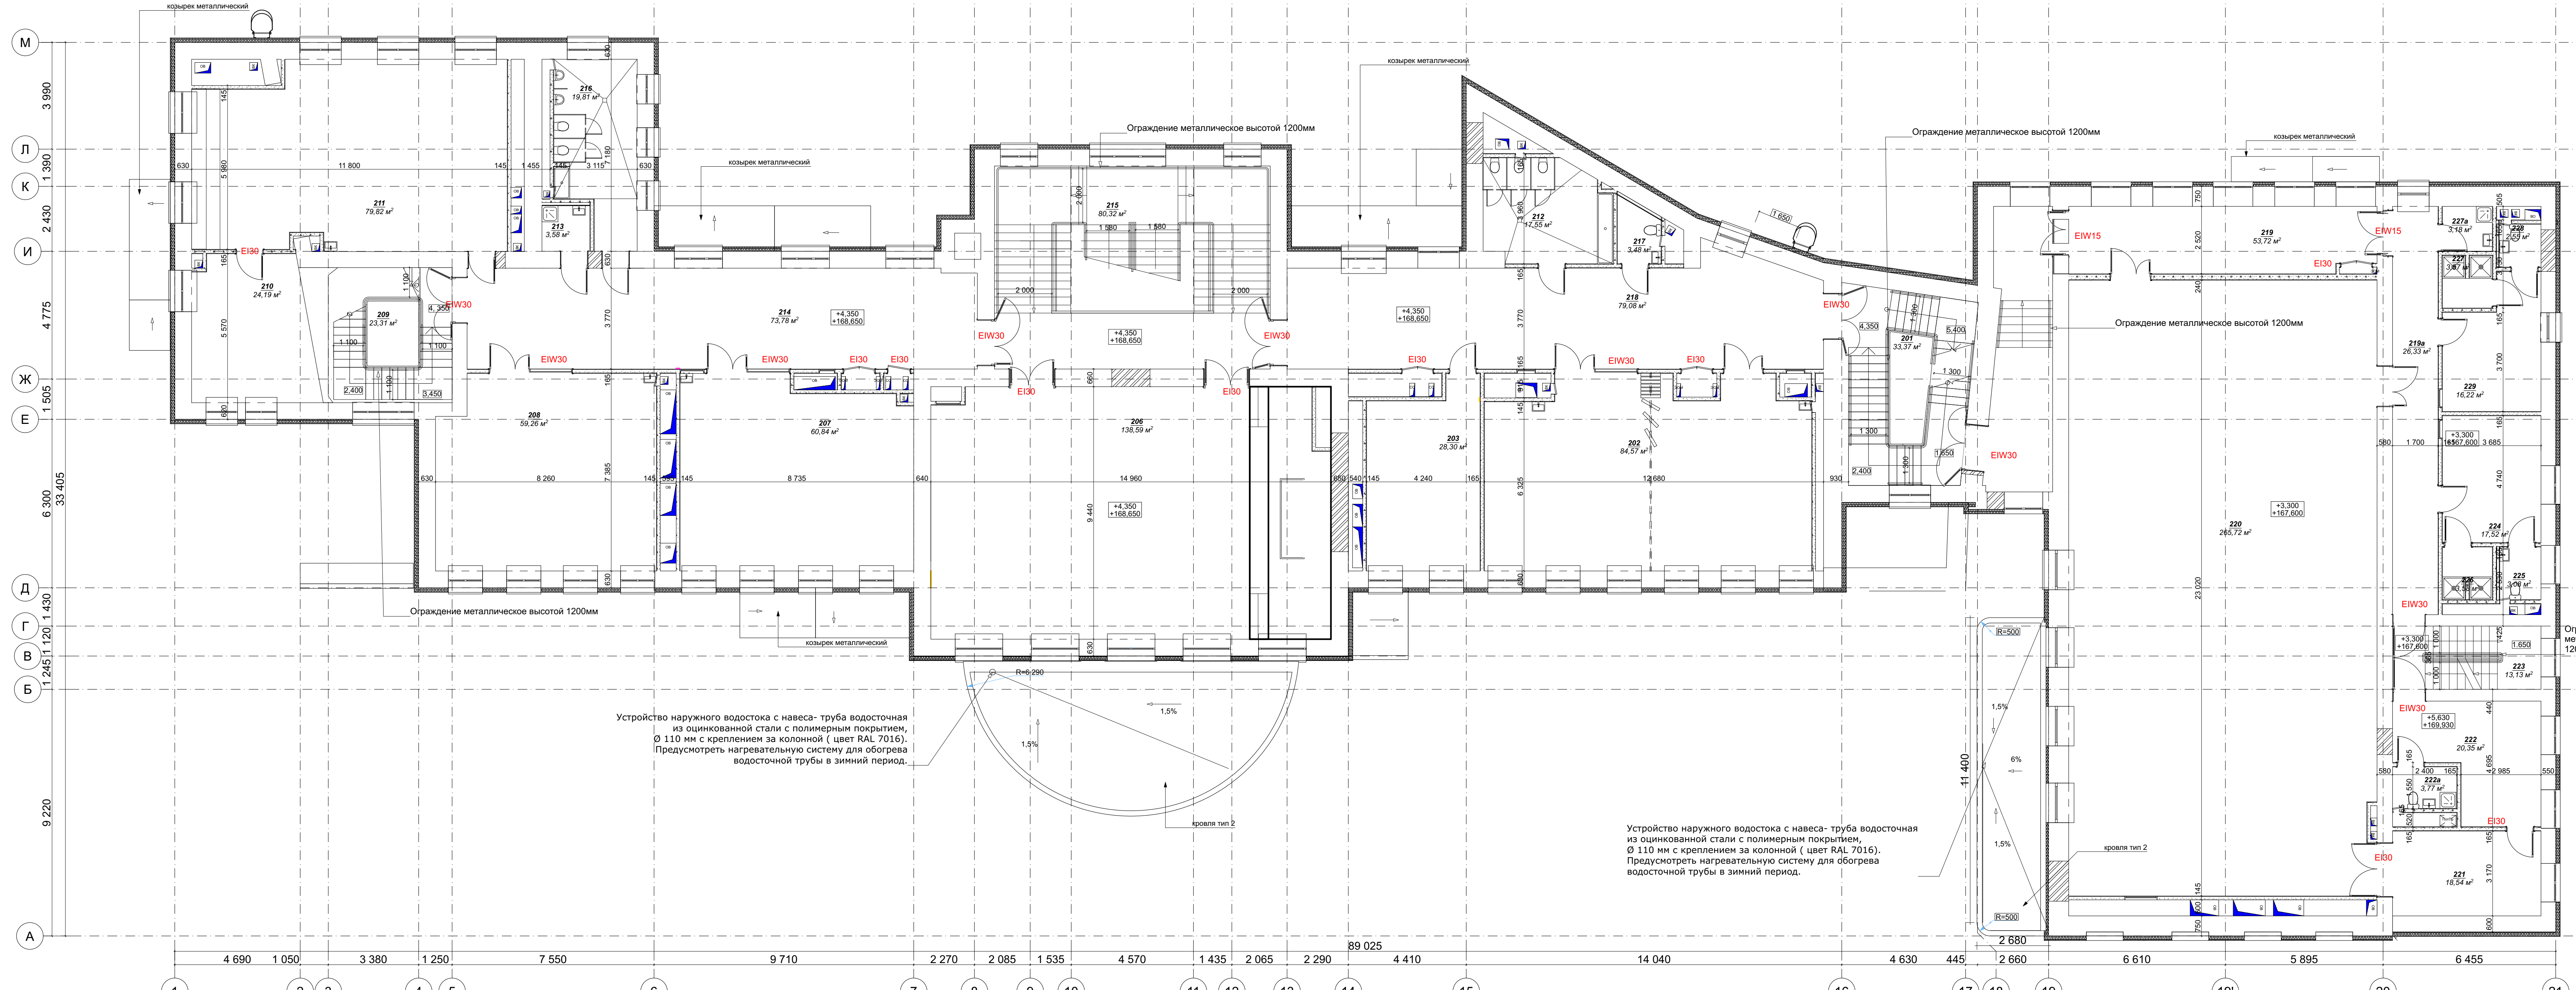

Экспликация помещений 2 этажа			
Номер помещения	Наименование	Площадь, м2	Кат. помещ.
201	Лестничная клетка тип Л1	33,37	
202	Кабинет иностранного языка	84,57	
203	Рабочее пространство для учителей тип 2	28,30	
206	Актовый зал	138,59	
207	Учебный кабинет	60,84	
208	Учебный кабинет	59,26	
209	Лестничная клетка Л1	23,31	
210	Кладовая инвентаря творческой мастерской	24,19	B3
211	Кабинет ИЗО	79,82	
212	Санузел для девочек	17,55	
213	ПУИ	3,58	B4
214	Коридор	73,78	
215	Вестиболь	80,32	
216	Санузел для мальчиков	19,81	
217	Санузел для персонала	3,48	
218	Коридор	79,08	
219	Коридор	53,72	
219a	Коридор	26,33	
220	Спортивный зал	265,72	
221	Снарядная	18,54	B3
222	Комната инструктора	20,35	
222a	Душ с санузлом	3,77	
223	Лестничная клетка тип Л1	13,13	
224	Раздевальная для девочек	17,52	
225	Санузел	3,08	
226	Душевая	3,58	
227	Душевая	3,57	
227a	ПУИ	3,18	B4
228	Санузел	2,55	
229	Раздевальная для мальчиков	16,22	
		1 261,11 м²	

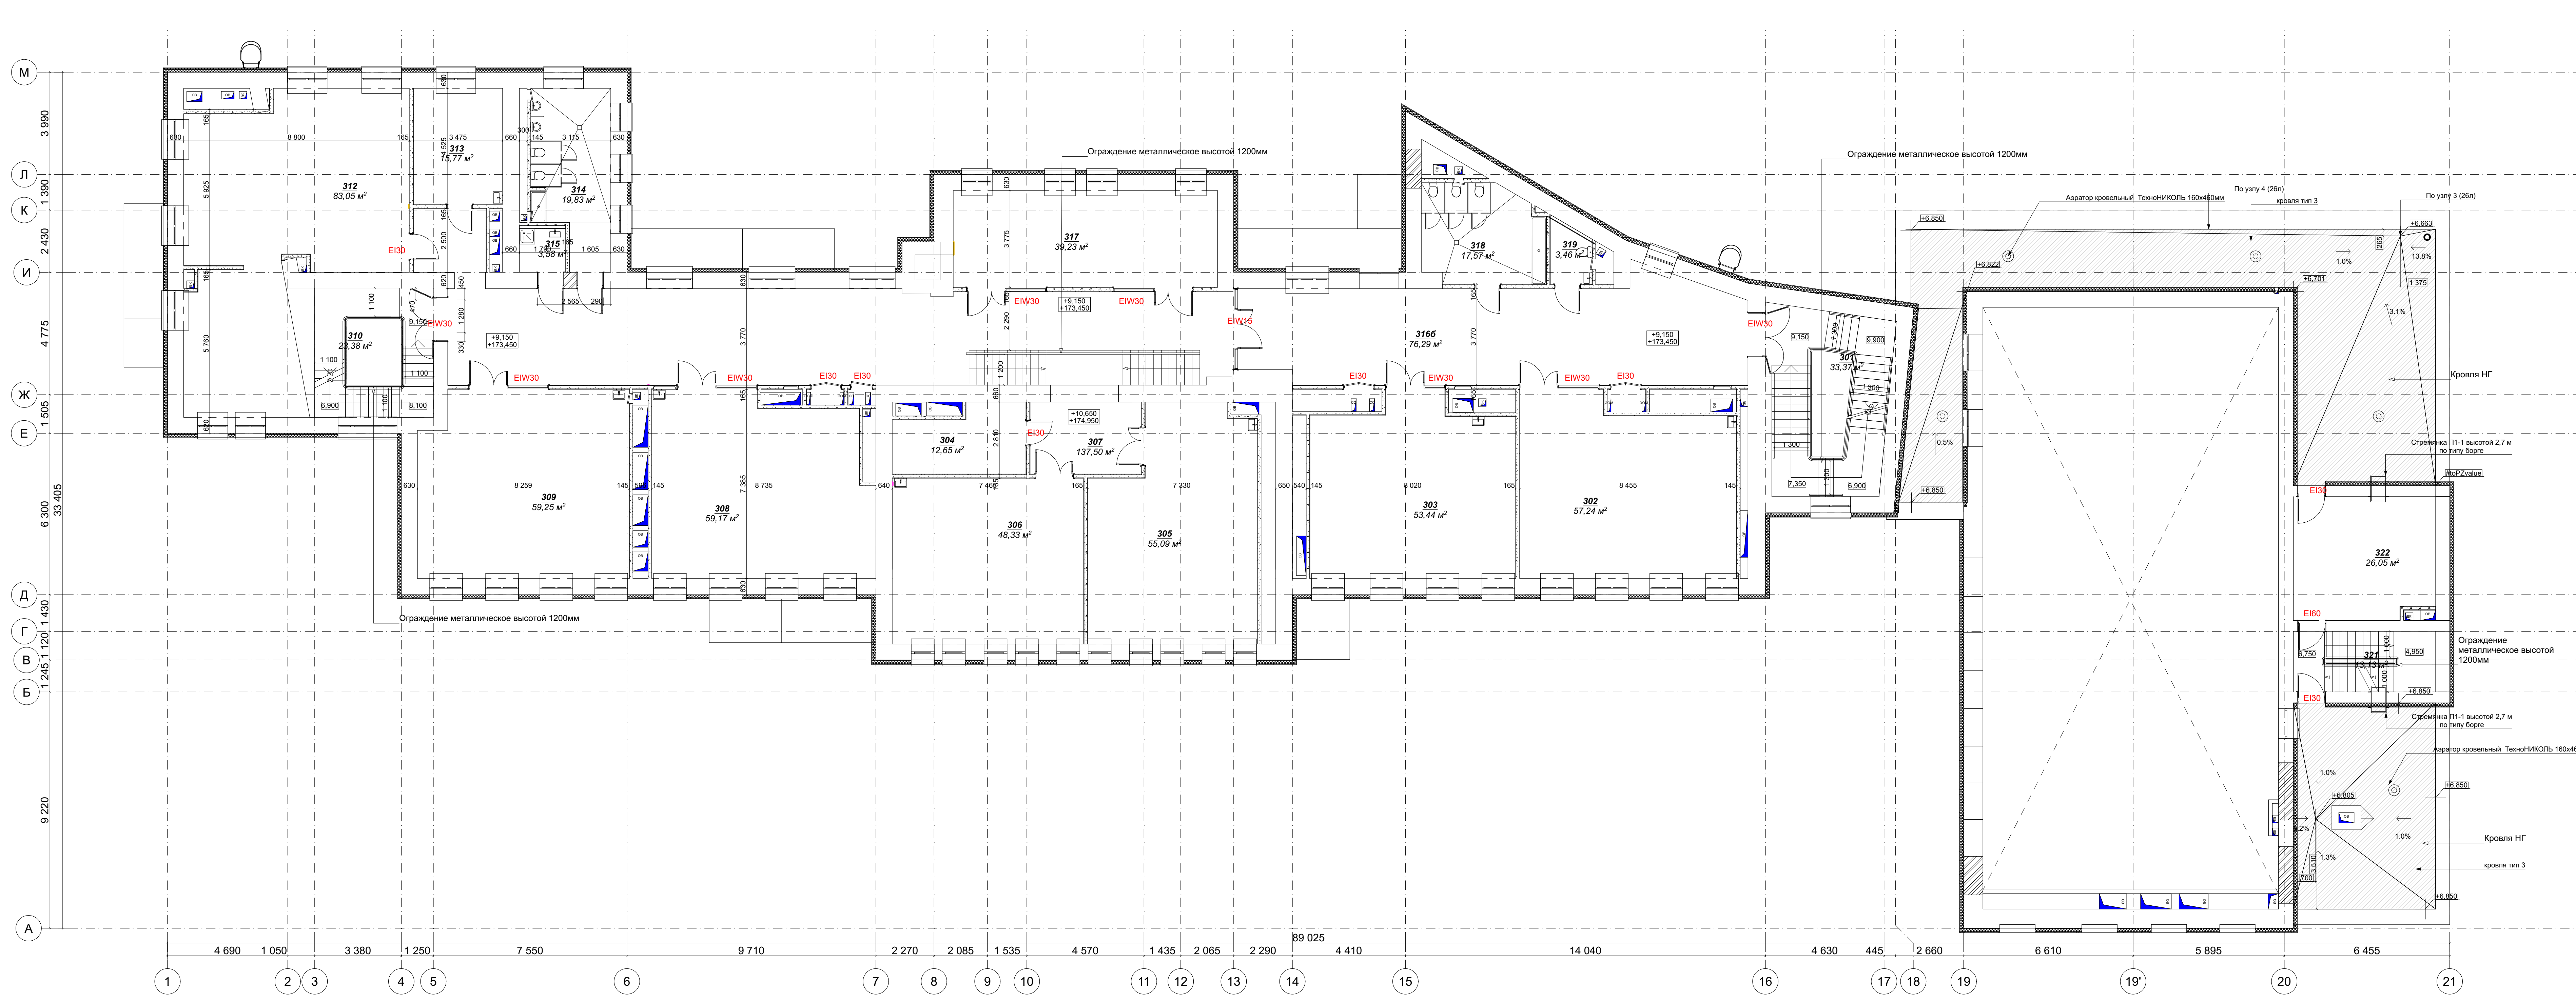

Экспликация помещений 3 этажа			
Номер помеще-ния	Наименование	Площадь, м2	Кат. пом.еще-ния
301	Лестничная клетка тип Л1	33,37	
302	Учебный кабинет	57,24	
303	Учебный кабинет	53,44	
304	Серверная	12,65	B3
305	Учебный кабинет	55,09	
306	Учебный кабинет	48,33	
307	Коридор	137,50	
308	Учебный кабинет	59,17	
309	Учебный кабинет	59,25	
310	Лестничная клетка тип Л2	23,38	
312	Библиотека	83,05	B3
313	Кабинет для индивидуальных занятий в т.ч. с учителем-логопедом	15,77	
314	Санузел для мальчиков	19,83	
315	ПУИ	3,58	B4
316	Коридор	76,29	
317	Кабинет иностранного языка	39,23	
318	Санузел для девочек	17,57	
319	Санузел для персонала	3,46	
321	Лестничная клетка тип Л1	13,13	
322	Тамбур	26,05	
		837,38 м²	

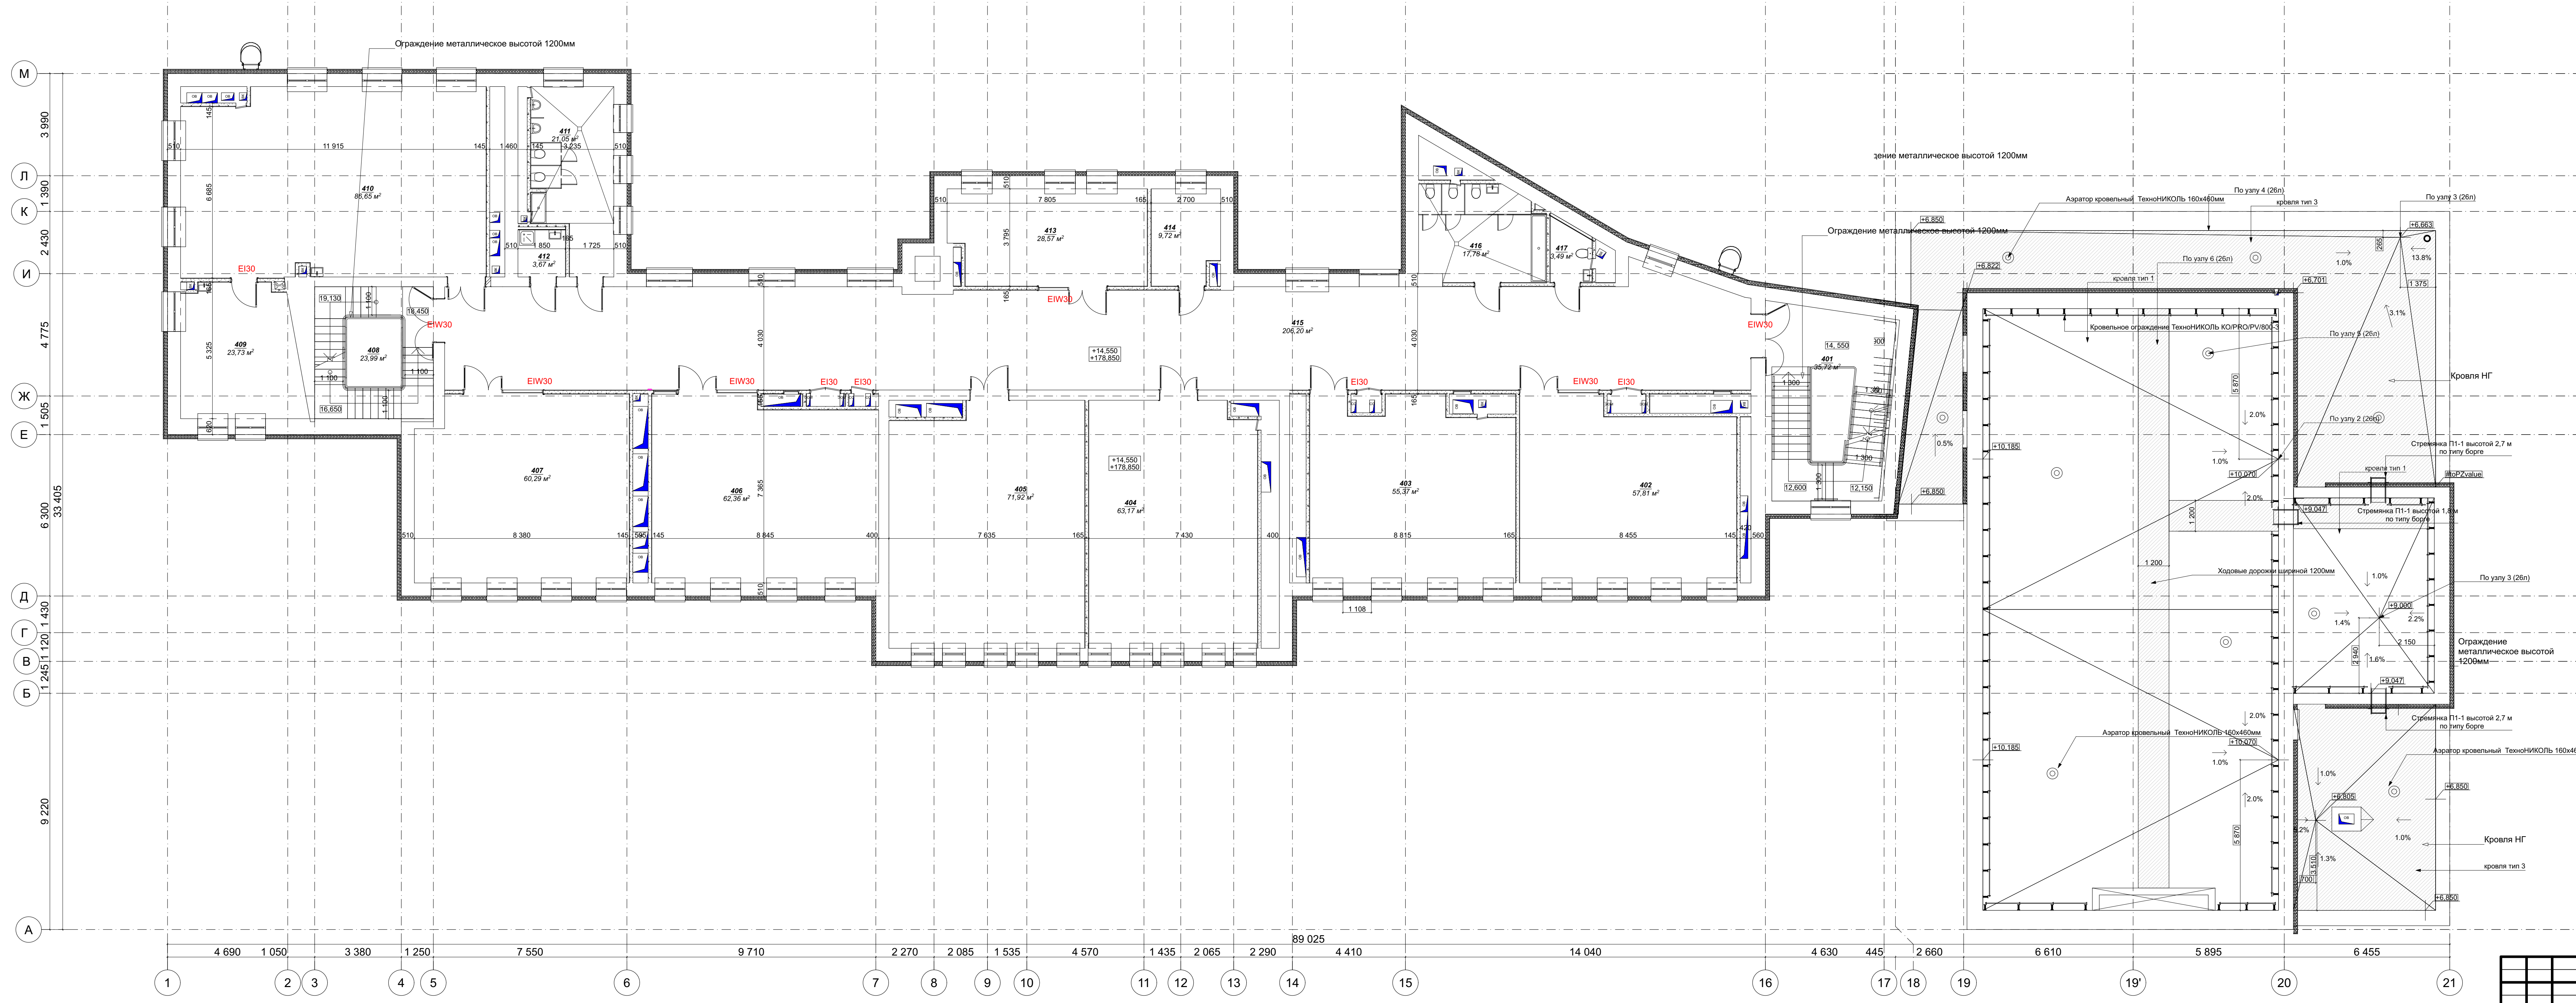


Экспликация помещений 4 этажа			
Номер помеще-ния	Наименование	Площадь, м2	Кат. пом.еще-ния
401	Лестничная клетка тип Л1	35,72	
402	Кабинет русского языка и литературы	57,81	
403	Кабинет русского языка и литературы	55,37	
404	Кабинет истории тип 1	63,17	
405	Кабинет математики	71,92	
406	Кабинет математики	62,36	
407	ОБЗР	60,29	
408	Лестничная клетка тип Л2	23,99	
409	Лаборантская кабинета биологии	23,73	B3
410	Учебные кабинеты для изучения естествознания: биологии/ЛИК	86,65	
411	Санузел для мальчиков	21,05	
412	ПУИ	3,67	B4
413	Административный кабинет тип 1	28,57	
414	Кабинет для индивидуальных занятий в т.ч. с педагогом-психологом	9,72	
415	Коридор	206,20	
416	Санузел для девочек с комнатой личной гигиены	17,78	
417	Санузел для персонала	3,49	
		831,49 м²	

- Условные обозначения
- Существующие стены
 - Восстановление кирпичной кладки
 - Утепление минераловатой
 - Замена перегородки из гипсового полнотелого кирпича, толщиной 125мм
 - Замена перегородки из газобетона, толщиной 125мм, плотность D600
 - Замена обшивки на ГКЛВ
 - Замена внутренних вентри
 - Номер помещения
 - Отметка чистого пола

2024-00375-00-0-AP			
Здания Государственного бюджетного общеобразовательного учреждения города Москвы "Школа № 1574", расположенного по адресу: г. Москва, пер. Староименинский, д. 5			
Уч. Заказчик	Исполнитель	Пол. Дир.	Лист
Роспотреб.	Роспотреб.	Роспотреб.	11.25
ГМП	Плмус	Плмус	11.25
Н.Контр.	Н.Контр.	Н.Контр.	11.25
Капитальный ремонт			Страница
План 3-го этажа, план 4-го этажа			Лист
			Листов
			3
			МОСКВИНПРОЕКТ



Экспликация помещений 5 этажа			
Номер помеще-ния	Наименование	Площадь, м2	Кат. помеще-ния
501	Лестничная клетка тип П1	35,72	
502	Кабинет иностранного языка для подгруппы	28,66	
503	Учебный кабинет для изучения естественных наук (химия)	73,11	
504	Лаборантская кабинета химии	19,30	B3
505	Серверная	9,05	B4
506	Кабинет информационных технологий	130,09	
507	Кабинет географии	62,36	
508	Кабинет русского и литературы	60,25	
509	Лестничная клетка тип Н2	23,94	
510	Лаборантская кабинета физики	25,30	B3
511	Учебная кабинета для изучения естественных наук: физика	86,65	
512	ПУИ	4,50	B4
513	Санузел для мальчиков	21,05	
514	Кабинет иностранного языка для подгруппы	37,22	
515	Коридор	206,19	
516	Санузел для девочек с комнатой личной гигиены	17,75	
517	Санузел для персонала	3,50	
		844,64 м²	

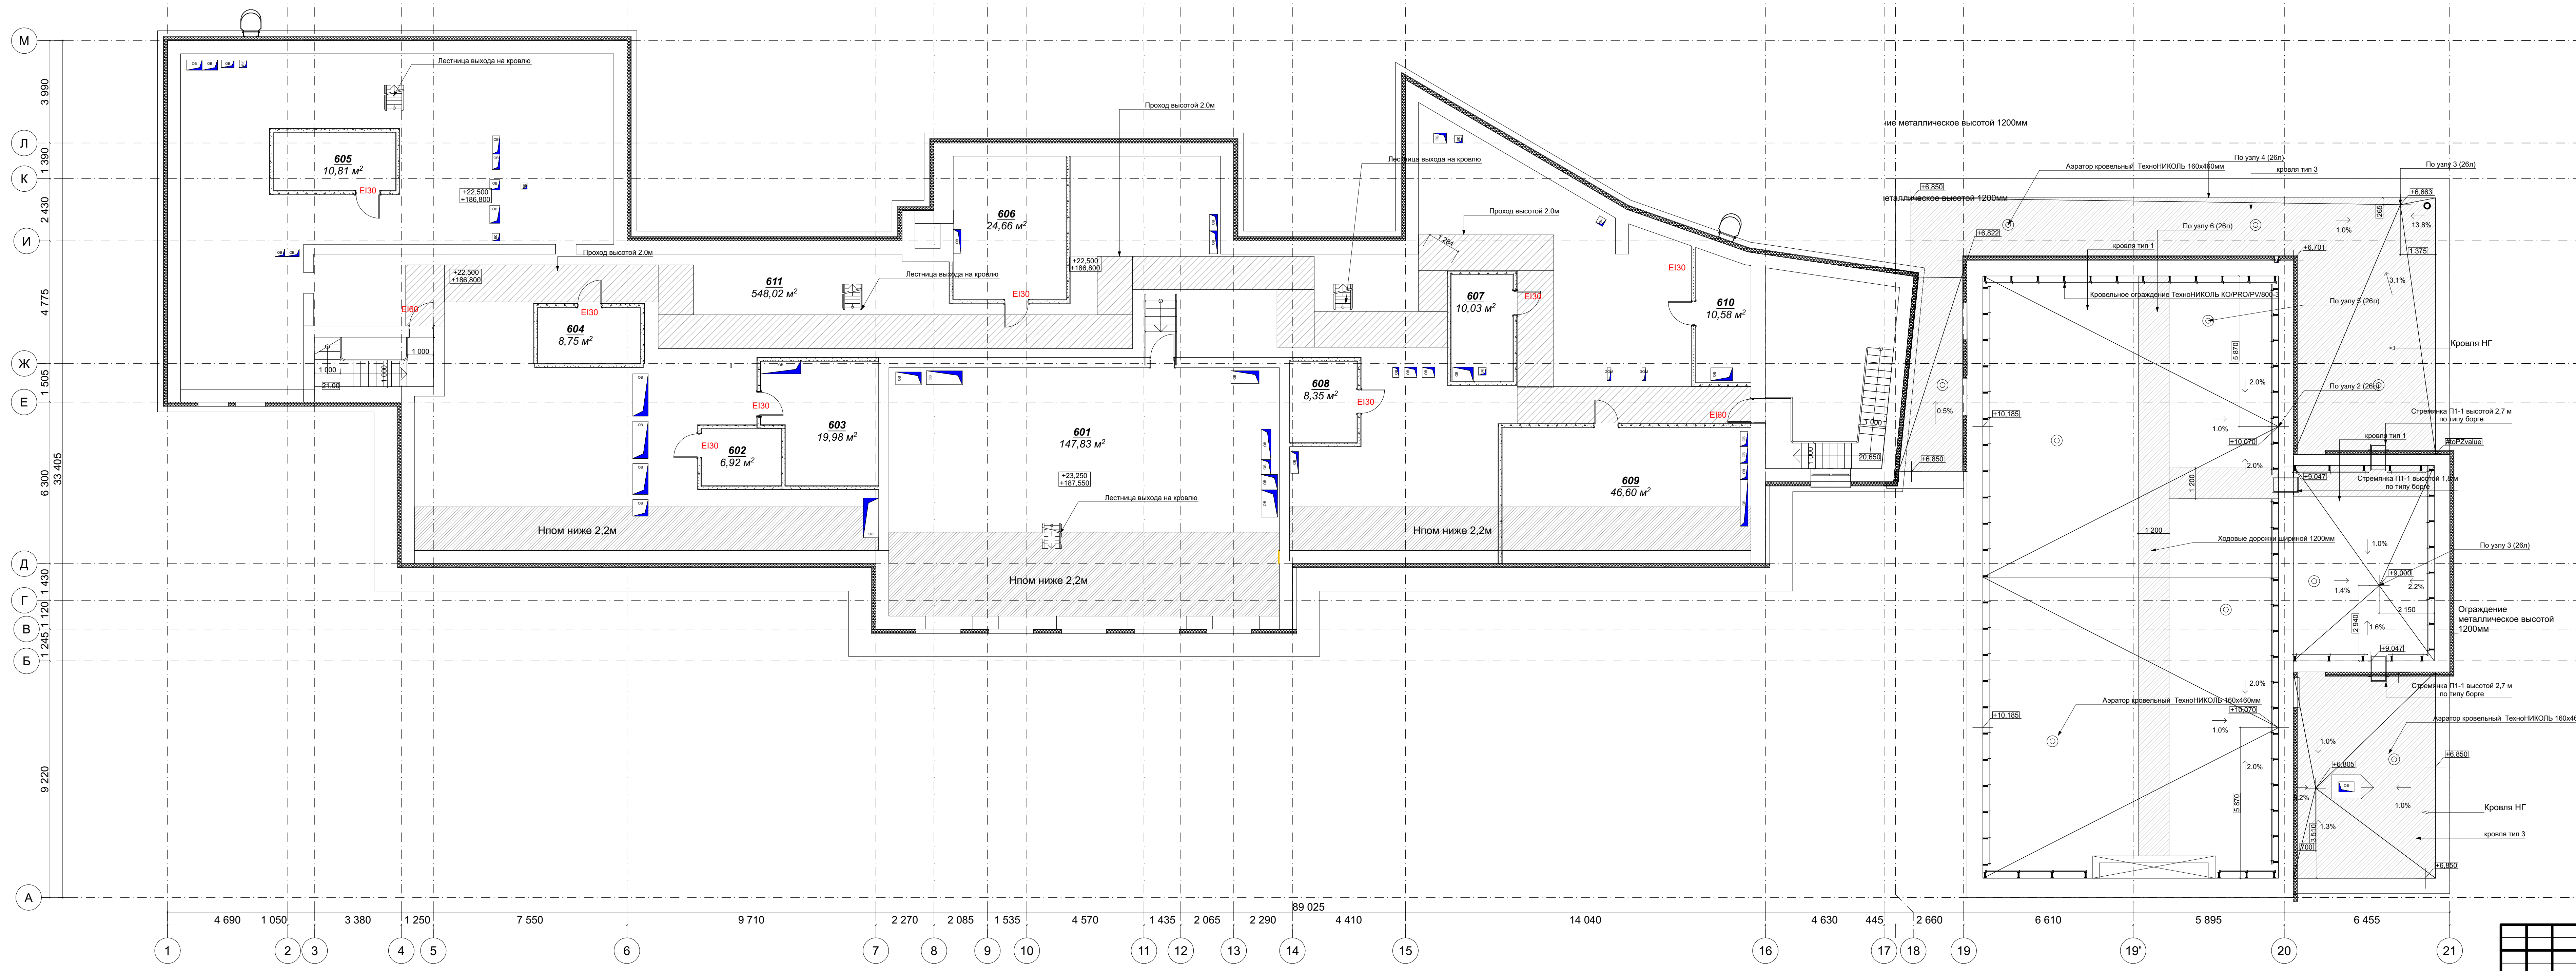


Экспликация помещений чердака			
Номер помеще-ния	Наименование	Площадь, м2	Кат. помеще-ния
601	Вытяжная вентиляция	147,83	B3
602	Вытяжная вентиляция	6,92	B3
603	ПД вентиляция	19,98	B3
604	ДУ вентиляция	8,75	B3
605	Вытяжная вентиляция	10,81	B3
606	Приточная вентиляция	24,66	B3
607	ДУ вентиляция	10,03	B3
608	ДУ вентиляция	8,35	B3
609	Вытяжная вентиляция	46,60	B3
610	ПД вентиляция	10,58	B3
611	Техническое помещение	548,02	B4
		842,53 м²	

Условные обозначения			
	Существующие стены		Восстановленные перегородки
	Восстановленные перегородки		Утеплитель минераловатный
	Утеплитель минераловатный		Заменяемая паркетная из лиственных породных пород, толщиной 120мм
	Заменяемая паркетная из лиственных породных пород, толщиной 120мм		Заменяемая паркетная из лиственных породных пород, толщиной 120мм
	Заменяемая паркетная из лиственных породных пород, толщиной 120мм		Заменяемая облицовка из ПВХ
	Заменяемая облицовка из ПВХ		Заменяемые внутренние вентили

120 - Номер помещения
89,0 м² - Отметка чистого пола
0,000

2024-00375-00-0-AP			
Здания Государственного бюджетного общеобразовательного учреждения города Москвы "Школа № 1574", расположенного по адресу: Москва, пер. Староименный, д. 5			
Дир. Школы	Дир. Школы	Дир. Школы	Дир. Школы
Зам. Дир. Школы	Зам. Дир. Школы	Зам. Дир. Школы	Зам. Дир. Школы
Ген. Дир. Школы	Ген. Дир. Школы	Ген. Дир. Школы	Ген. Дир. Школы
Н.Контр.	Н.Контр.	Н.Контр.	Н.Контр.
Капитальный ремонт			
План 5-го этажа; план чердака			
МОСКВИН			

1. Фасад в осях 1-21

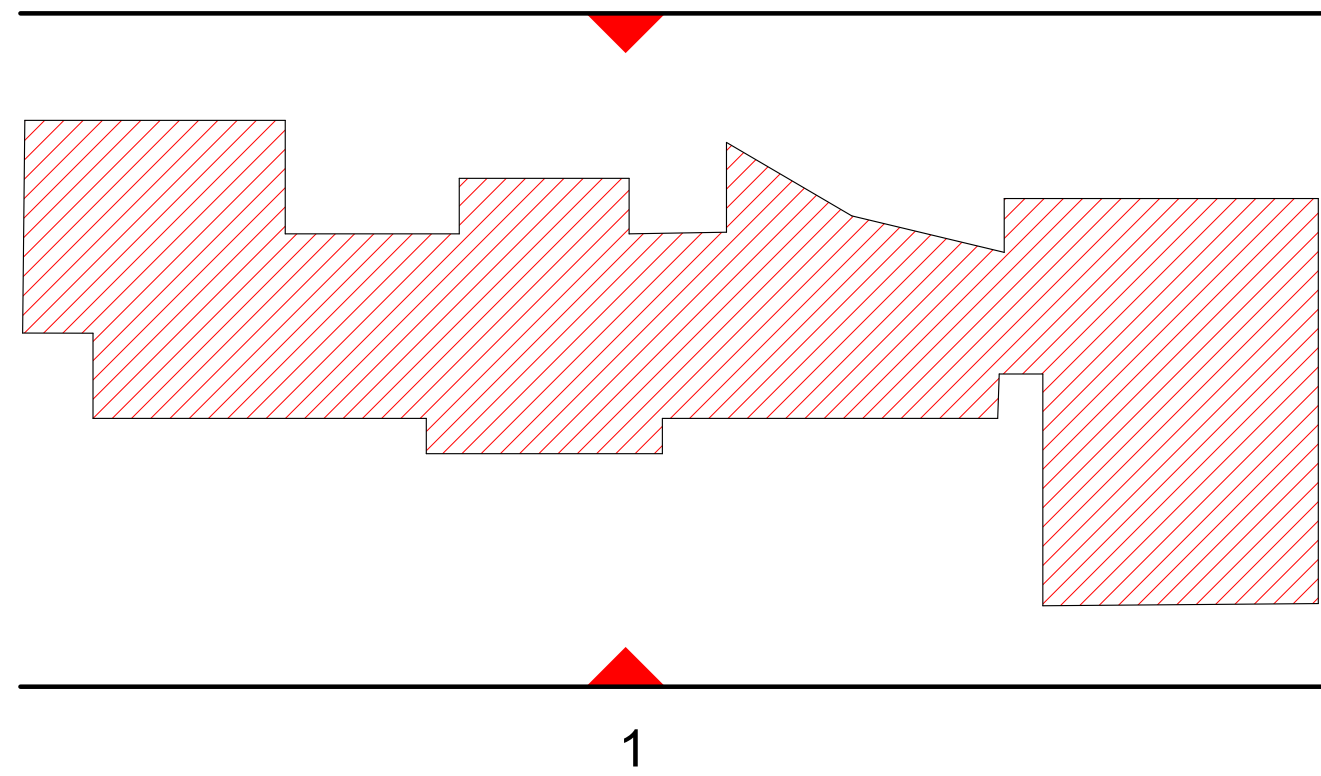[illegible]

2. Фасад в осях 21-1



							2024-00375-00-0-AP					
							Здания Государственного бюджетного общеобразовательного учреждения города Москвы "Школа № 1574", расположенного по адресу: Москва, пер. Старопановский дом 5.					
Имя	Фамилия	Лист	№ документа	Реквизиты	Дата		Страница		Лист	Листов		
Григорьев	Евгений	11	25	11-25			п		6			
Тип	Платье	11	25	11-25								
Капитальный ремонт												
Н Контроль							Выполнение					
11							25					
Фасадный												
Счетчик 00000000000000000000							1 1306-0044					